




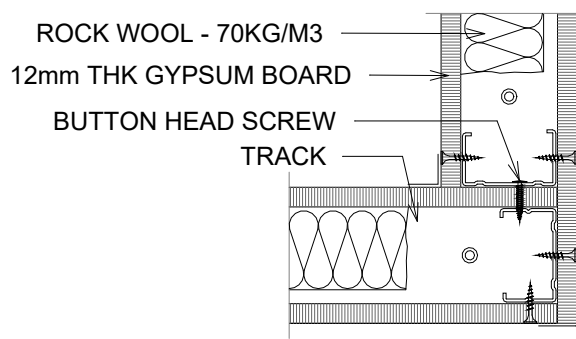


1 TYP. CORNER JOINT
1 : 5

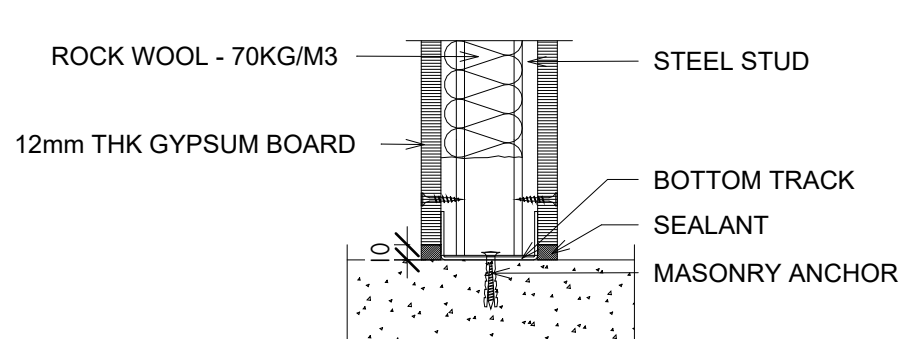


2 TYP. CONNECTION TO FLOOR
1 : 5

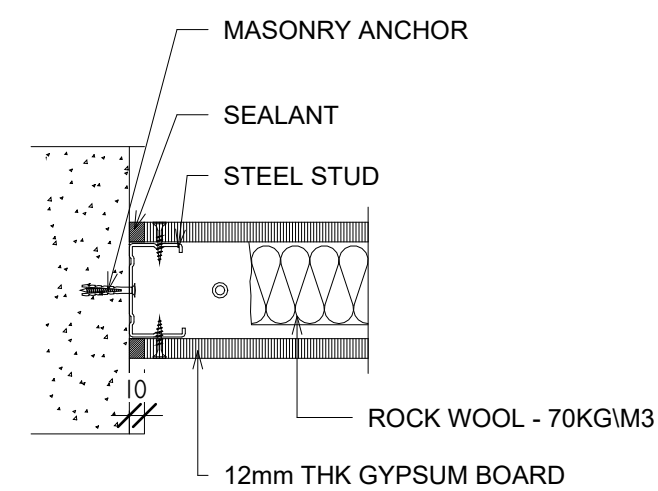


3 TYP. CONNECTION TO WALL
1 : 5

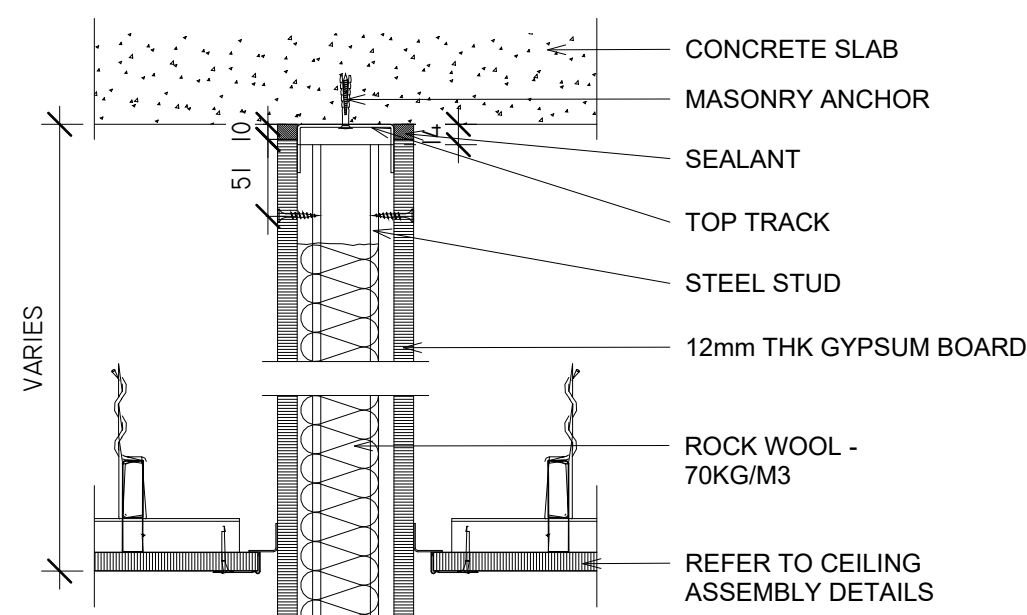


4 TYP. SOUND PROOFING
1 : 5

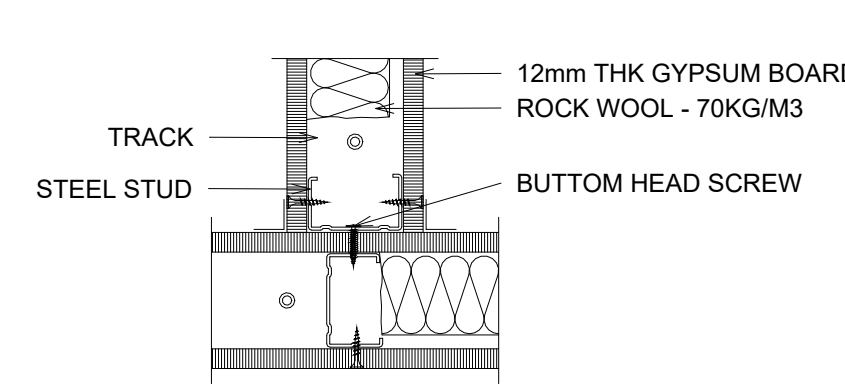


5 TYP. T-JUNCTION JOINT
1 : 5

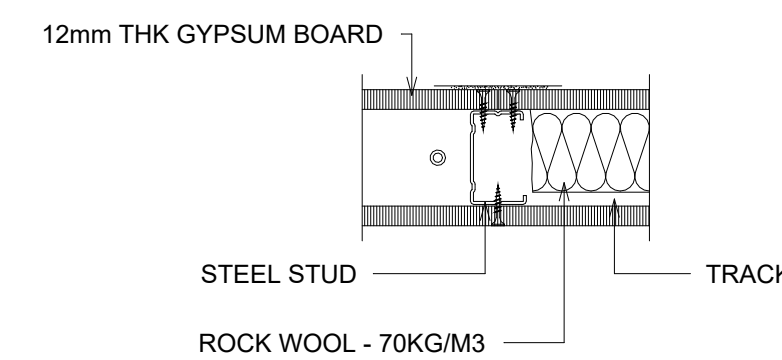


6 TYP. BUTT JOINT
1 : 5

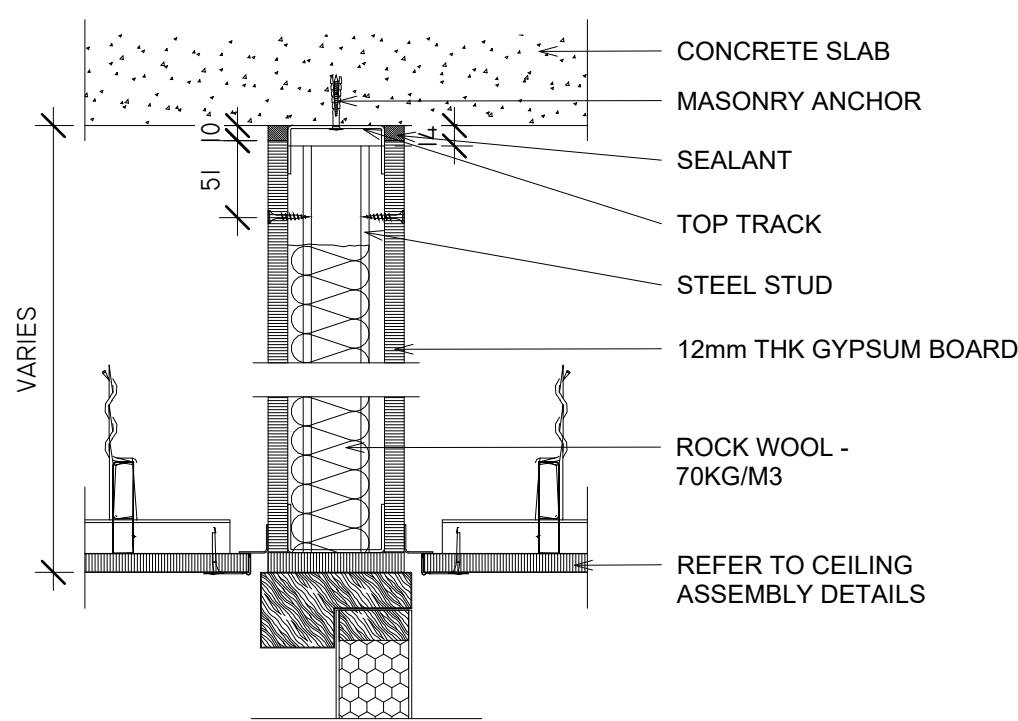


7 TYP. SOUND PROOFING DOOR
1 : 5

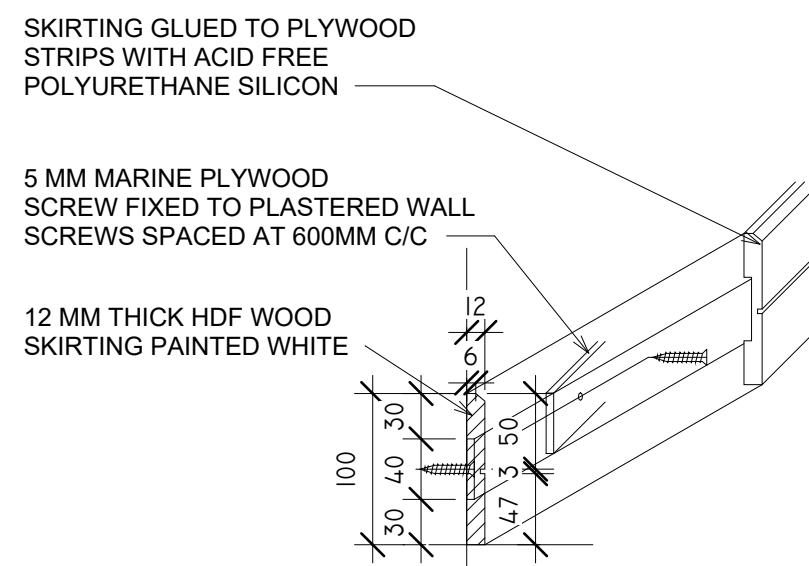


8 TYP. SKIRTING ASSEMBLY DETAIL
1 : 5

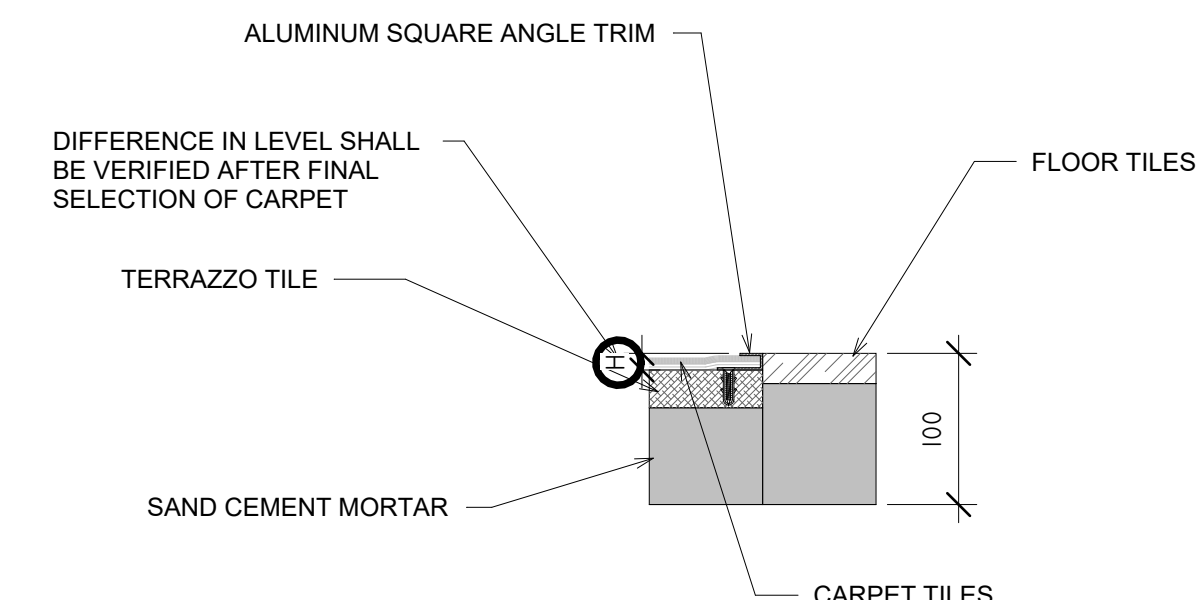


9 TYP. GRANITE CARPET DETAILS
1 : 5

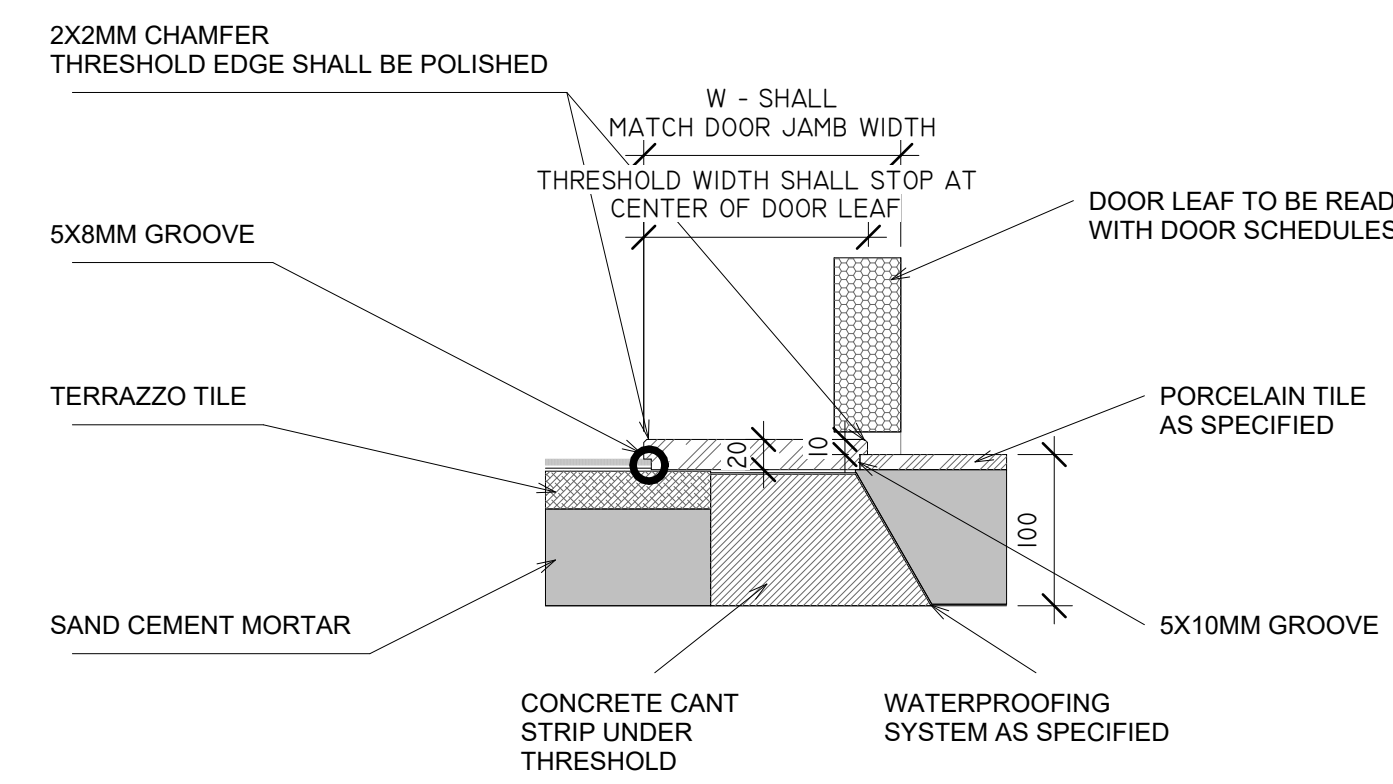

10 TYP. TOILET THRESHOLD DETAIL
1 : 5

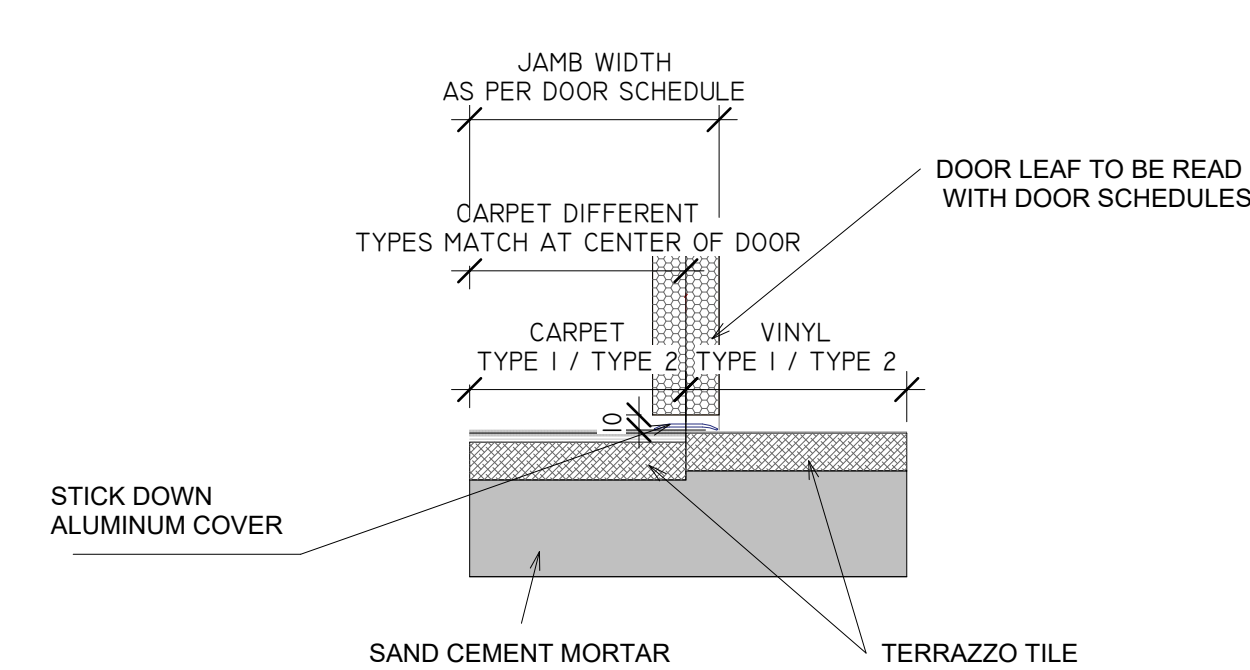


11 D-CARPET VINYL DETAIL
1 : 5

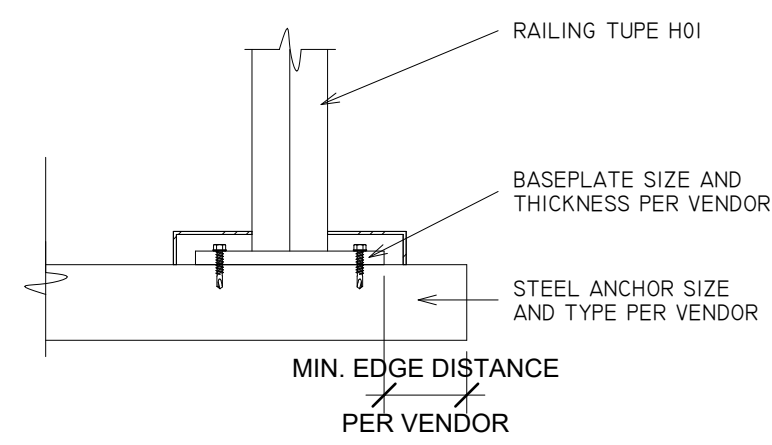


12 HANDRAIL DETAILS
1 : 5



DOOR SIZE H x W (MILLIMETERS)
300 x 300
450 x 450
600 x 600
1200 x 600

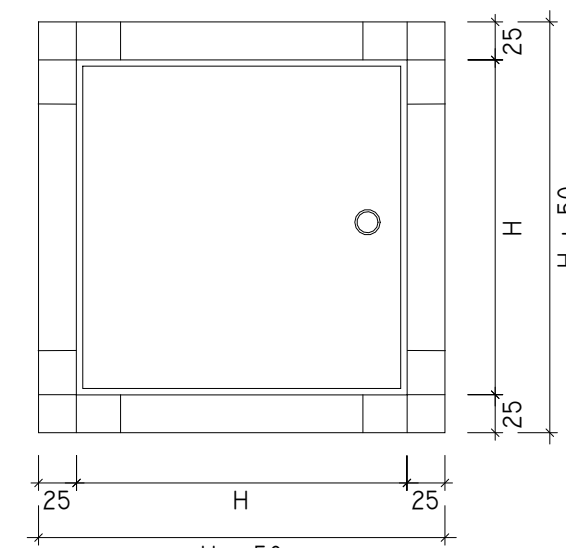


13 TYP. HINGED ACCESS PANEL PLAN
1 : 5

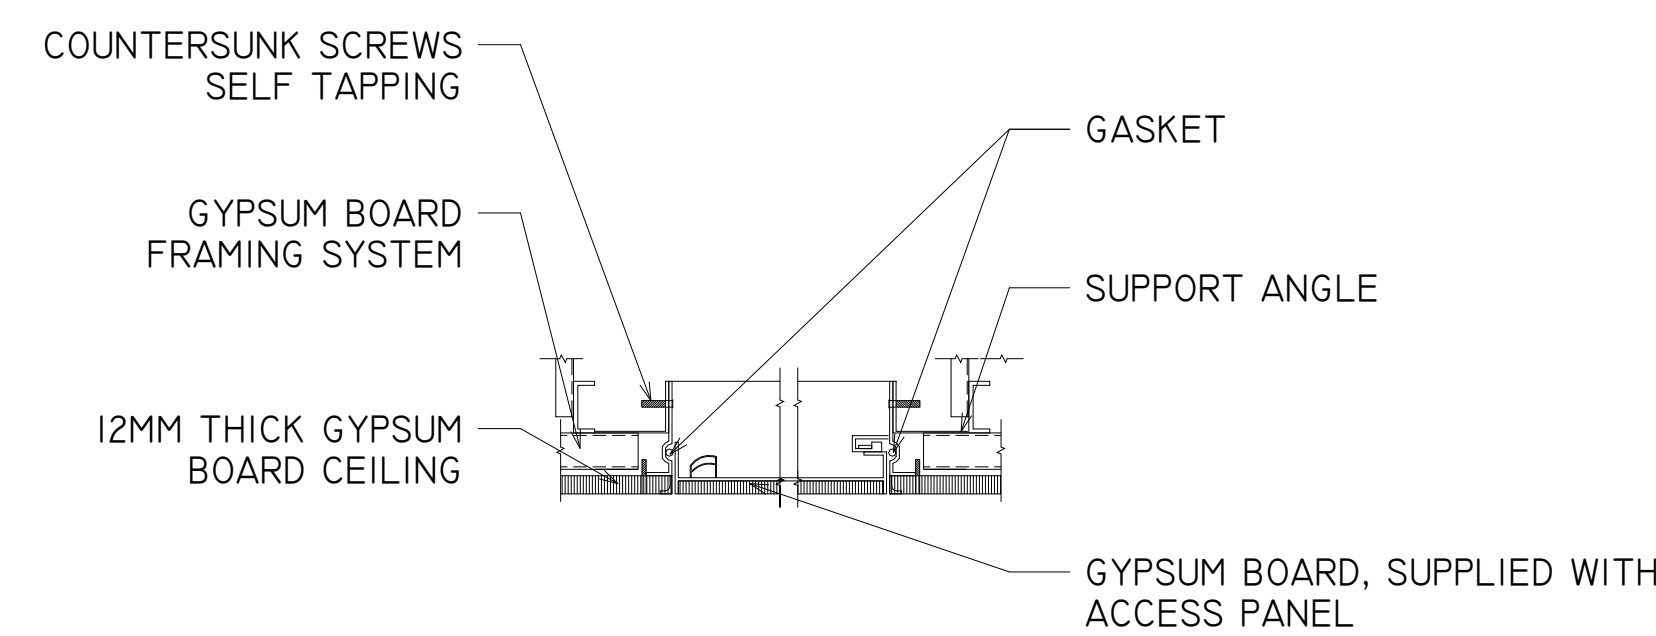


14 TYP. HINGED ACCESS PANEL SECTION
1 : 5

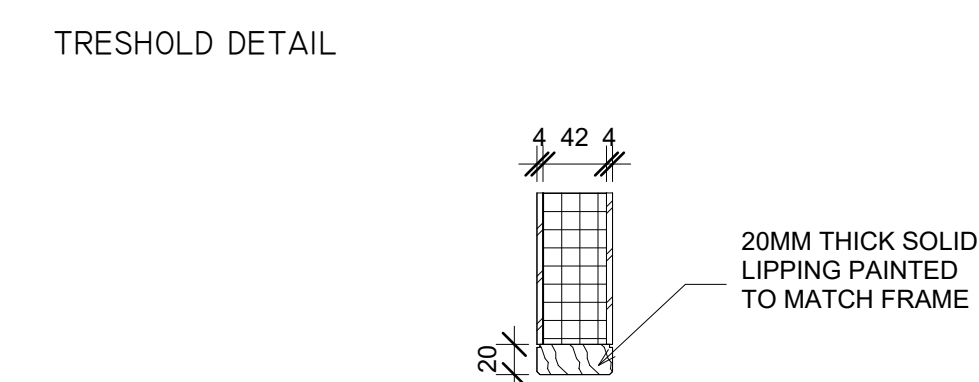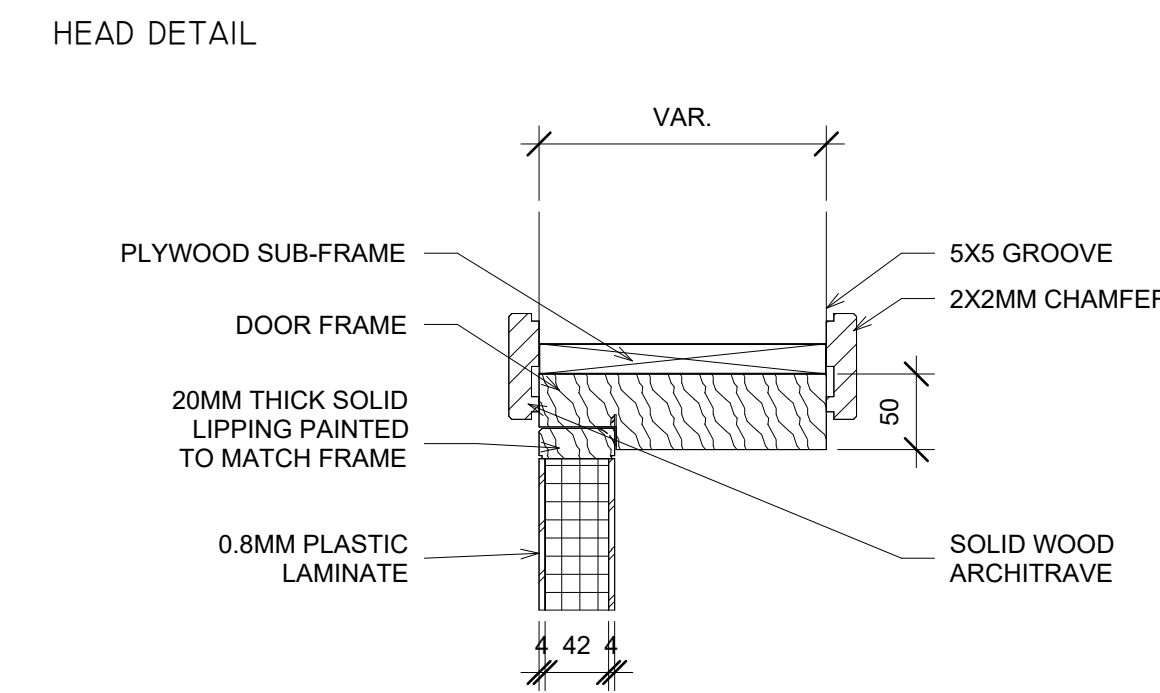


15 TYP. FLUSH WOOD DOOR DETAILS
1 : 5

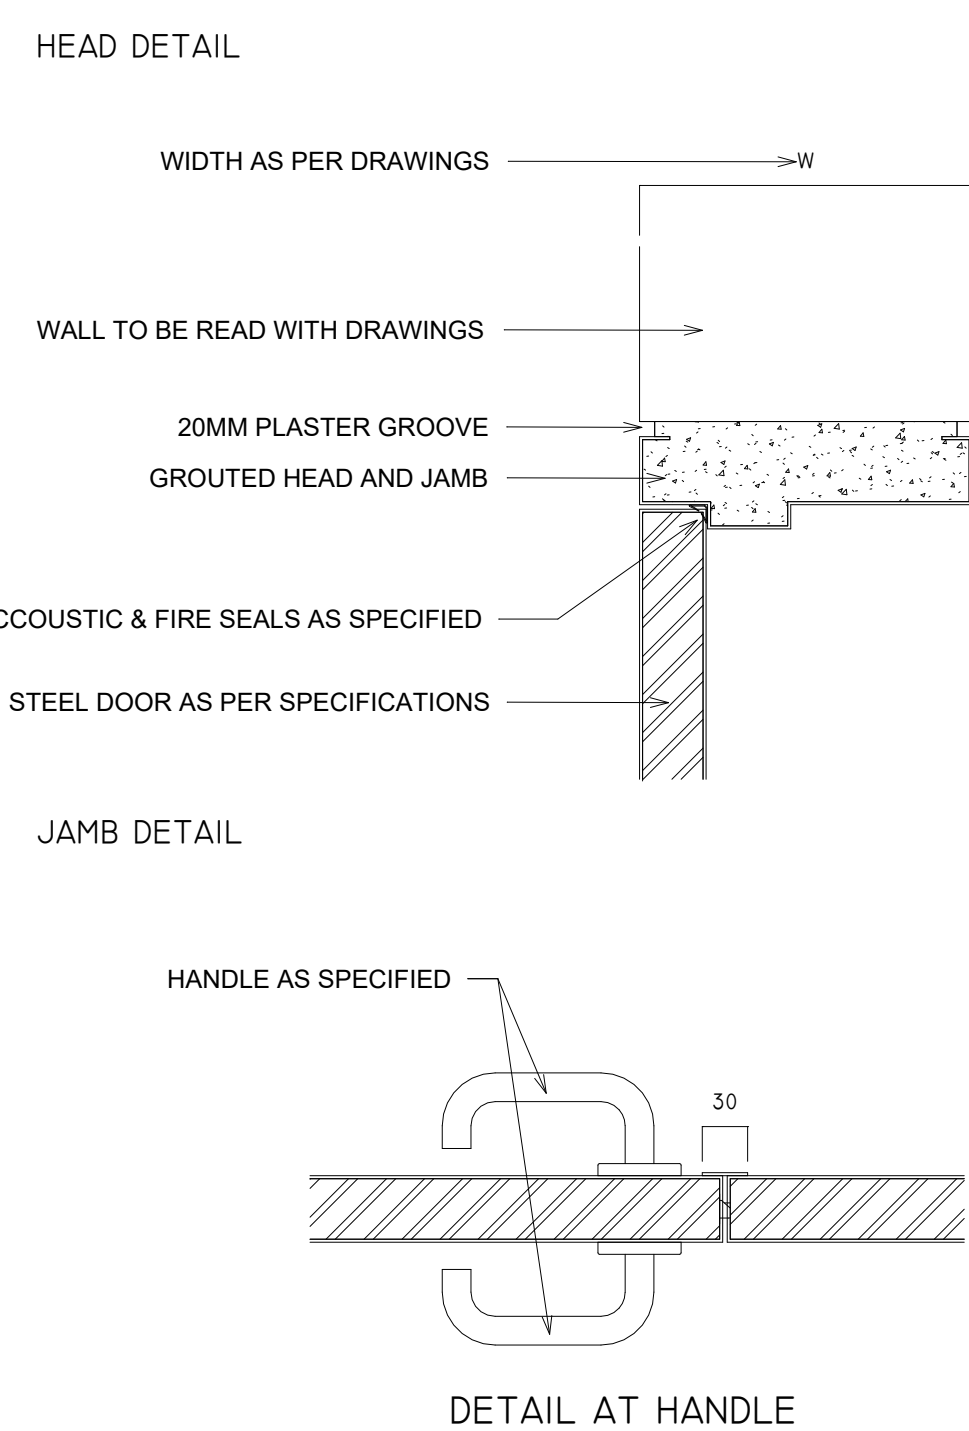


16 TYP. STEEL DOOR DETAILS
1 : 5

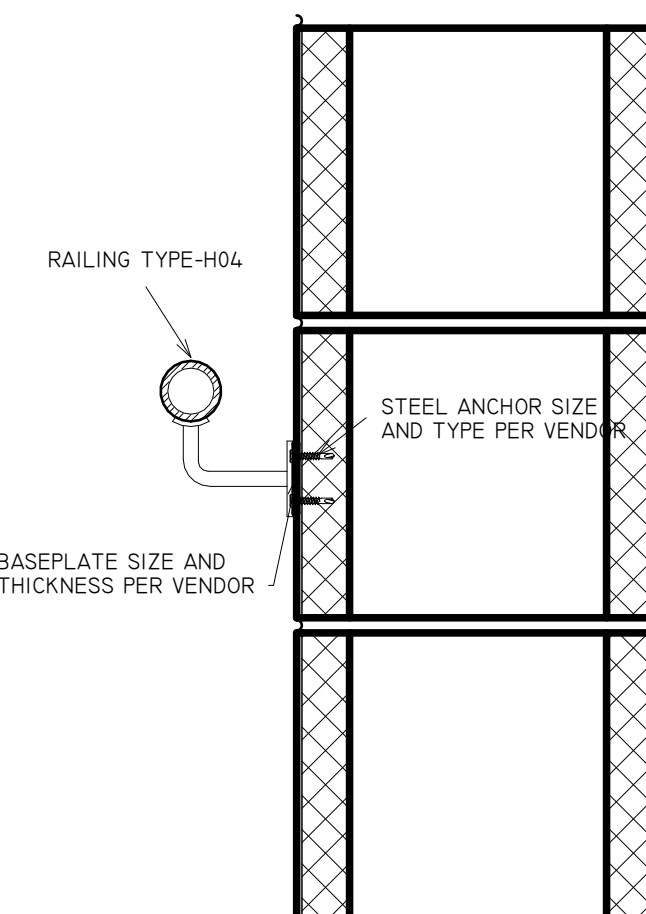


17 TYP. WALL MOUNTED HANDRAIL DETAILS
1 : 5

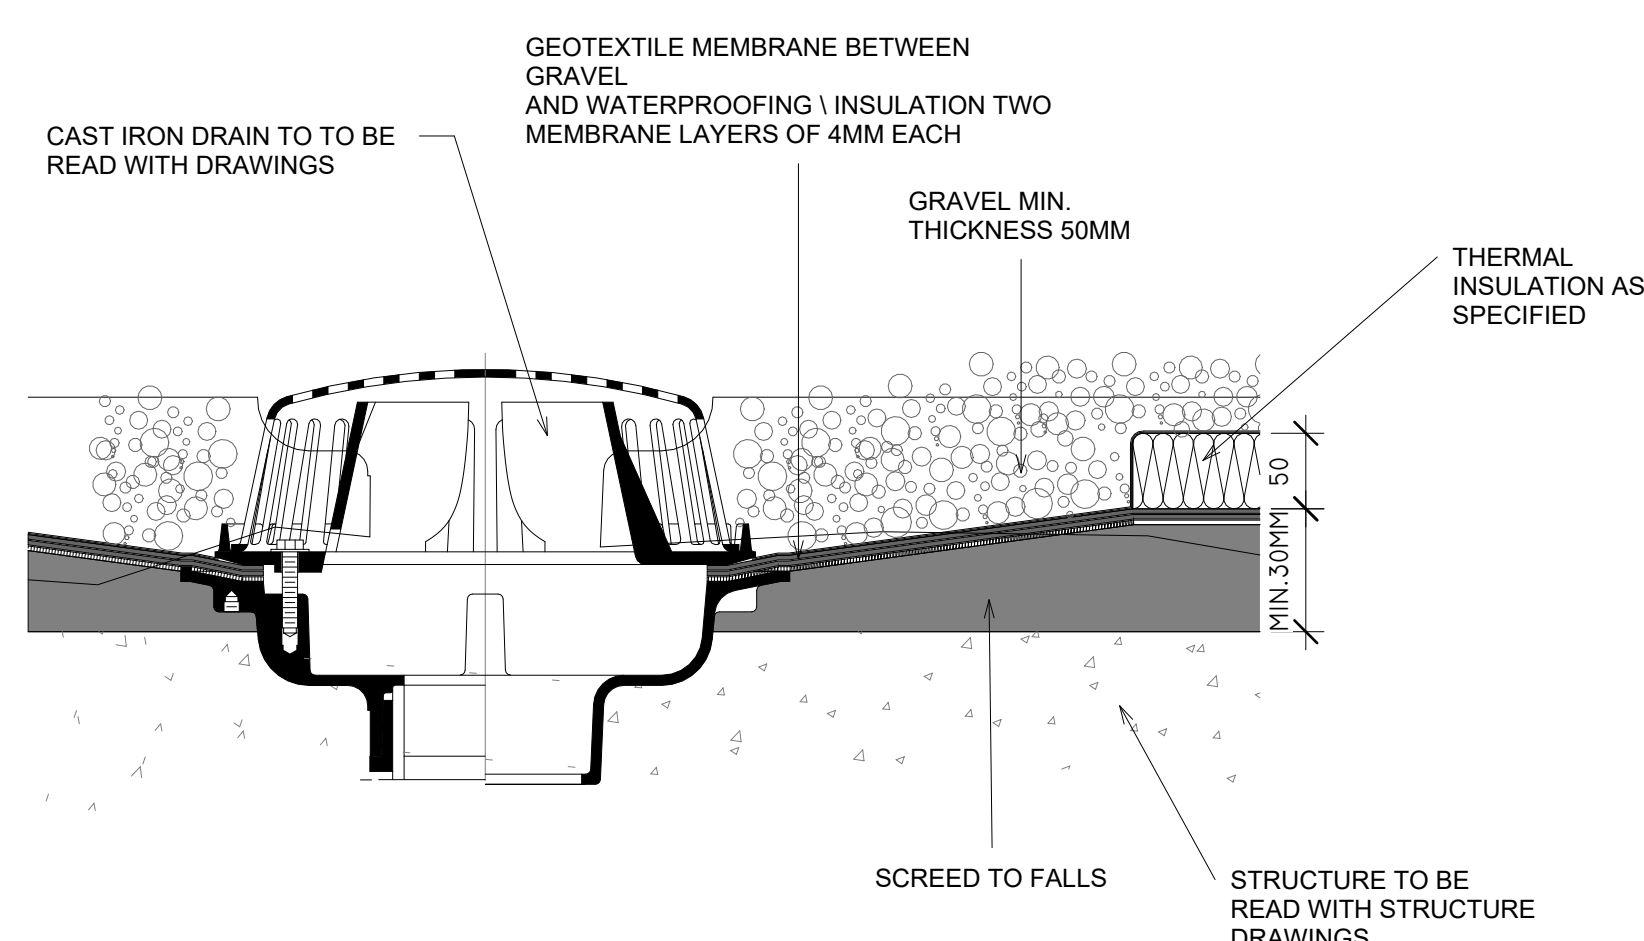

18 TYPICAL ROOF DRAINAGE DETAIL
1 : 5

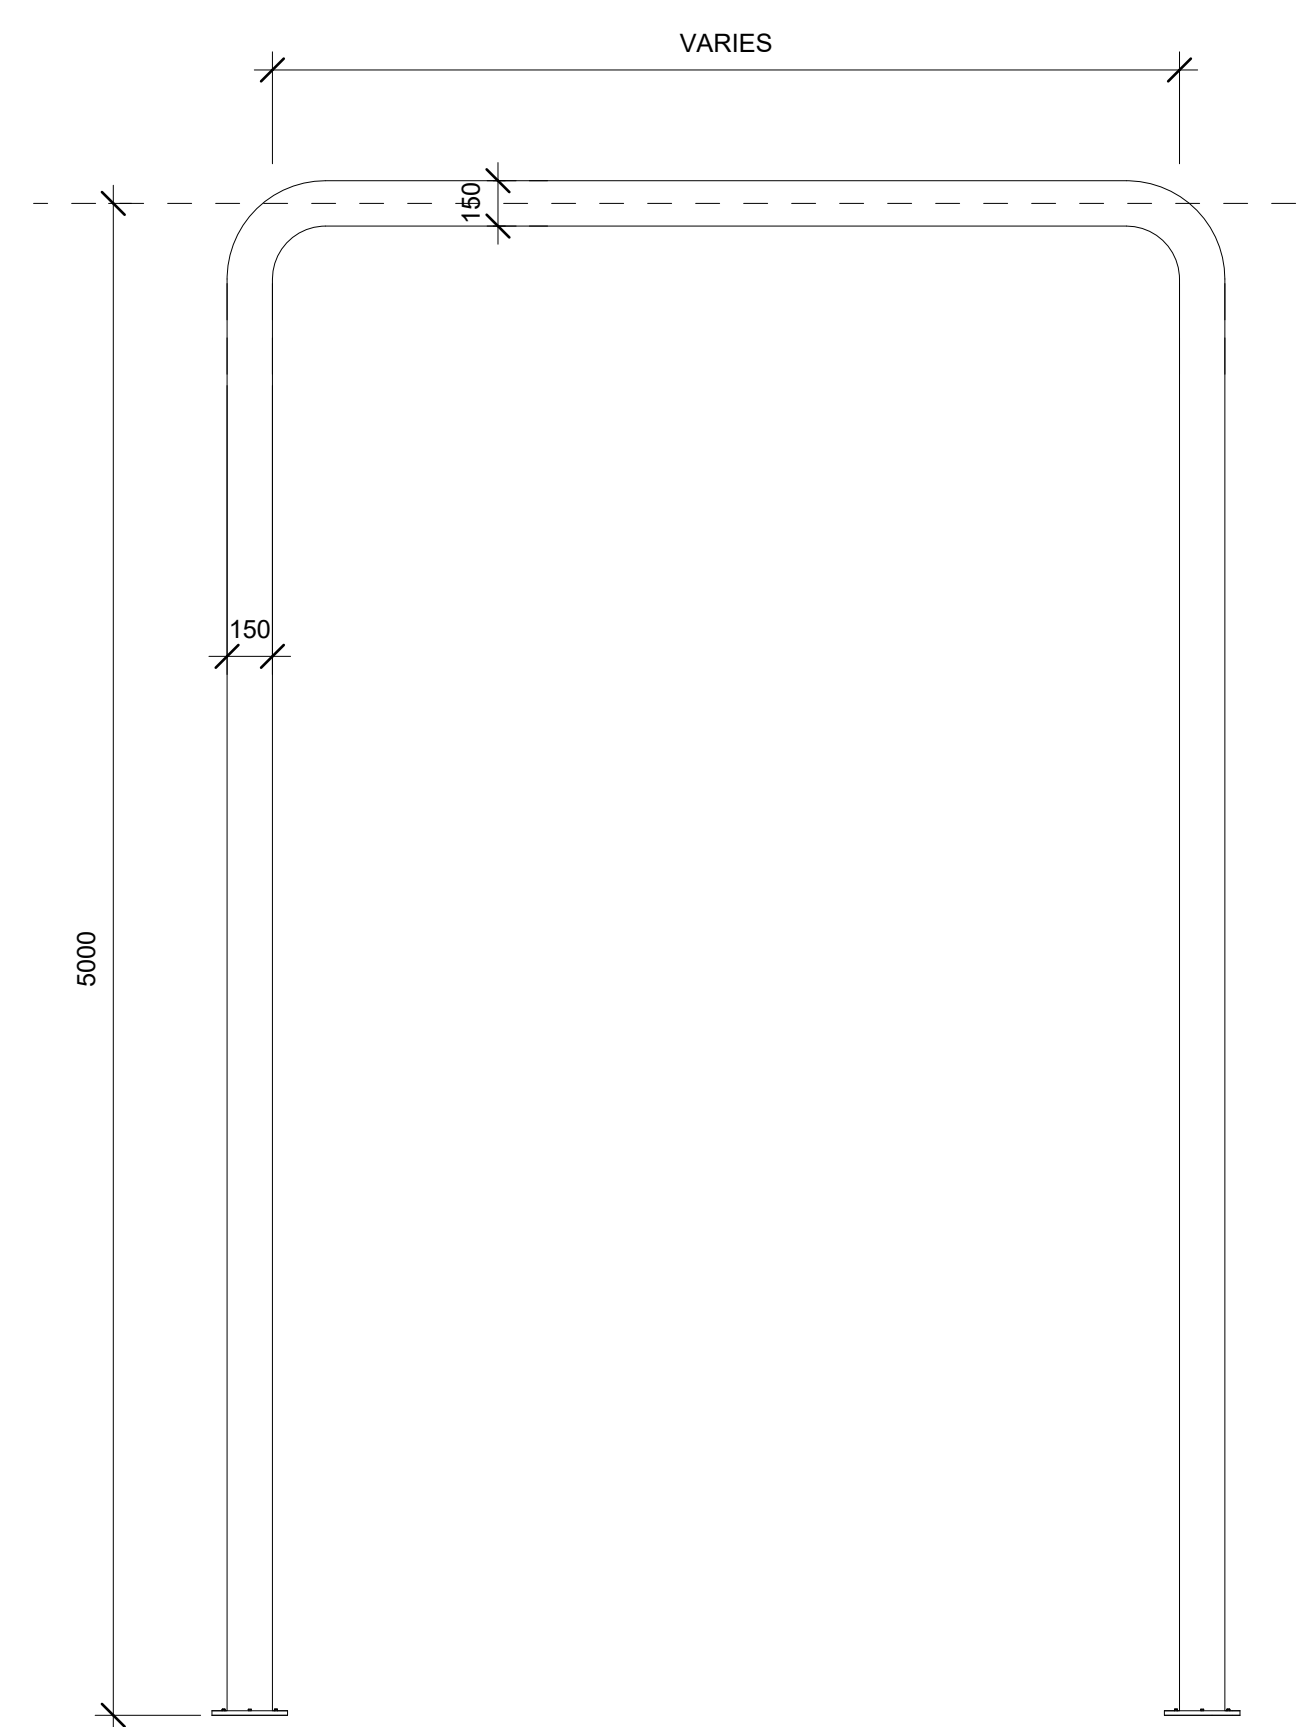

19 OVERHEAD SAFETY BARRIER (VENDOR)
1 : 25

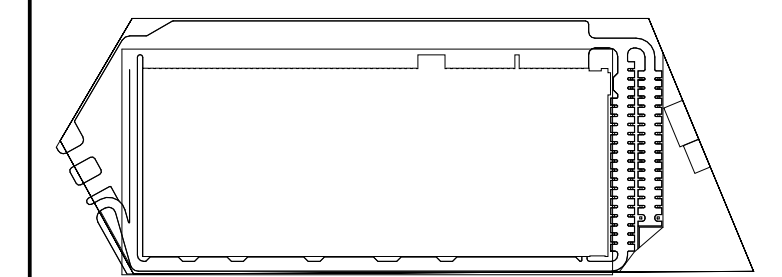

REV.	DATE	DESCRIPTION OF REVISION
00	23/05/2025	ISSUE FOR DETAILED DESIGN
01	18/08/2025	ISSUE FOR DETAILED DESIGN
02	11/12/2025	ISSUE FOR DETAILED DESIGN

DRAWN BY	CHECKED BY	DATE (DD.MM.YYYY)
IBR	ALN	22.05.2025