




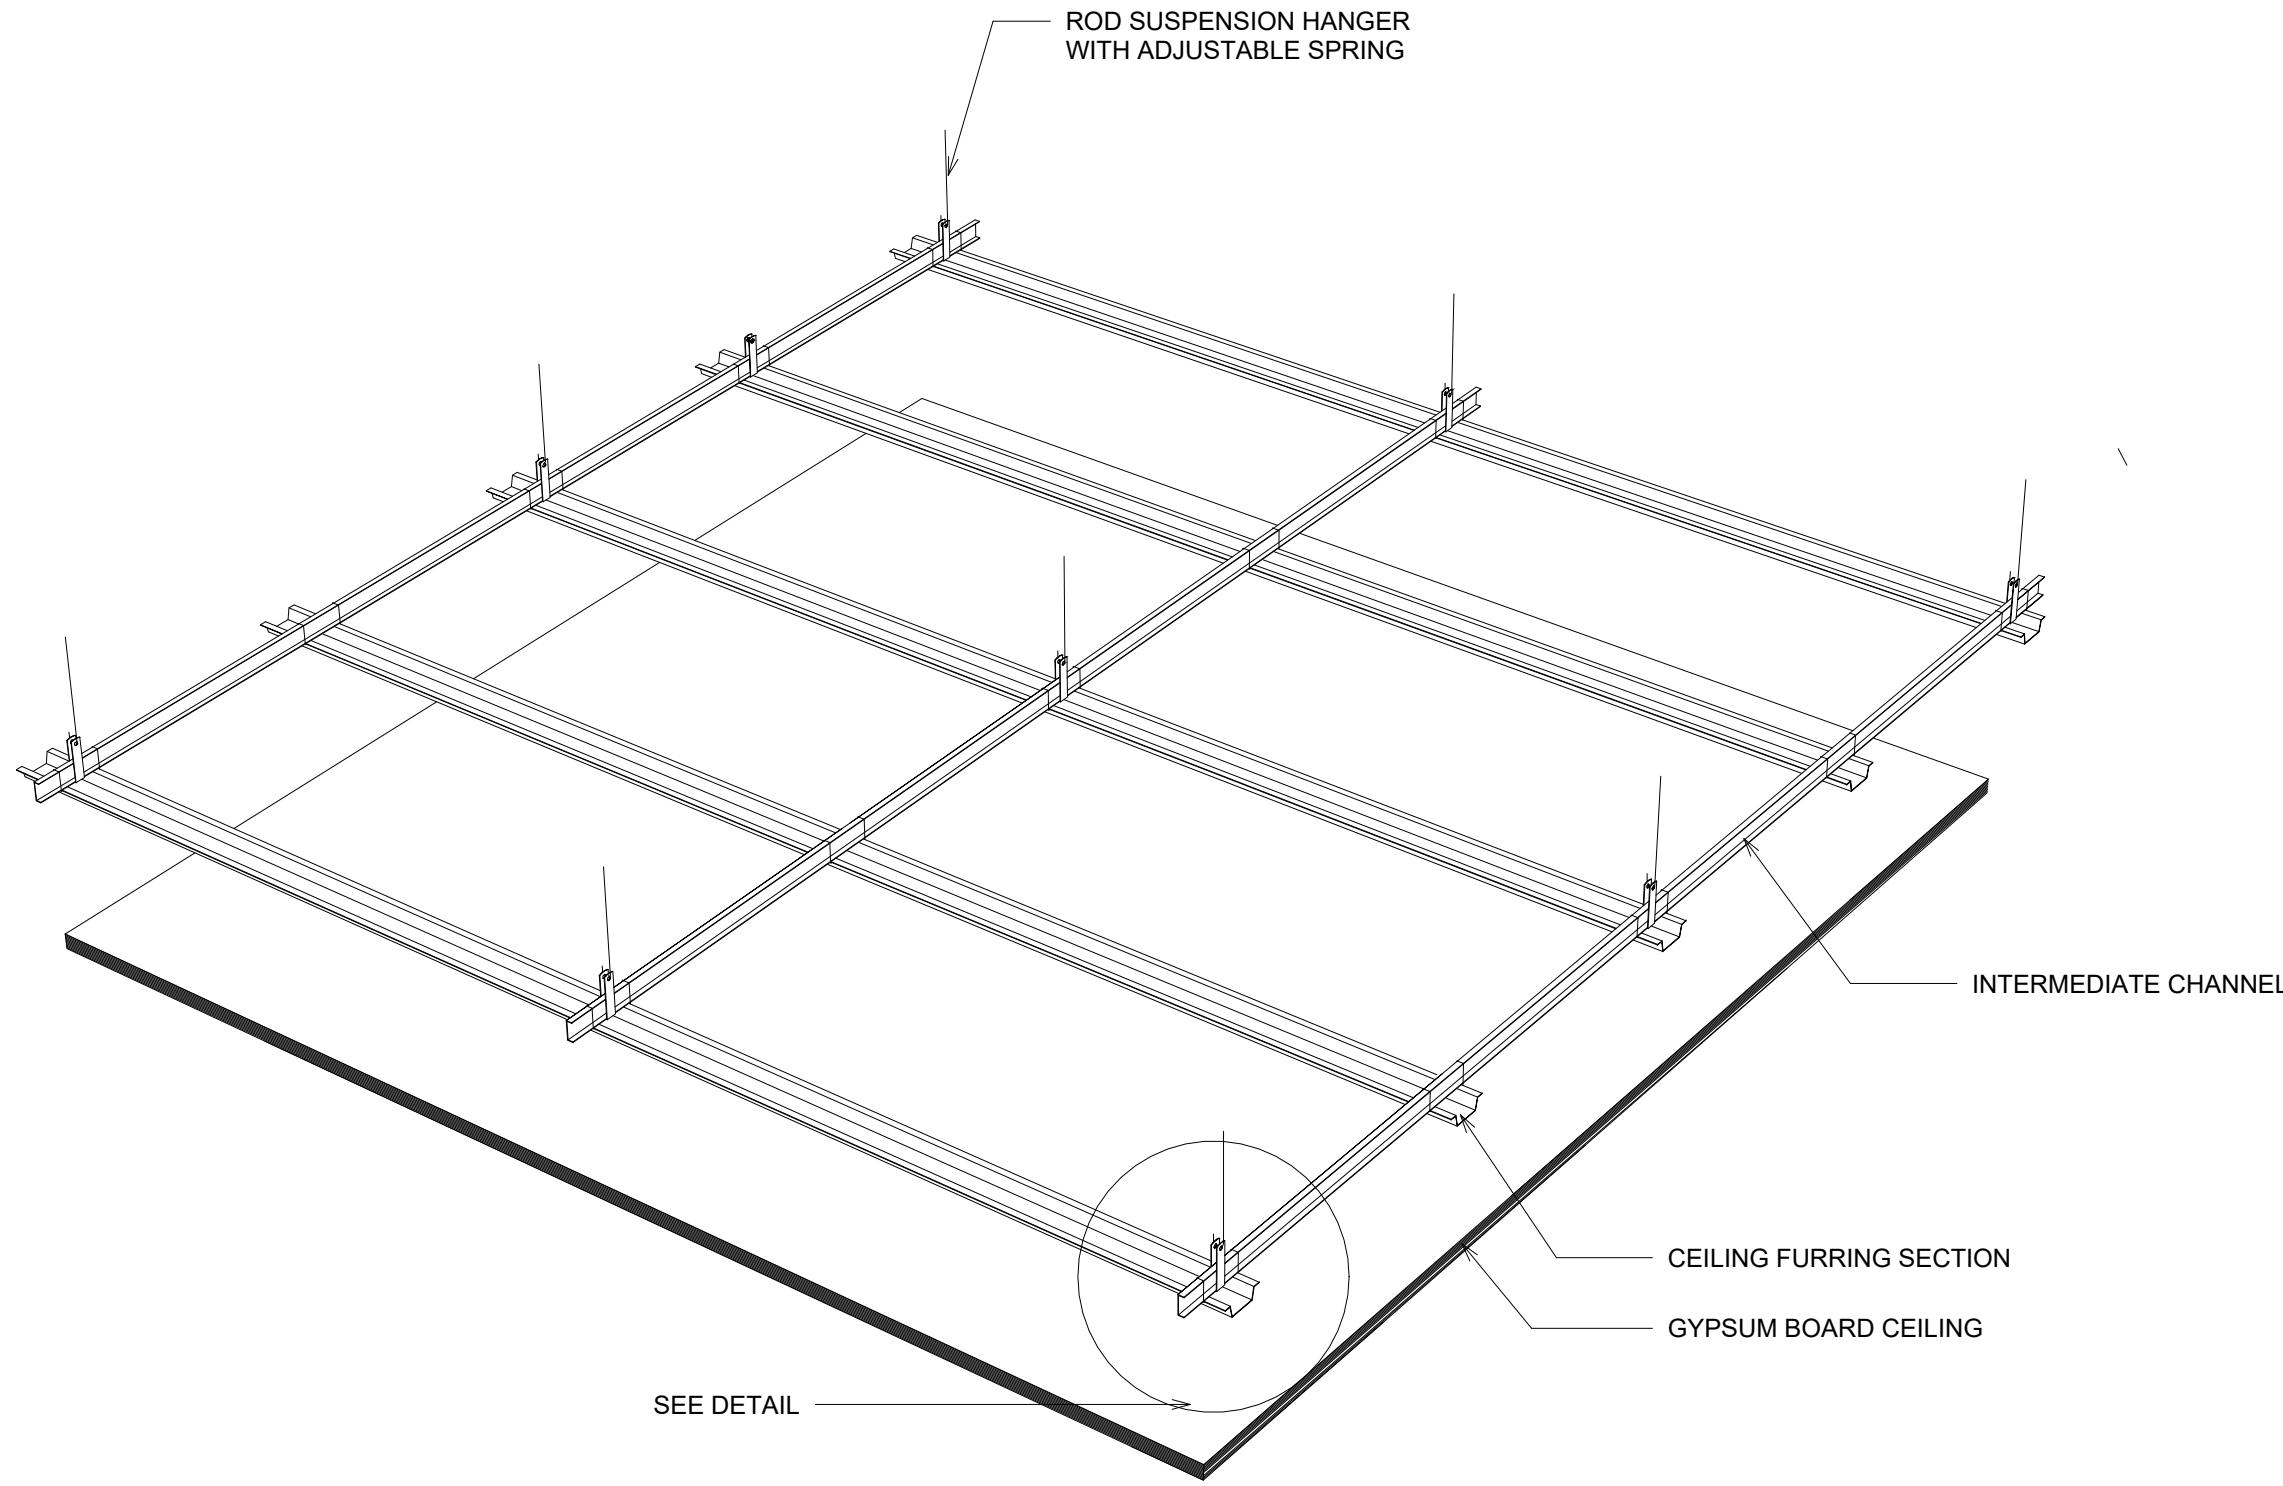


1 TYPICAL 3D VIEW - GYPSUM BOARD CEILING
1 : 100

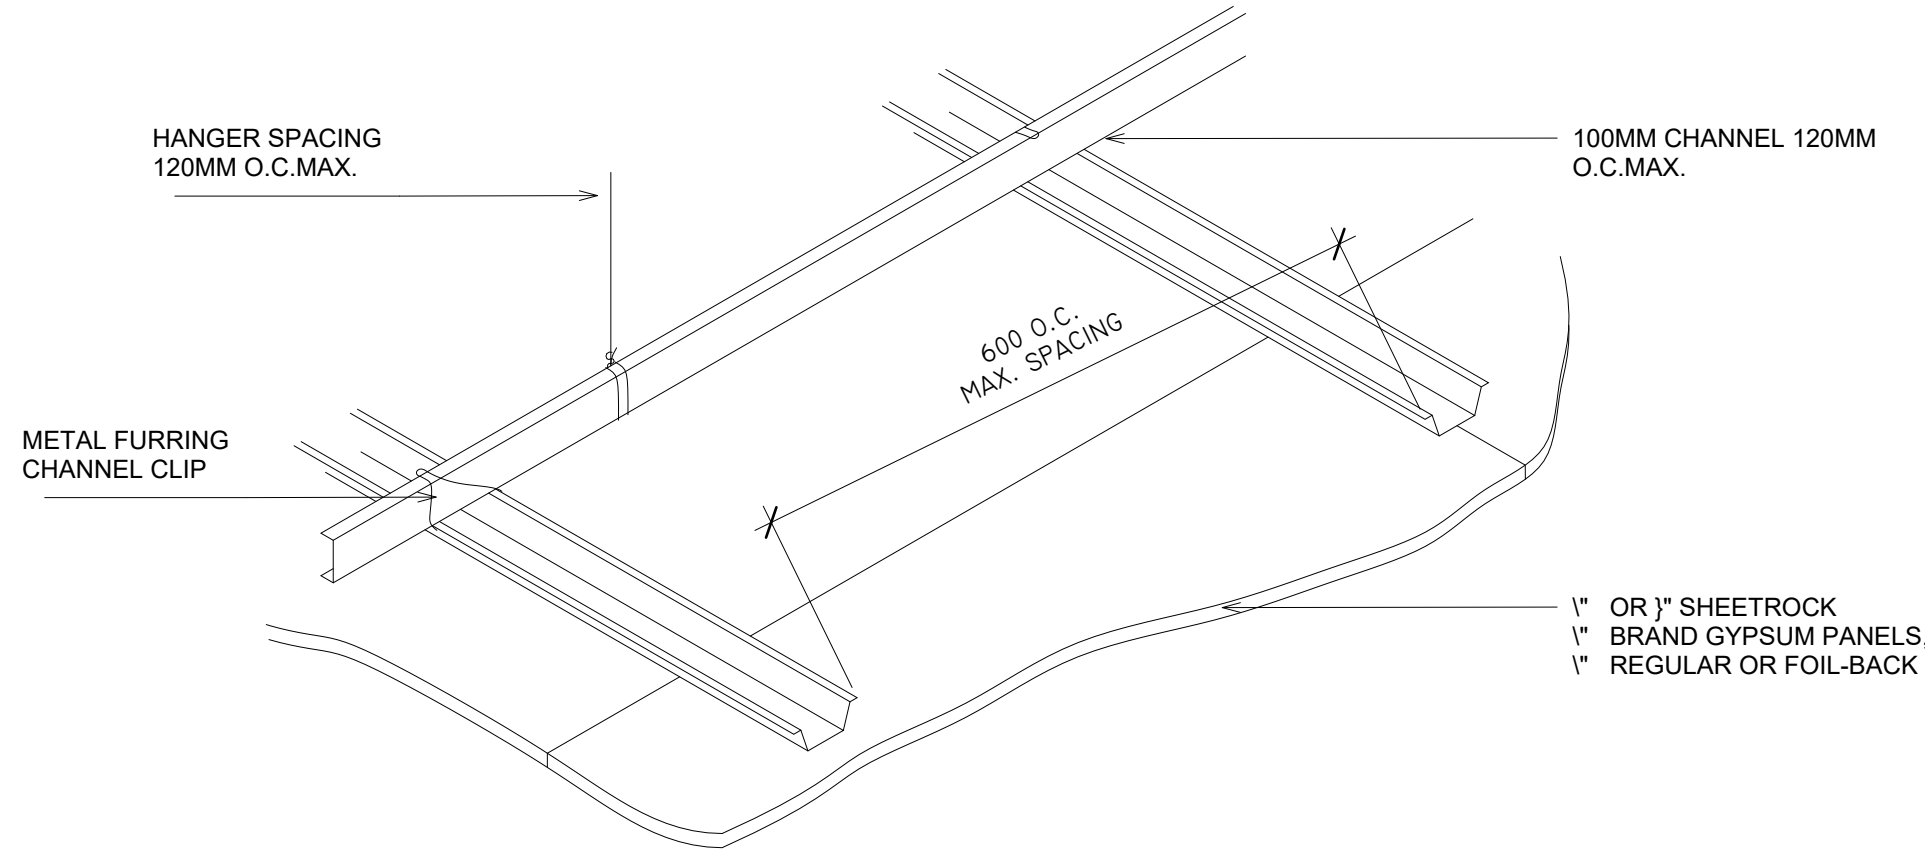


2 TYP. 3D GYPSUM STEEL FRAMED FURRING CHANNEL
1 : 5

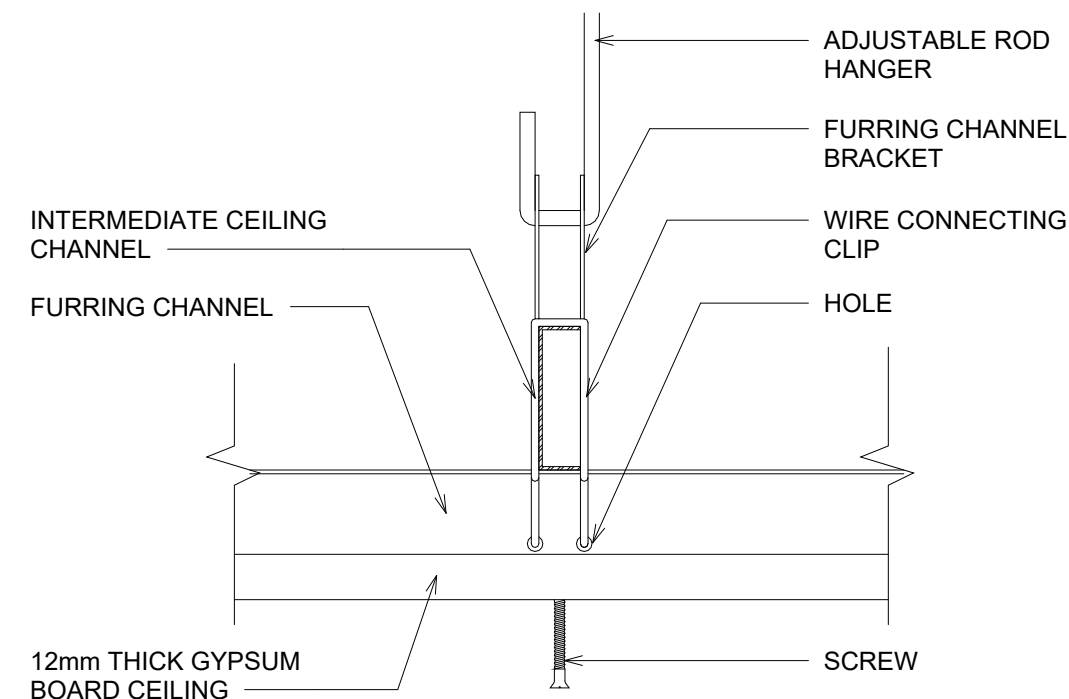


3 SECTION AT INTERMEDIATE CHANNEL
1 : 100

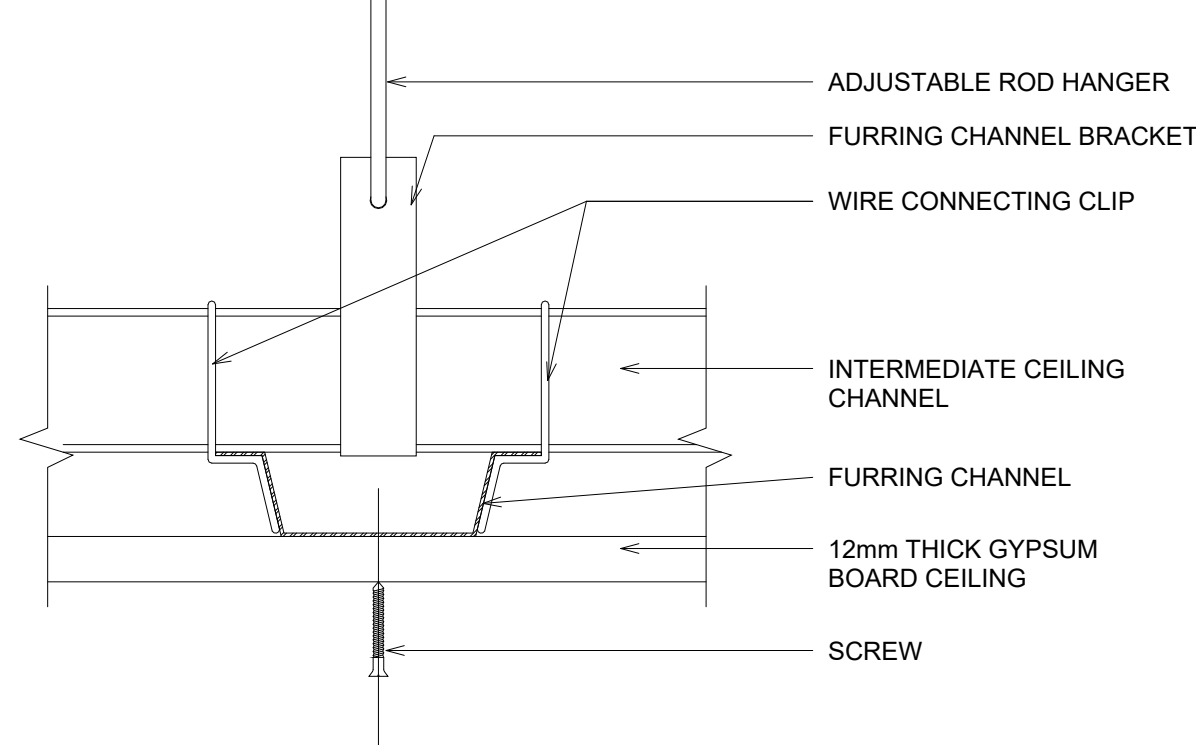


4 SECTION AT FURRING CHANNEL
1 : 100

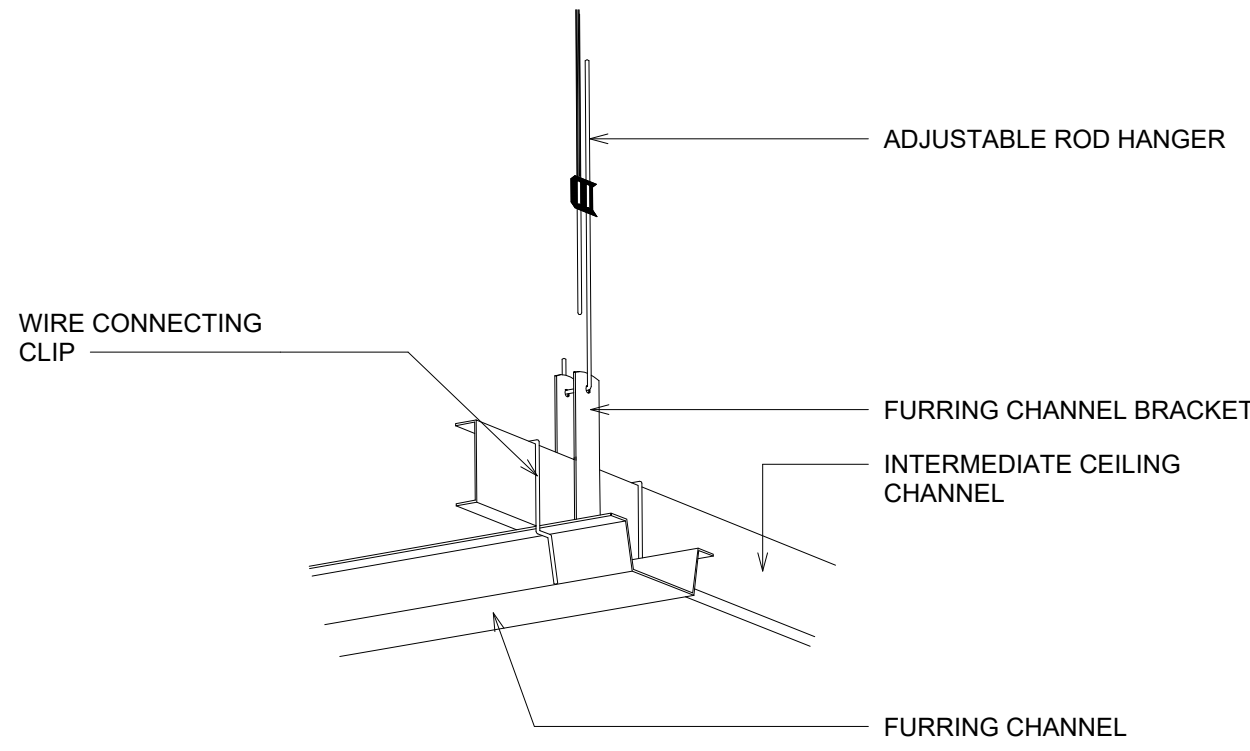


5 ISOMETRIC DETAIL
1 : 100

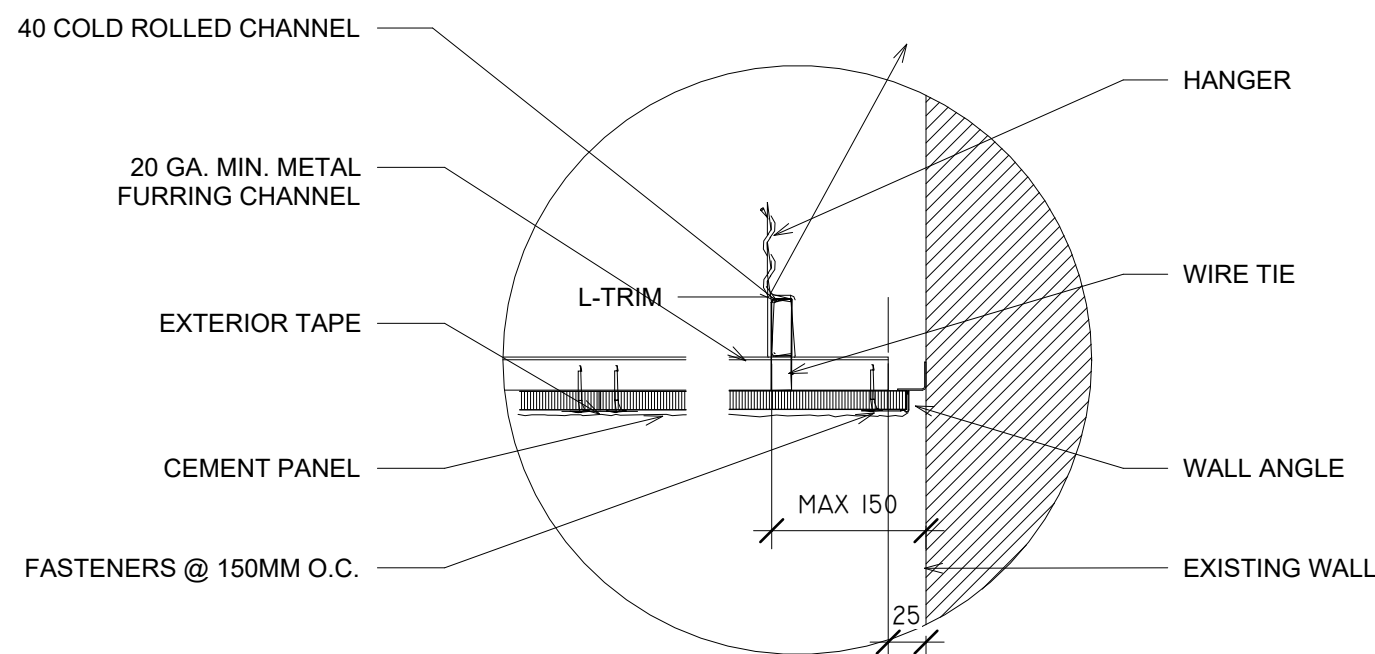

6 GYPSUM WALL INTERSECTION
1 : 5

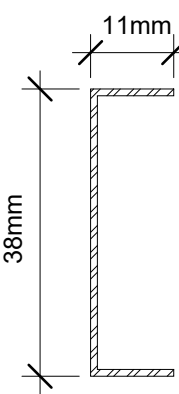


7 INTERMEDIATE CEILING CHANNEL
1 : 100

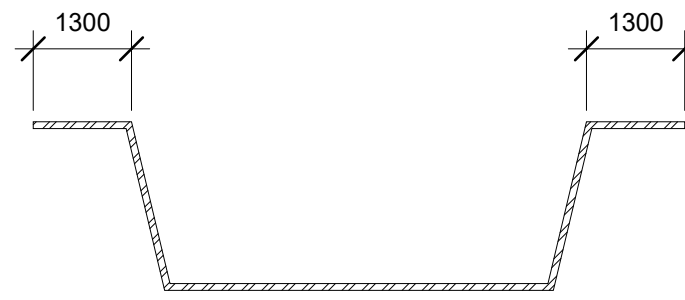

8 FURRING CHANNEL
1 : 100

KEY PLAN :

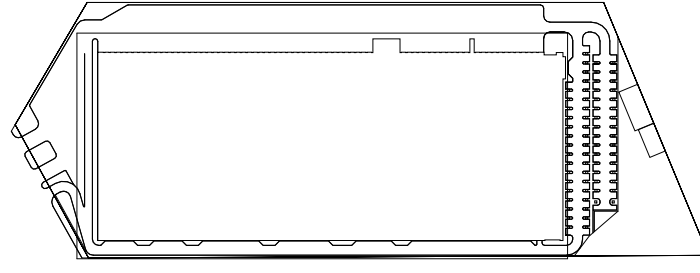

REV.	DATE	DESCRIPTION OF REVISION
00	11/12/2025	ISSUE FOR DETAILED DESIGN

SEAL & SIGNATURE:

DRAWN BY	CHECKED BY	DATE (DD.MM.YYYY)
IBR	ALN	22.05.2025

NUPCO WAREHOUSE
ASEER, KSA

CLIENT:



PROJECT MANAGER:



PROJECT PROGRAM MANAGER



ARCHITECTURE & ENGINEERING CONSULTANT:



PHASE & DISCIPLINE:

DETAIL DESIGN
ARCHITECTURE


DRAWING TITLE:

MISCELLANEOUS DETAILS
2/4


PROJECT NO.	DRAWING NUMBER	REV
102	RCC-NPC-ASR-ARC-DD-00701	00

SCALE (A0)


AS INDICATED

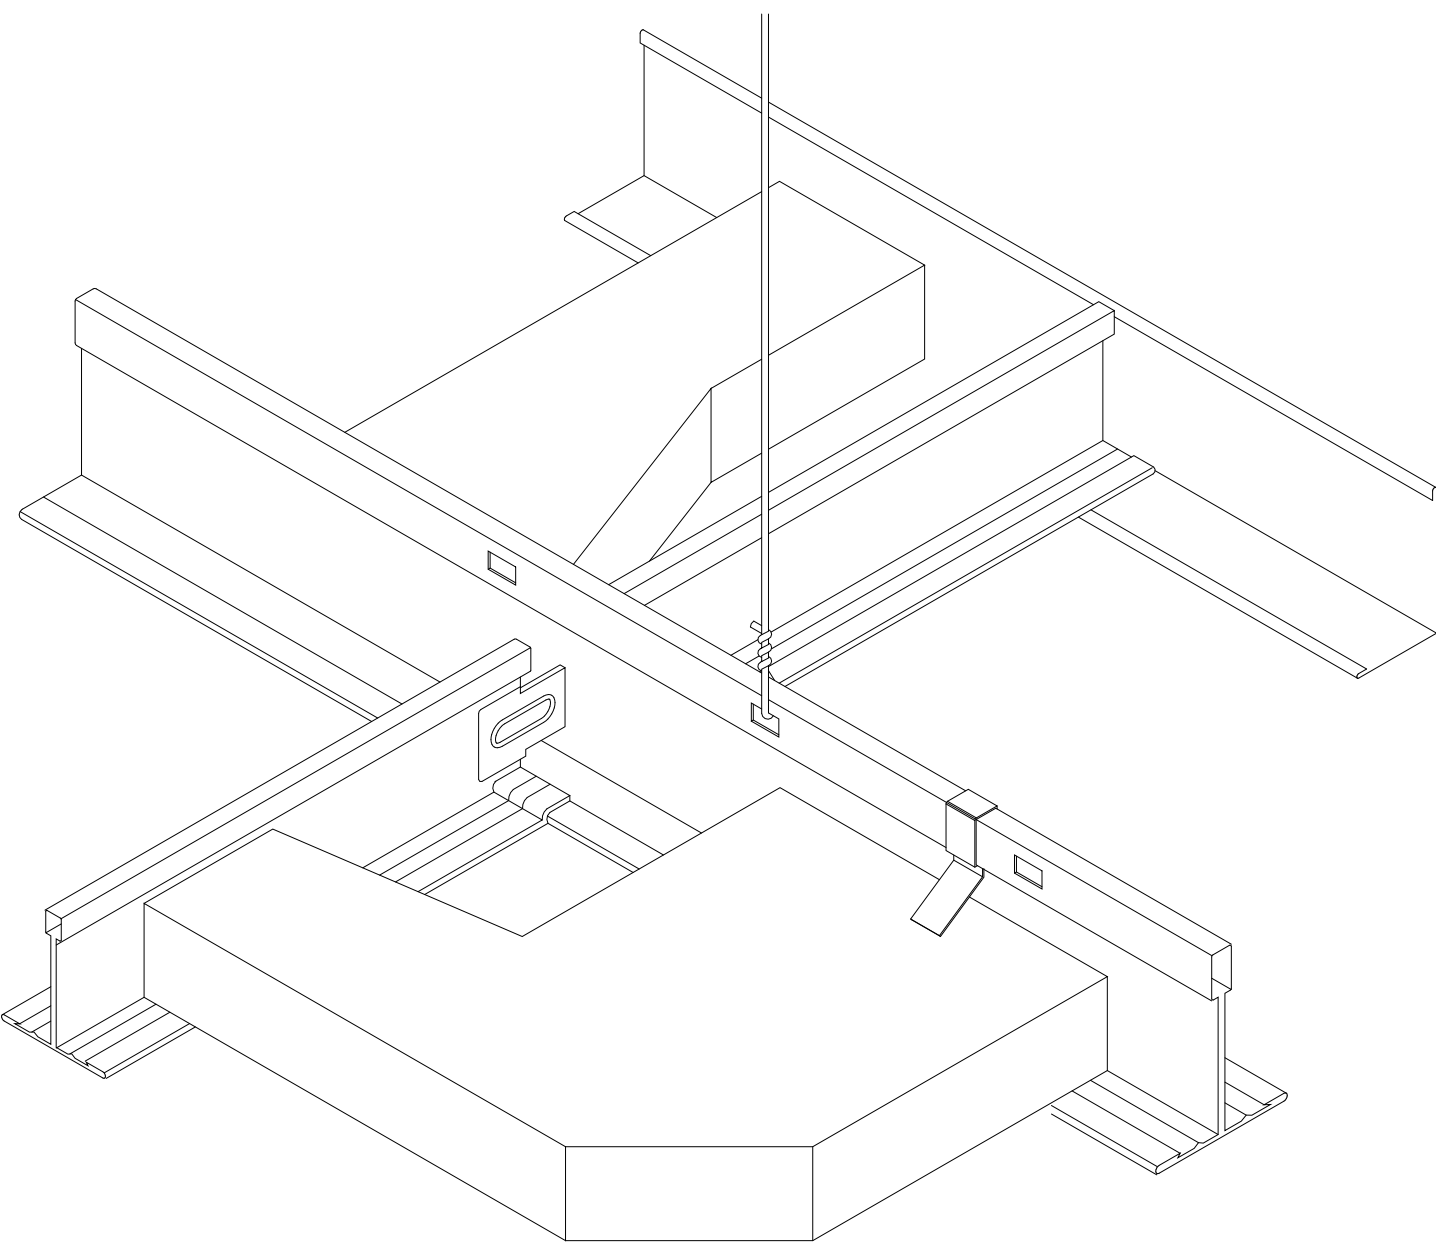

9 DETAIL OF EXPOSED T-BAR SYSTEM
1 : 100

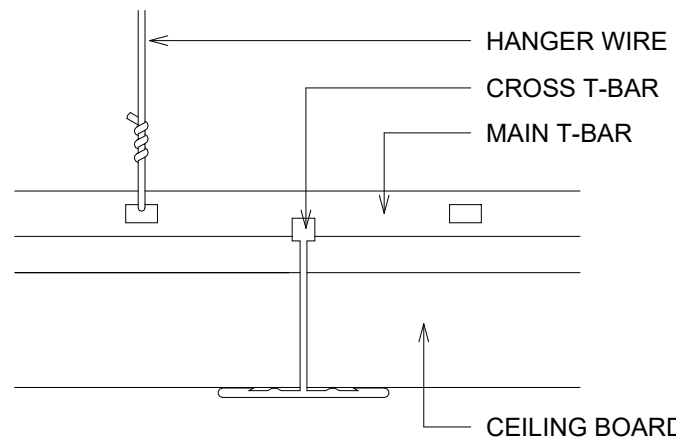

10 SECTION PERPENDICULAR TO CROSS T-BAR
1 : 100

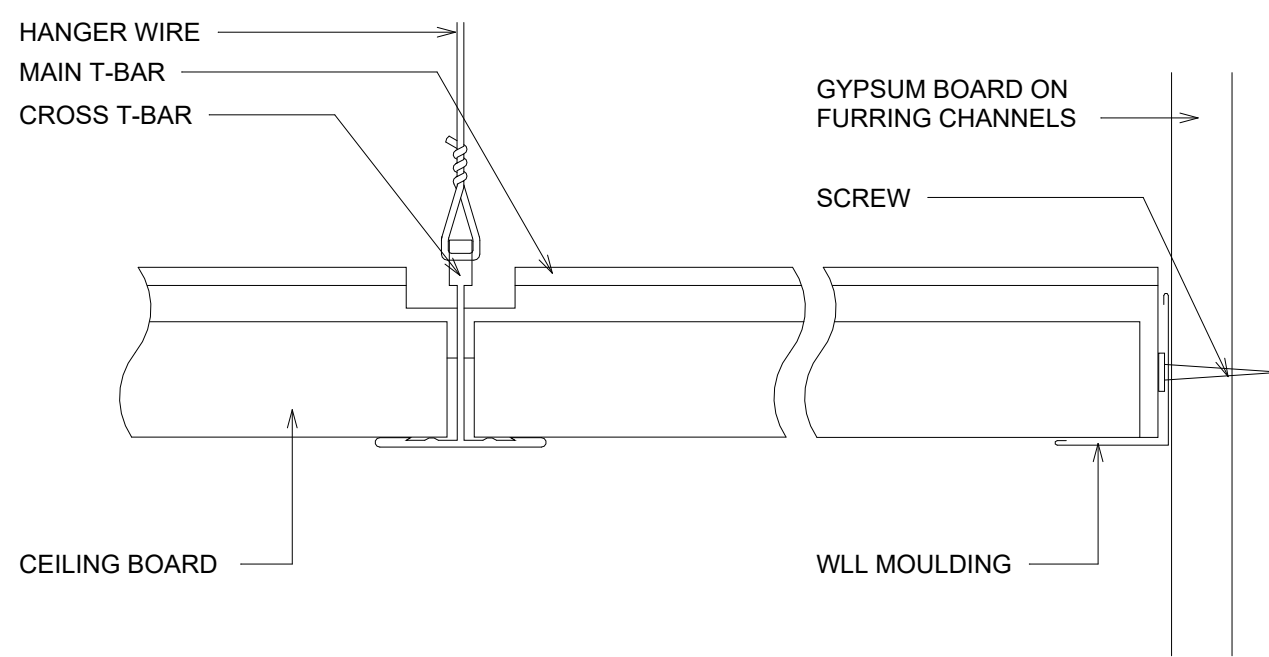

11 SECTION PERPENDICULAR TO MAIN T-BAR
1 : 100

