




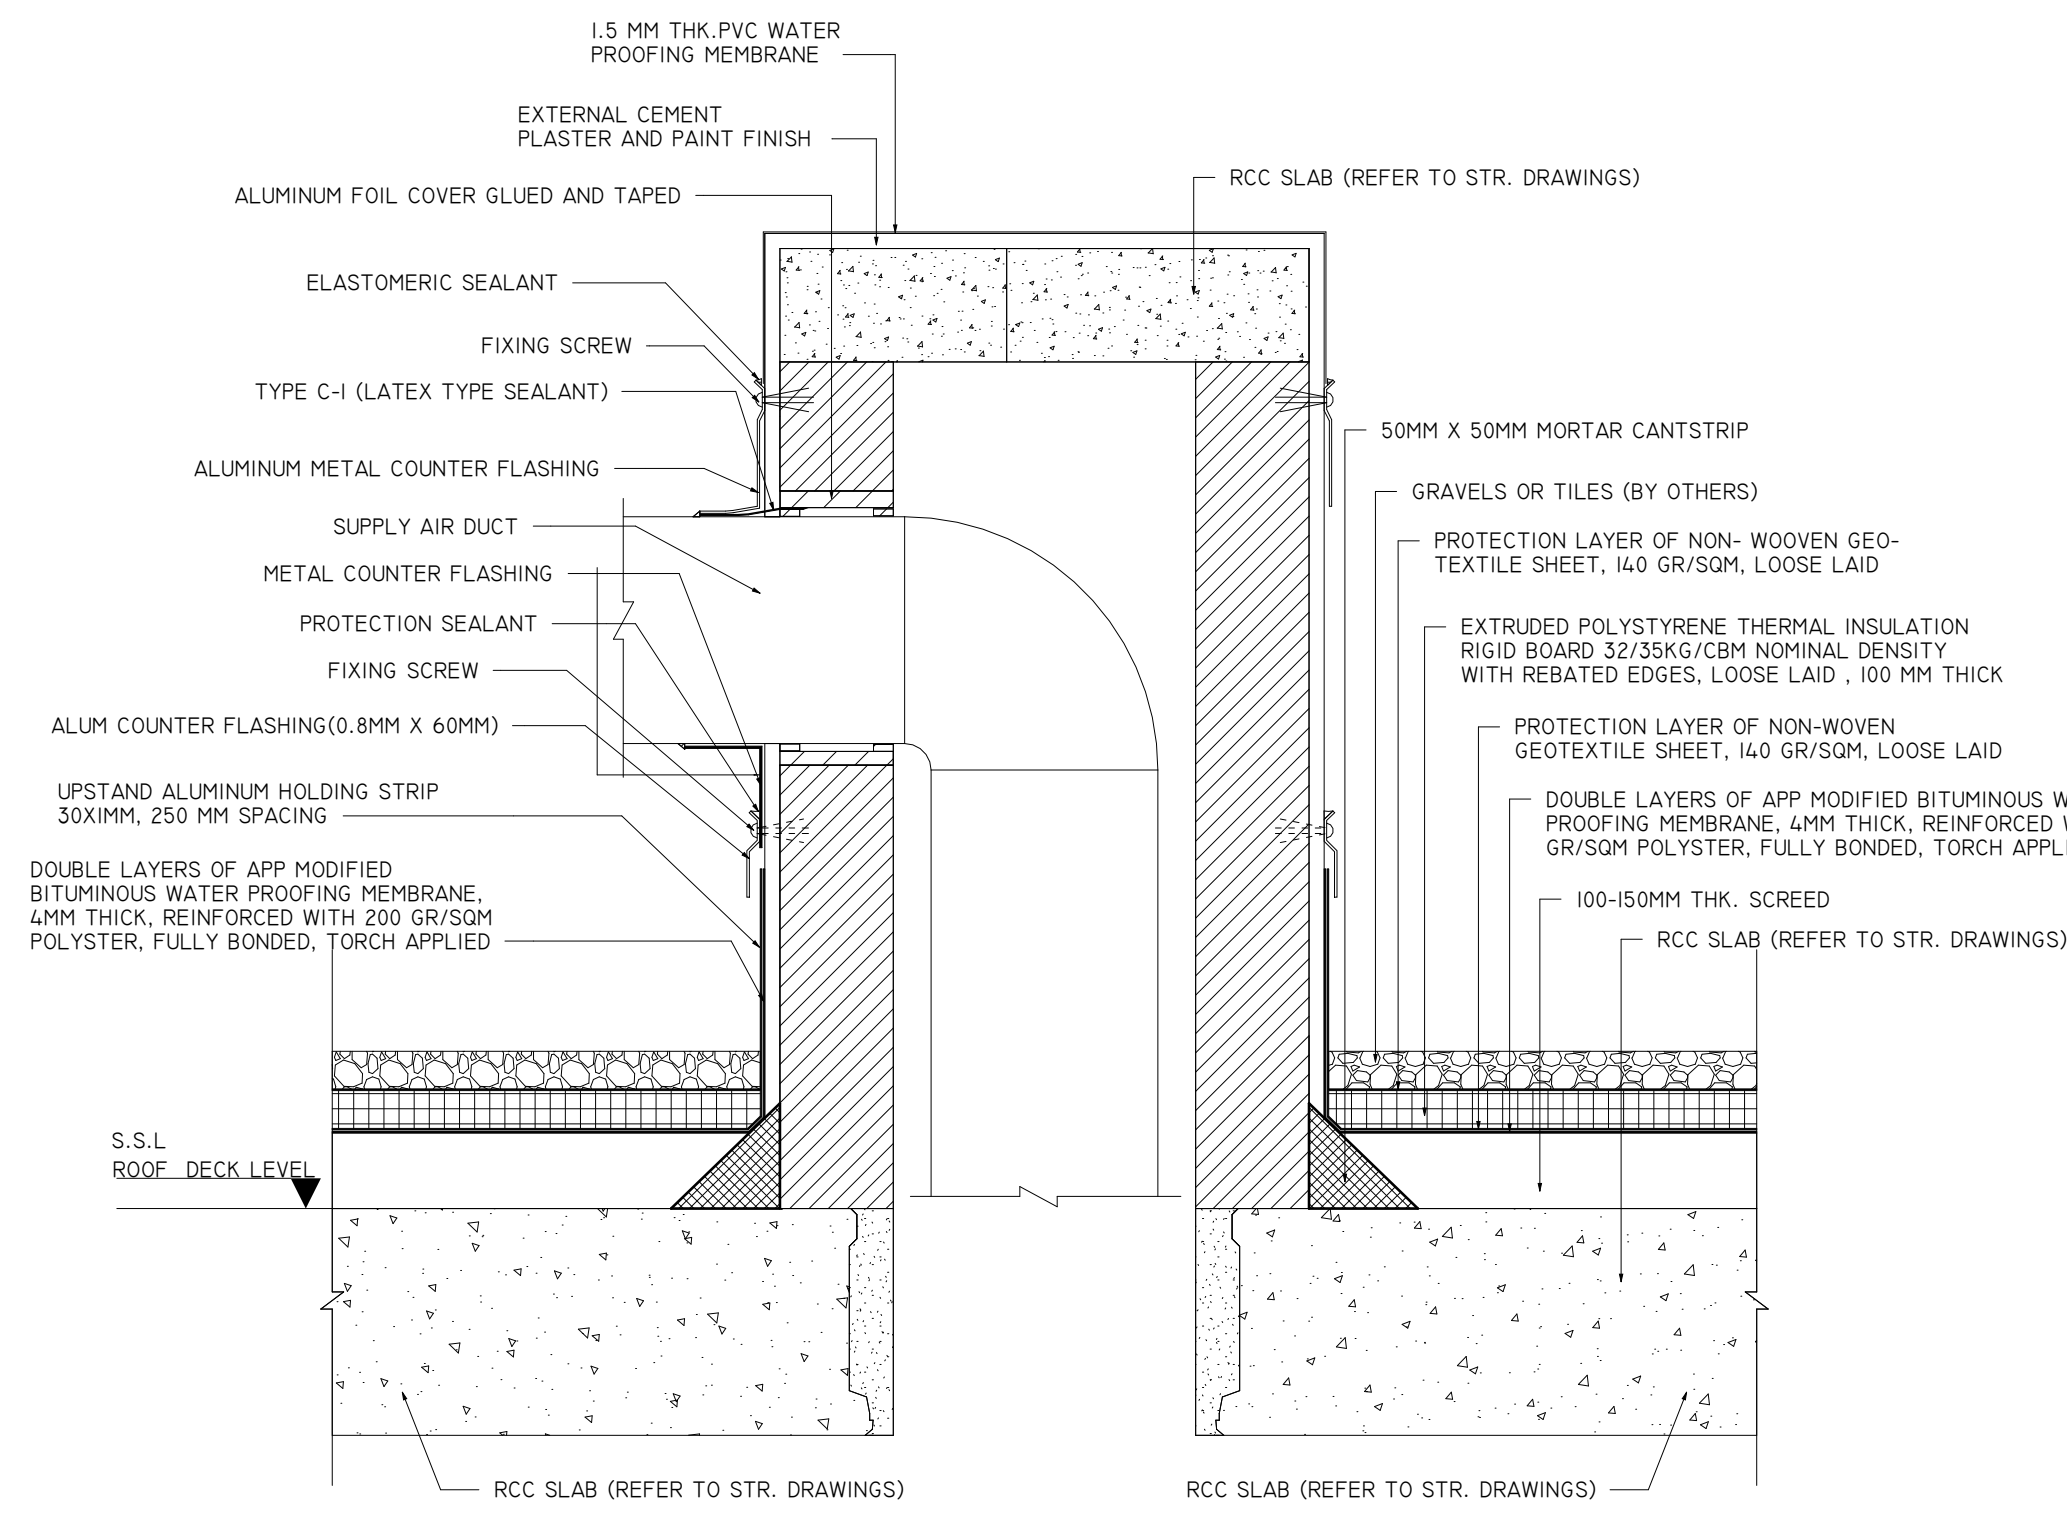


1 TYPICAL AIR DUCT - THROUGH ROOF
1 : 10

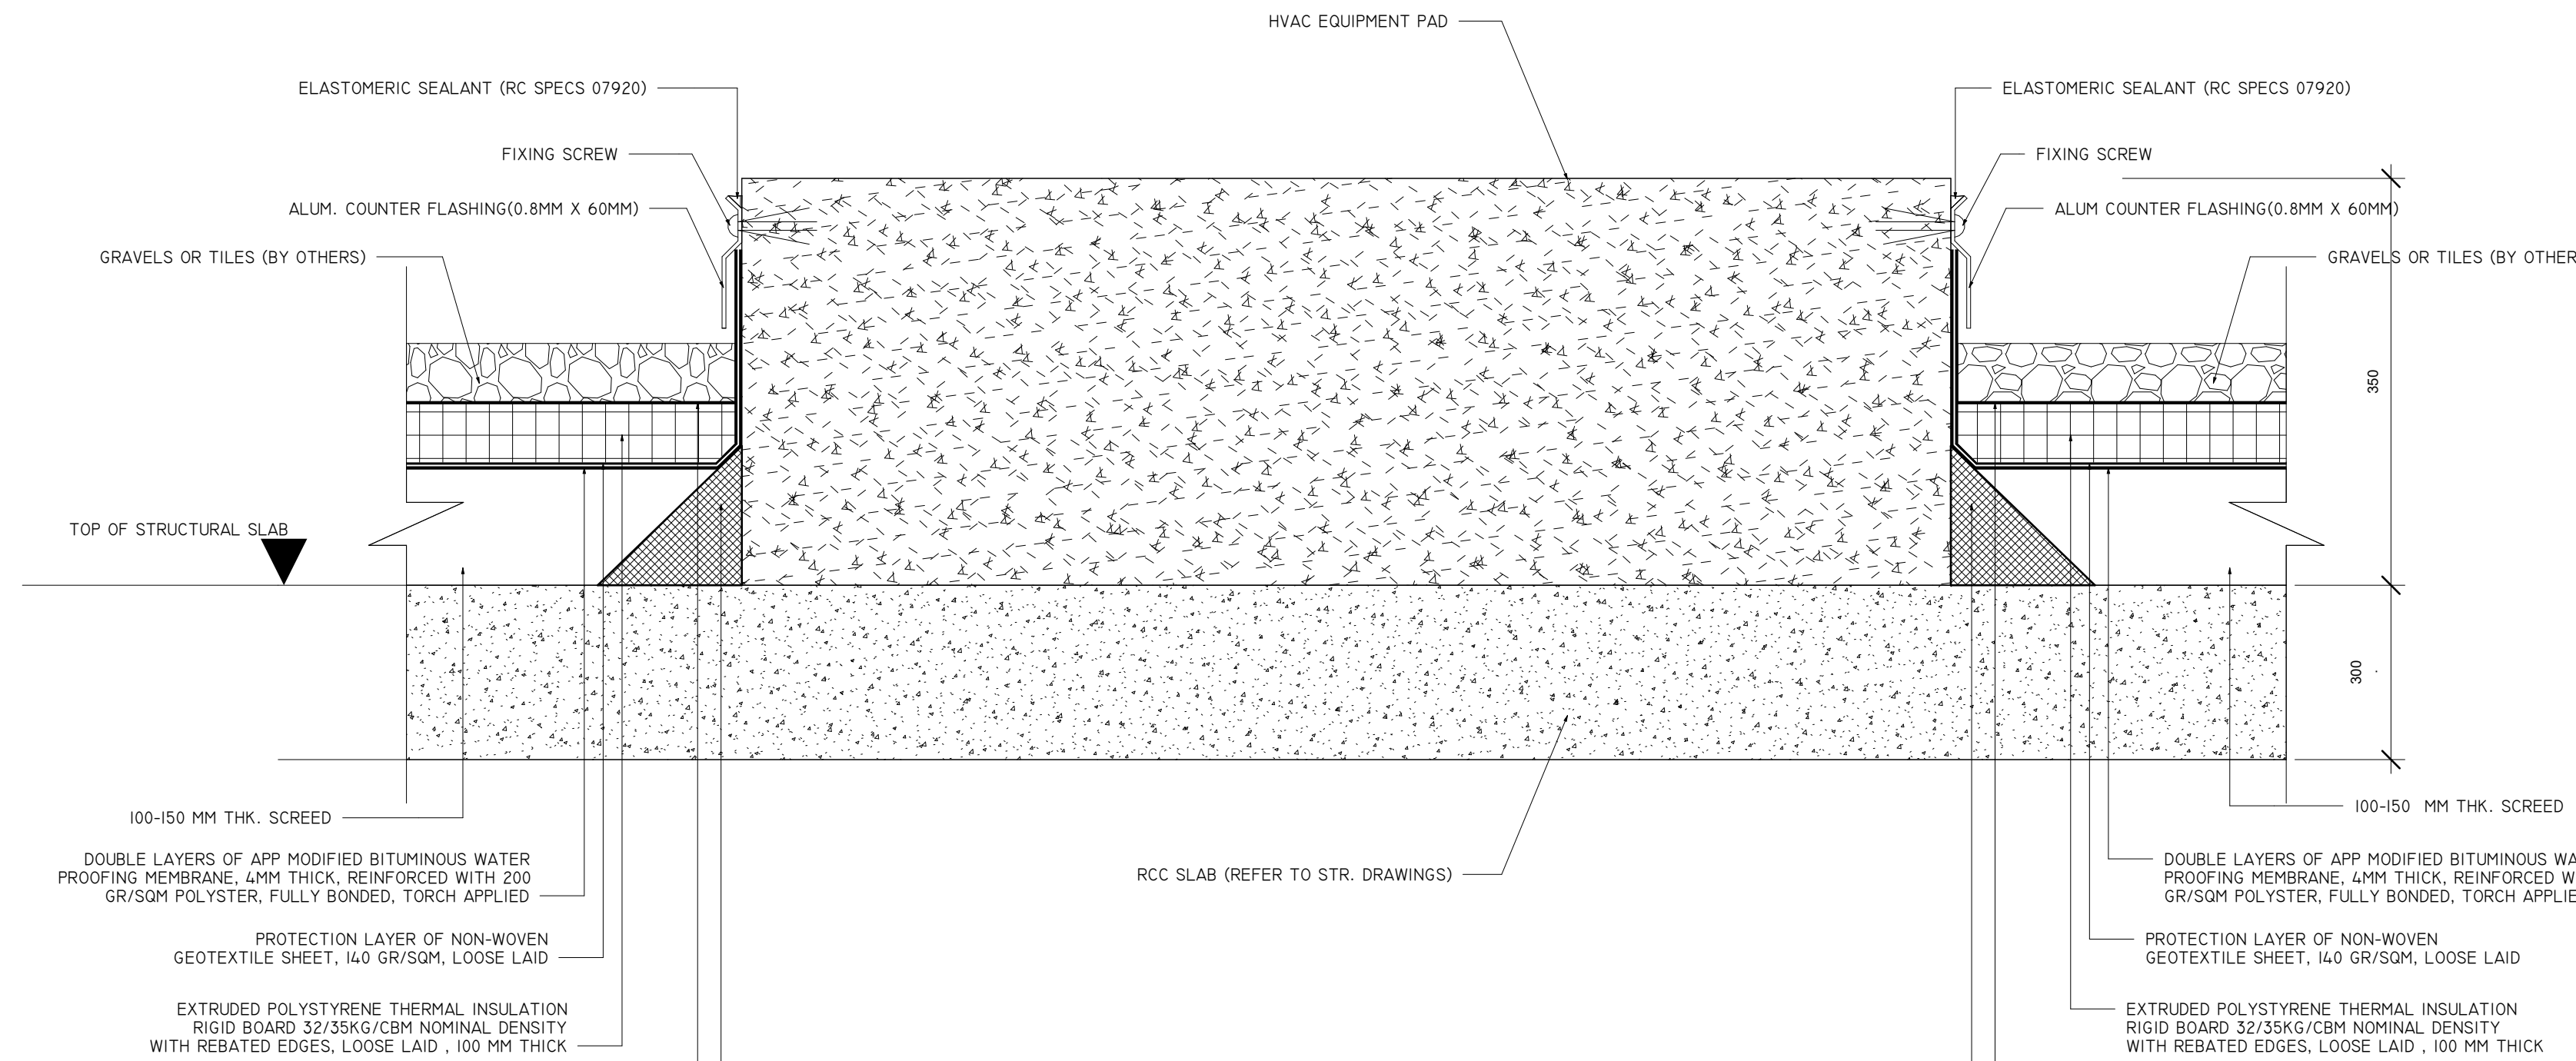


2 TYPICAL HVAC QEQUIPMENT PAD DETAIL
1 : 5

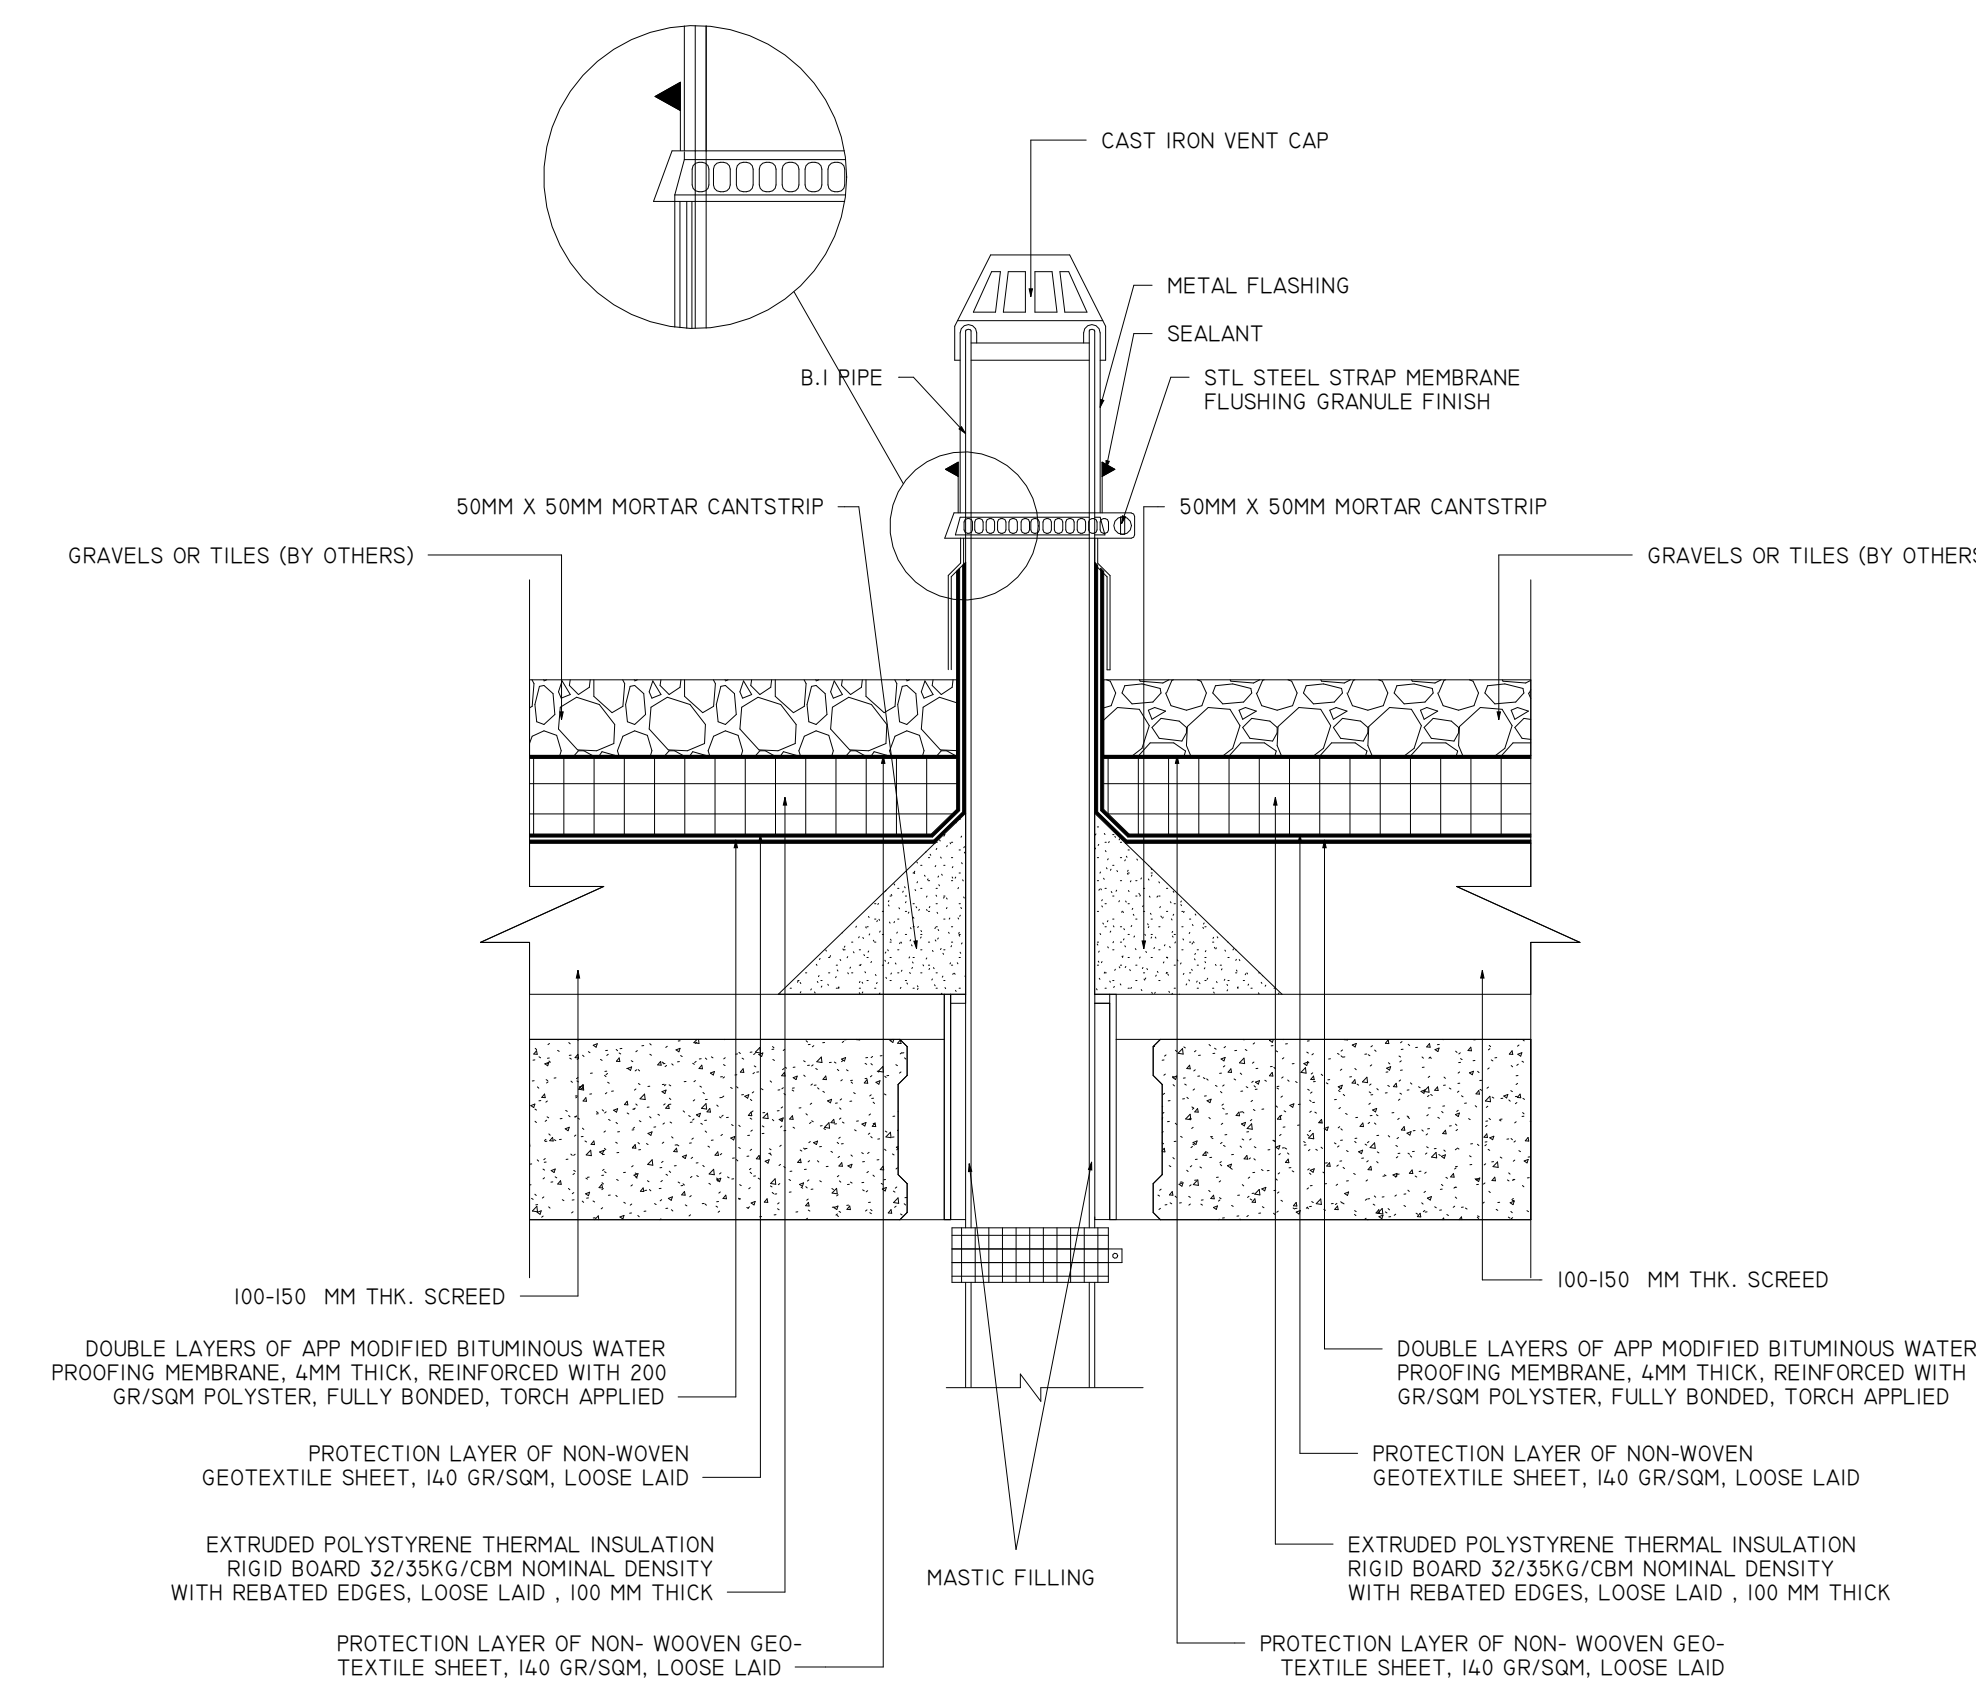


3 TYPICAL VENT THROUGH ROOF DETAIL
1 : 5

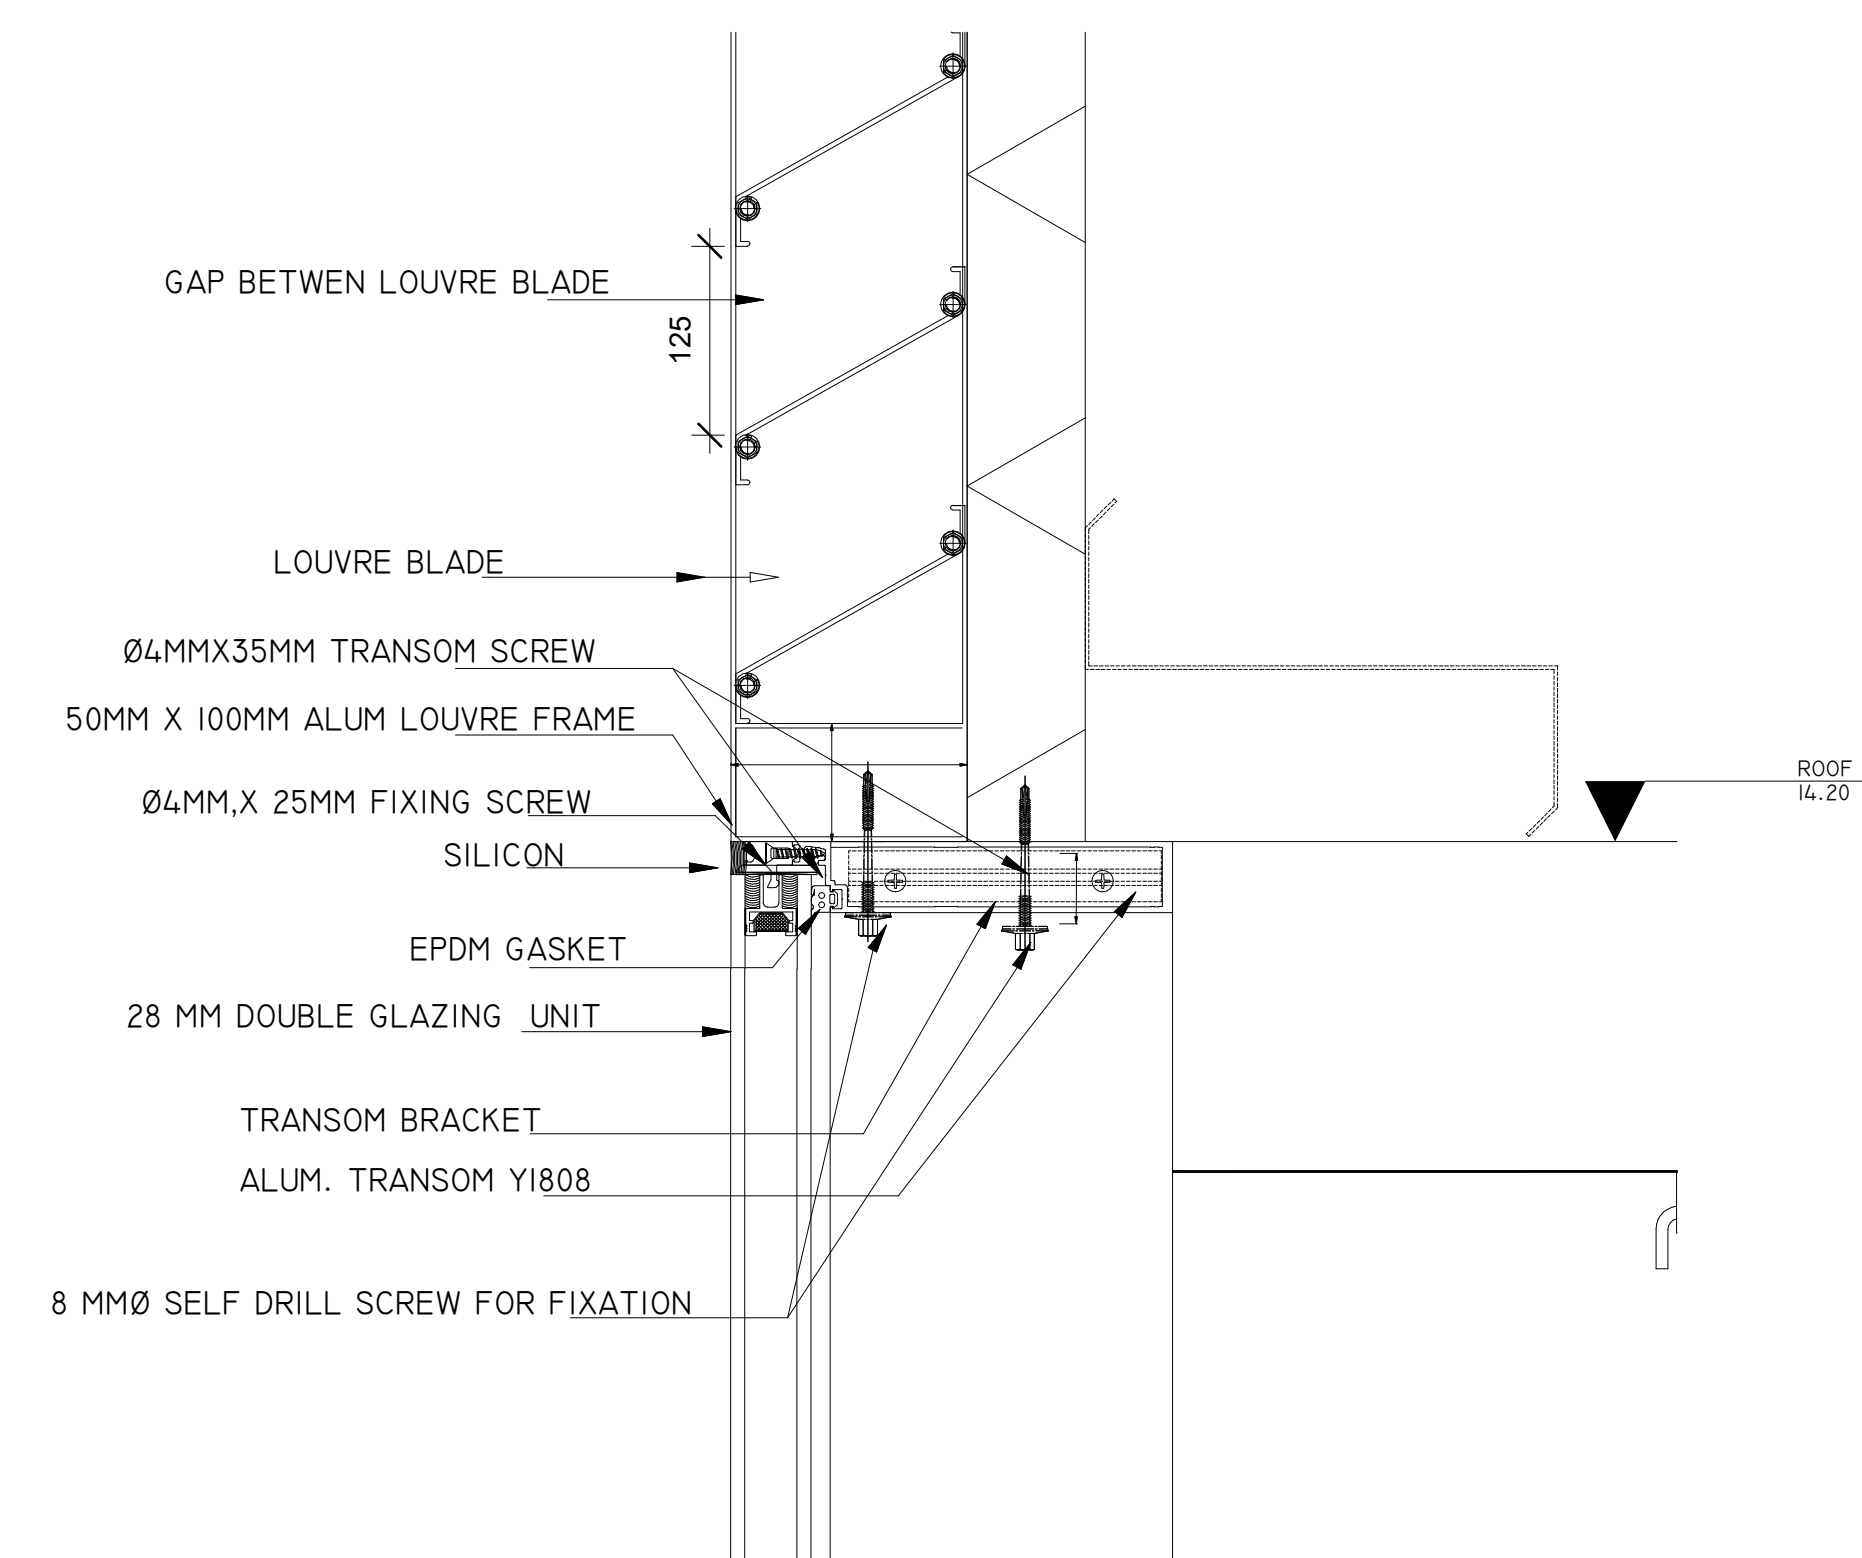


4 LOUVER TO CURTAIN WALL DETAILS
1 : 5

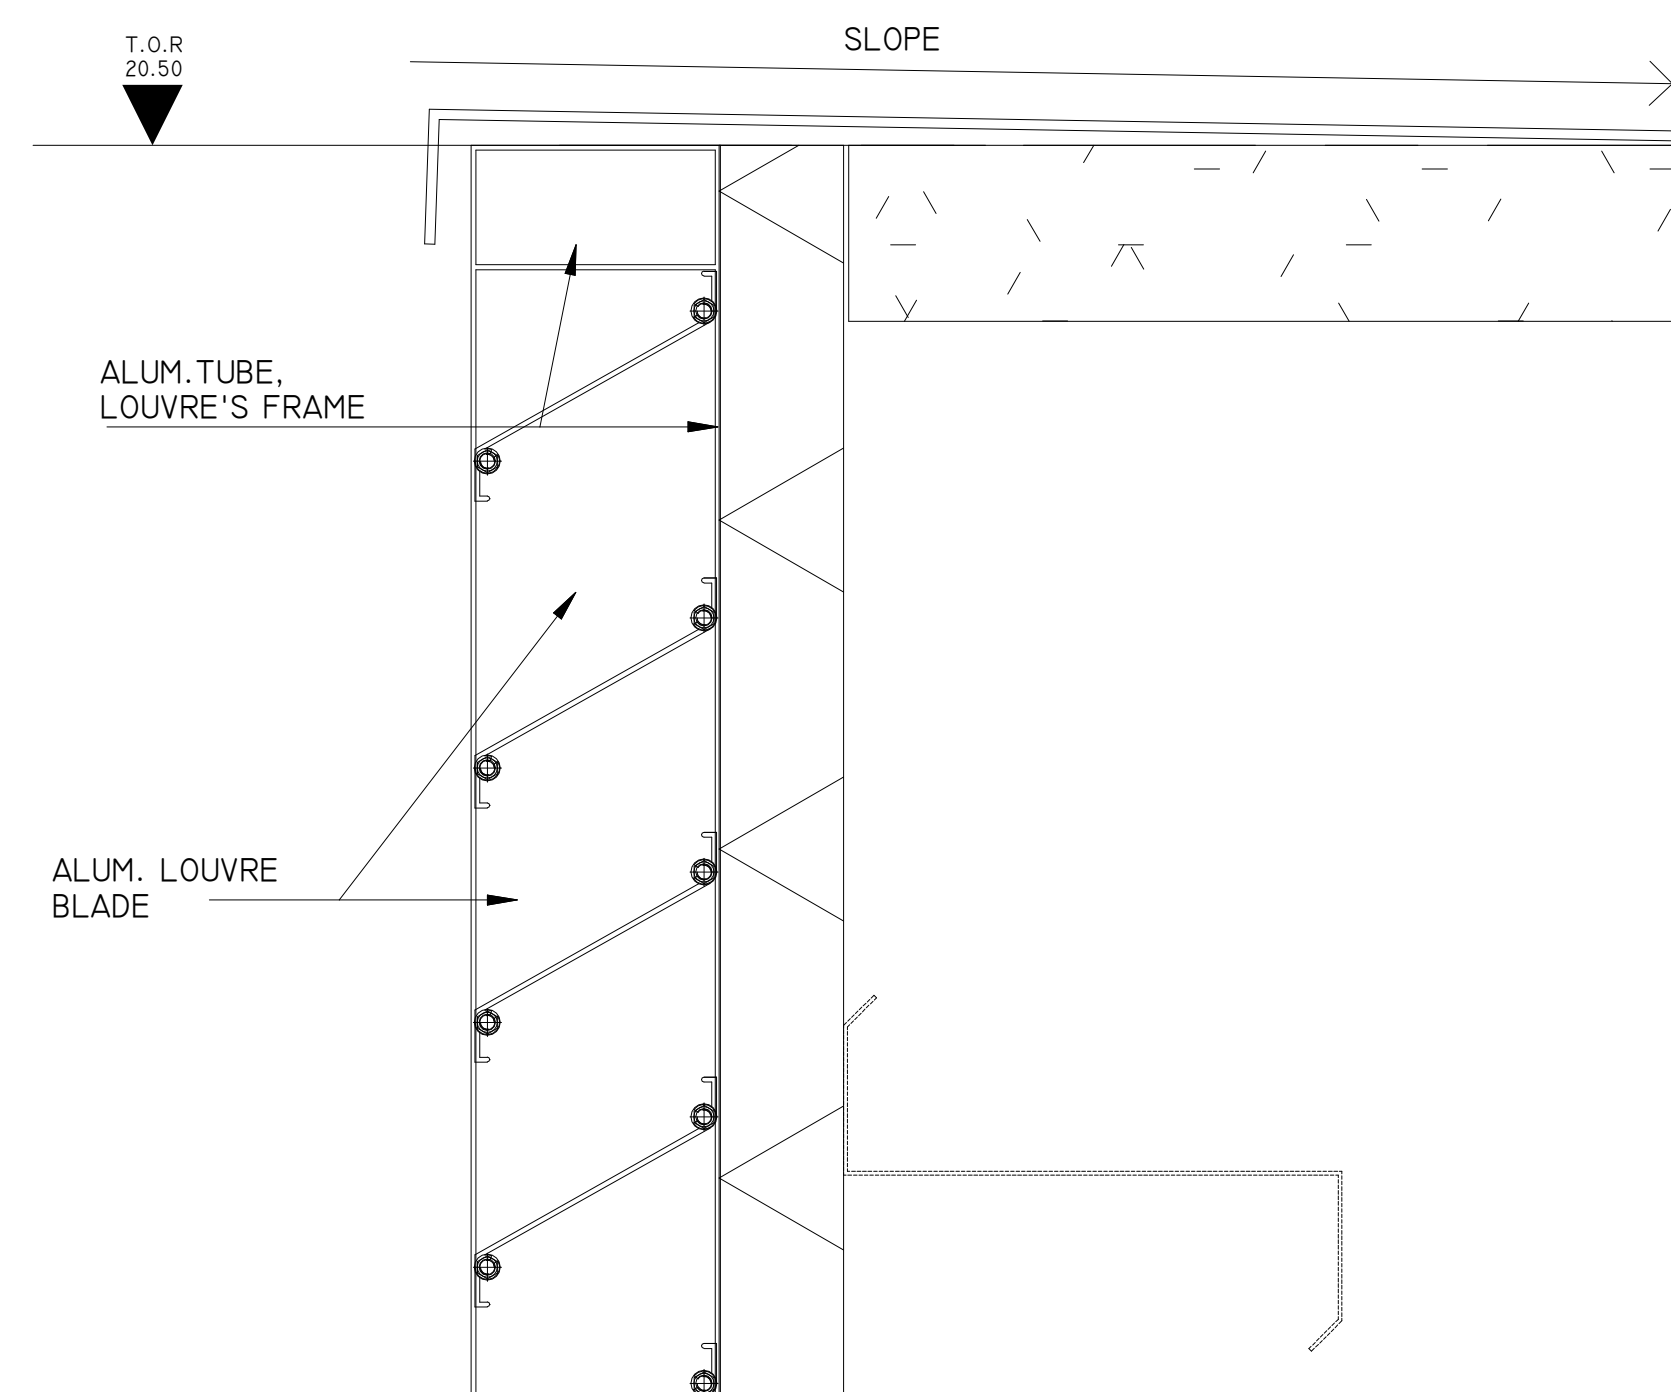


5 FLASHING DETAILS AT PARAPET
1 : 5

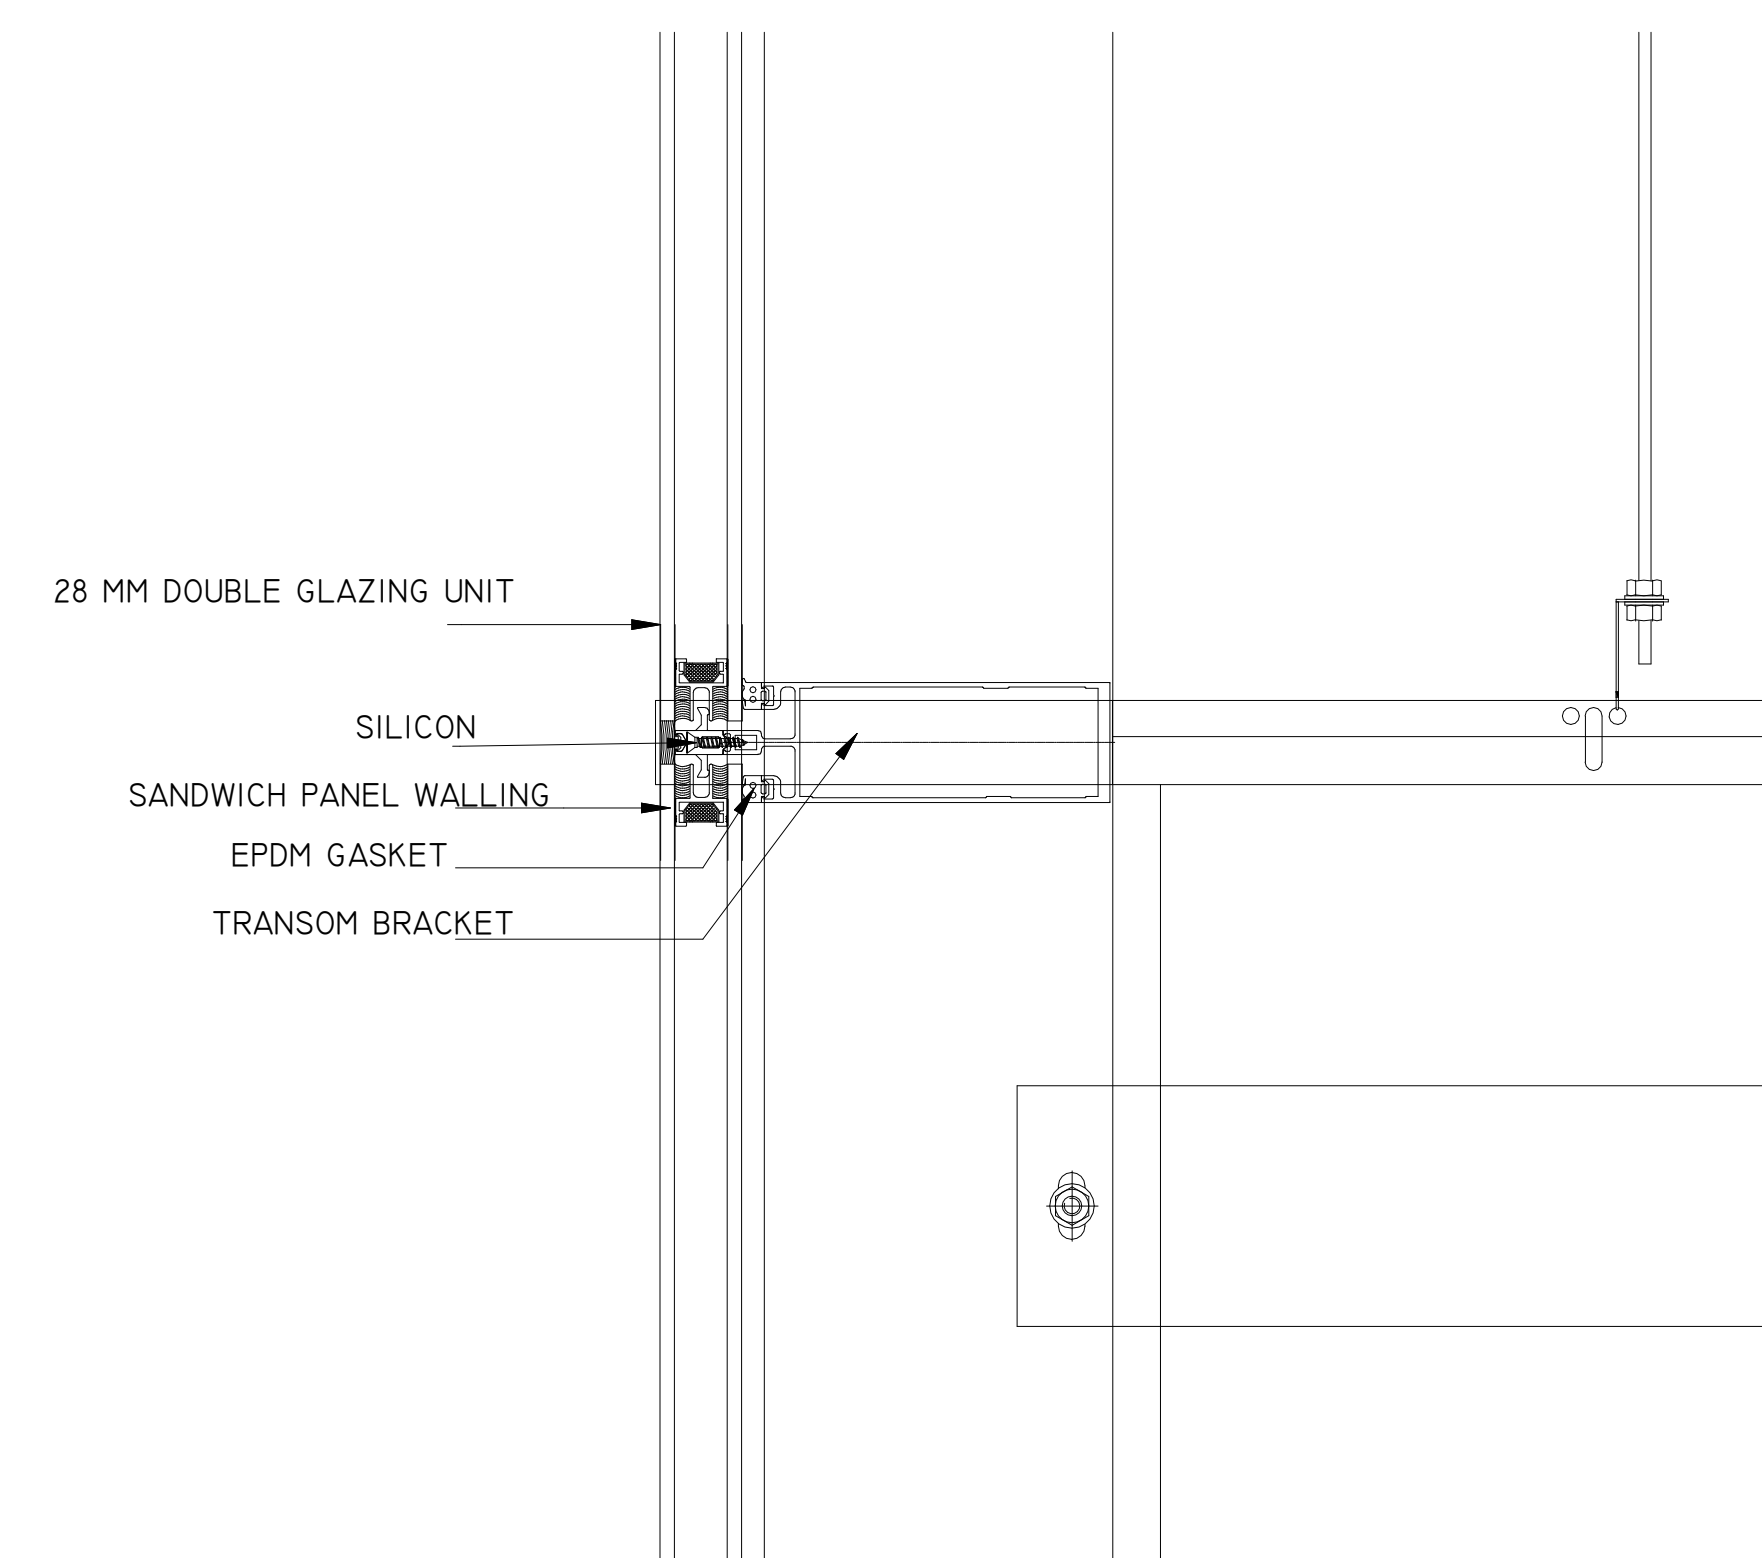


6 CURTAIN WALL CONNECTION
1 : 5

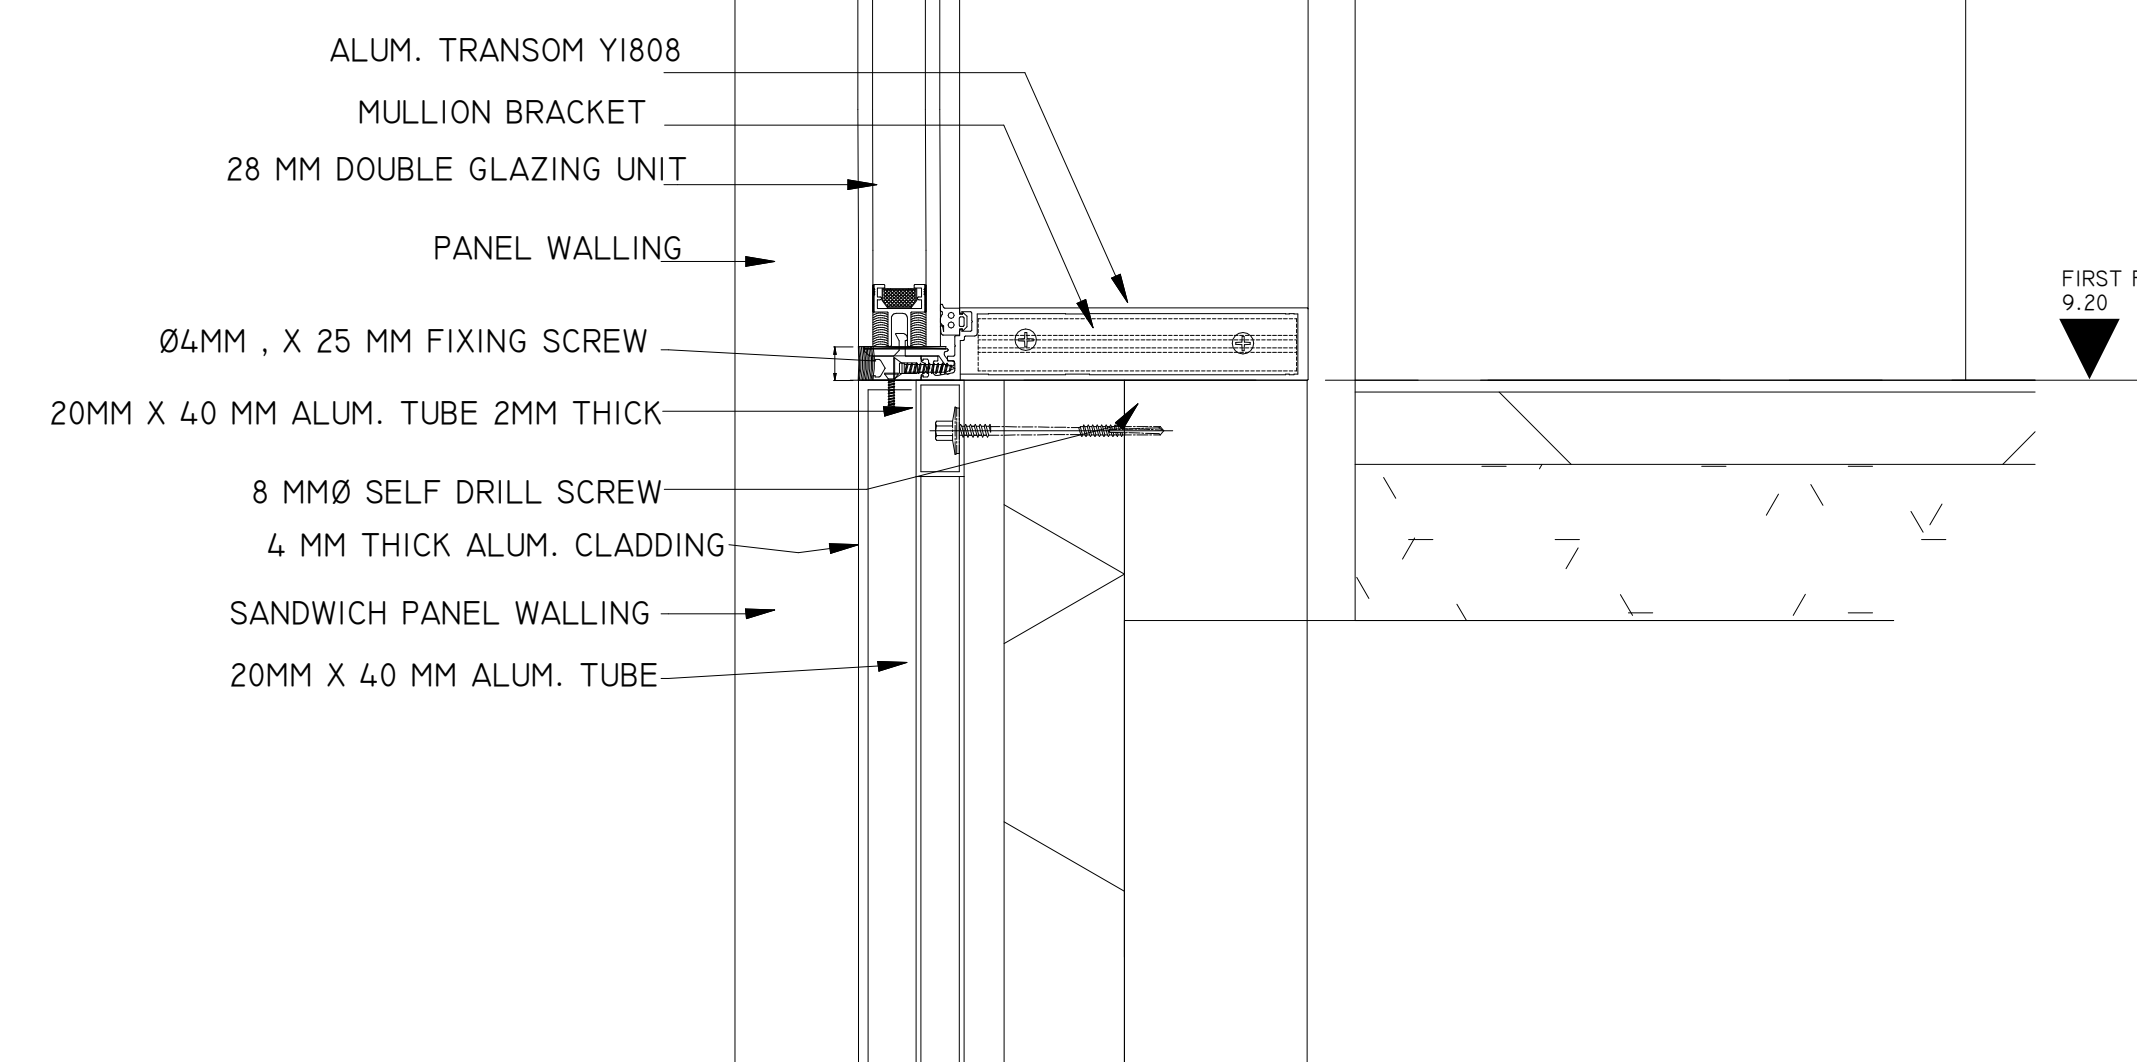


7 CURTAIN WALL CONNECTION ON SLAB DETAILS
1 : 5

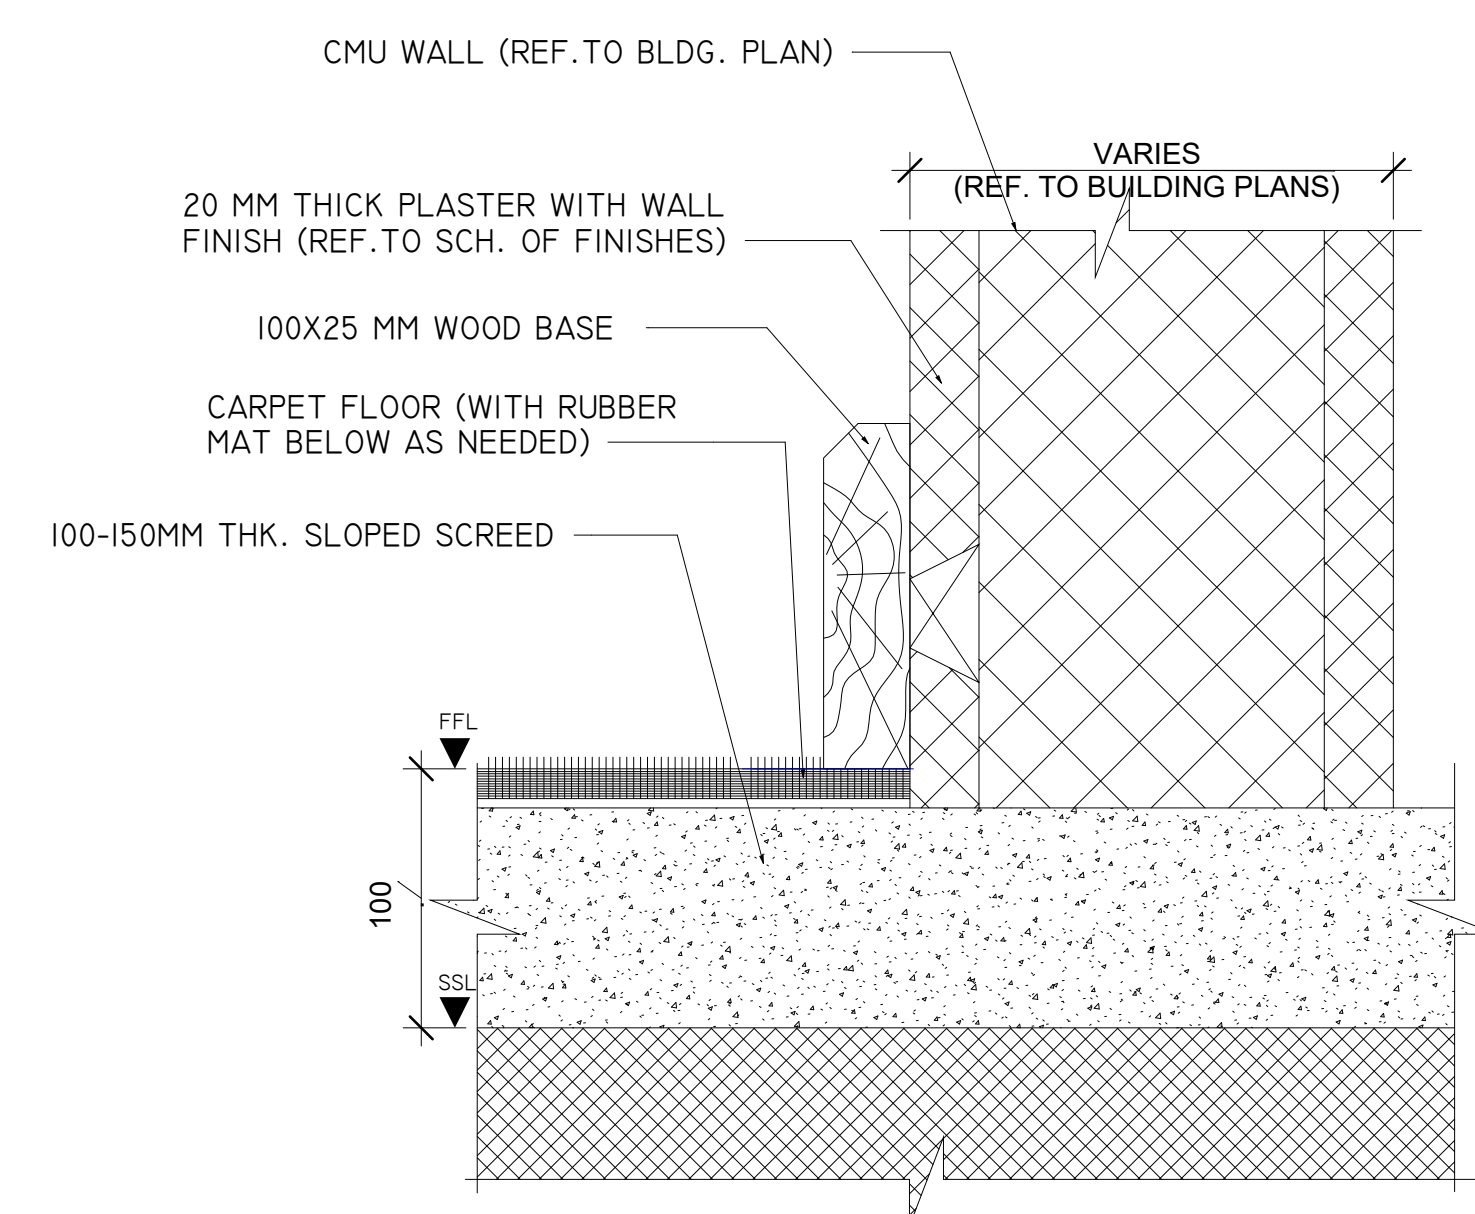

8 CARPET TO WOOD DETAIL
1 : 2

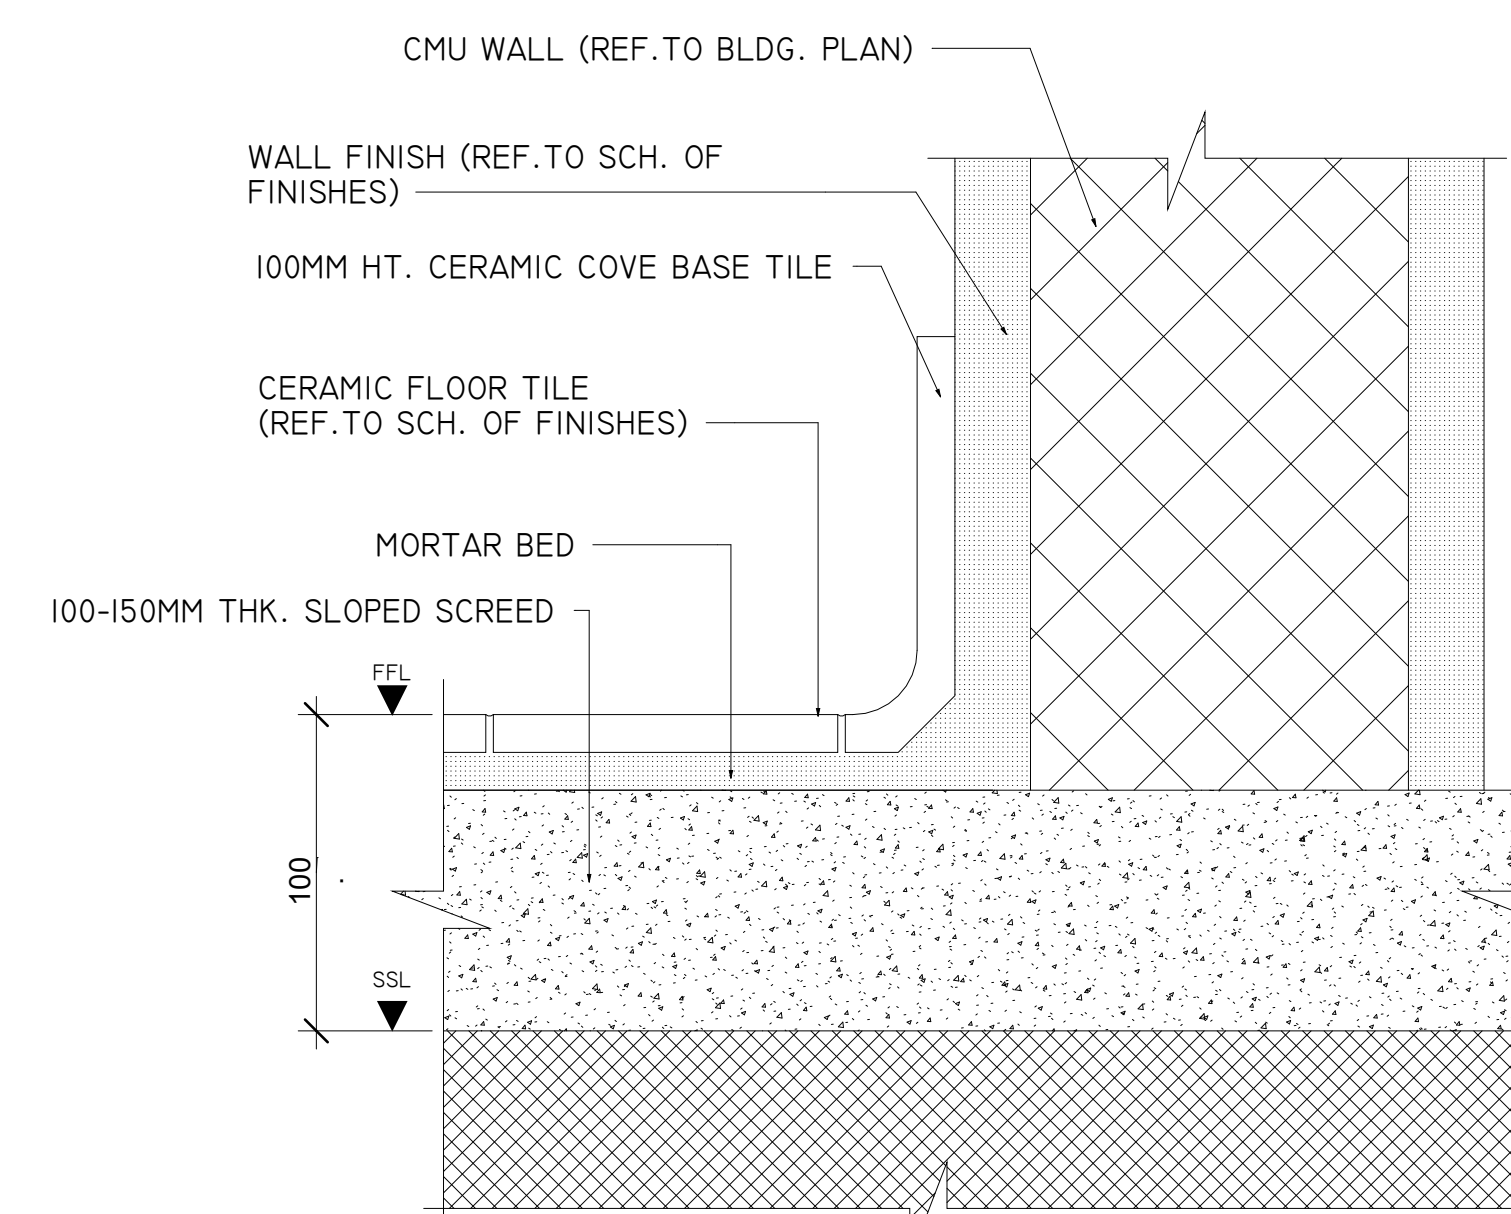


9 CERAMIC TO CERAMIC DETAIL
1 : 2

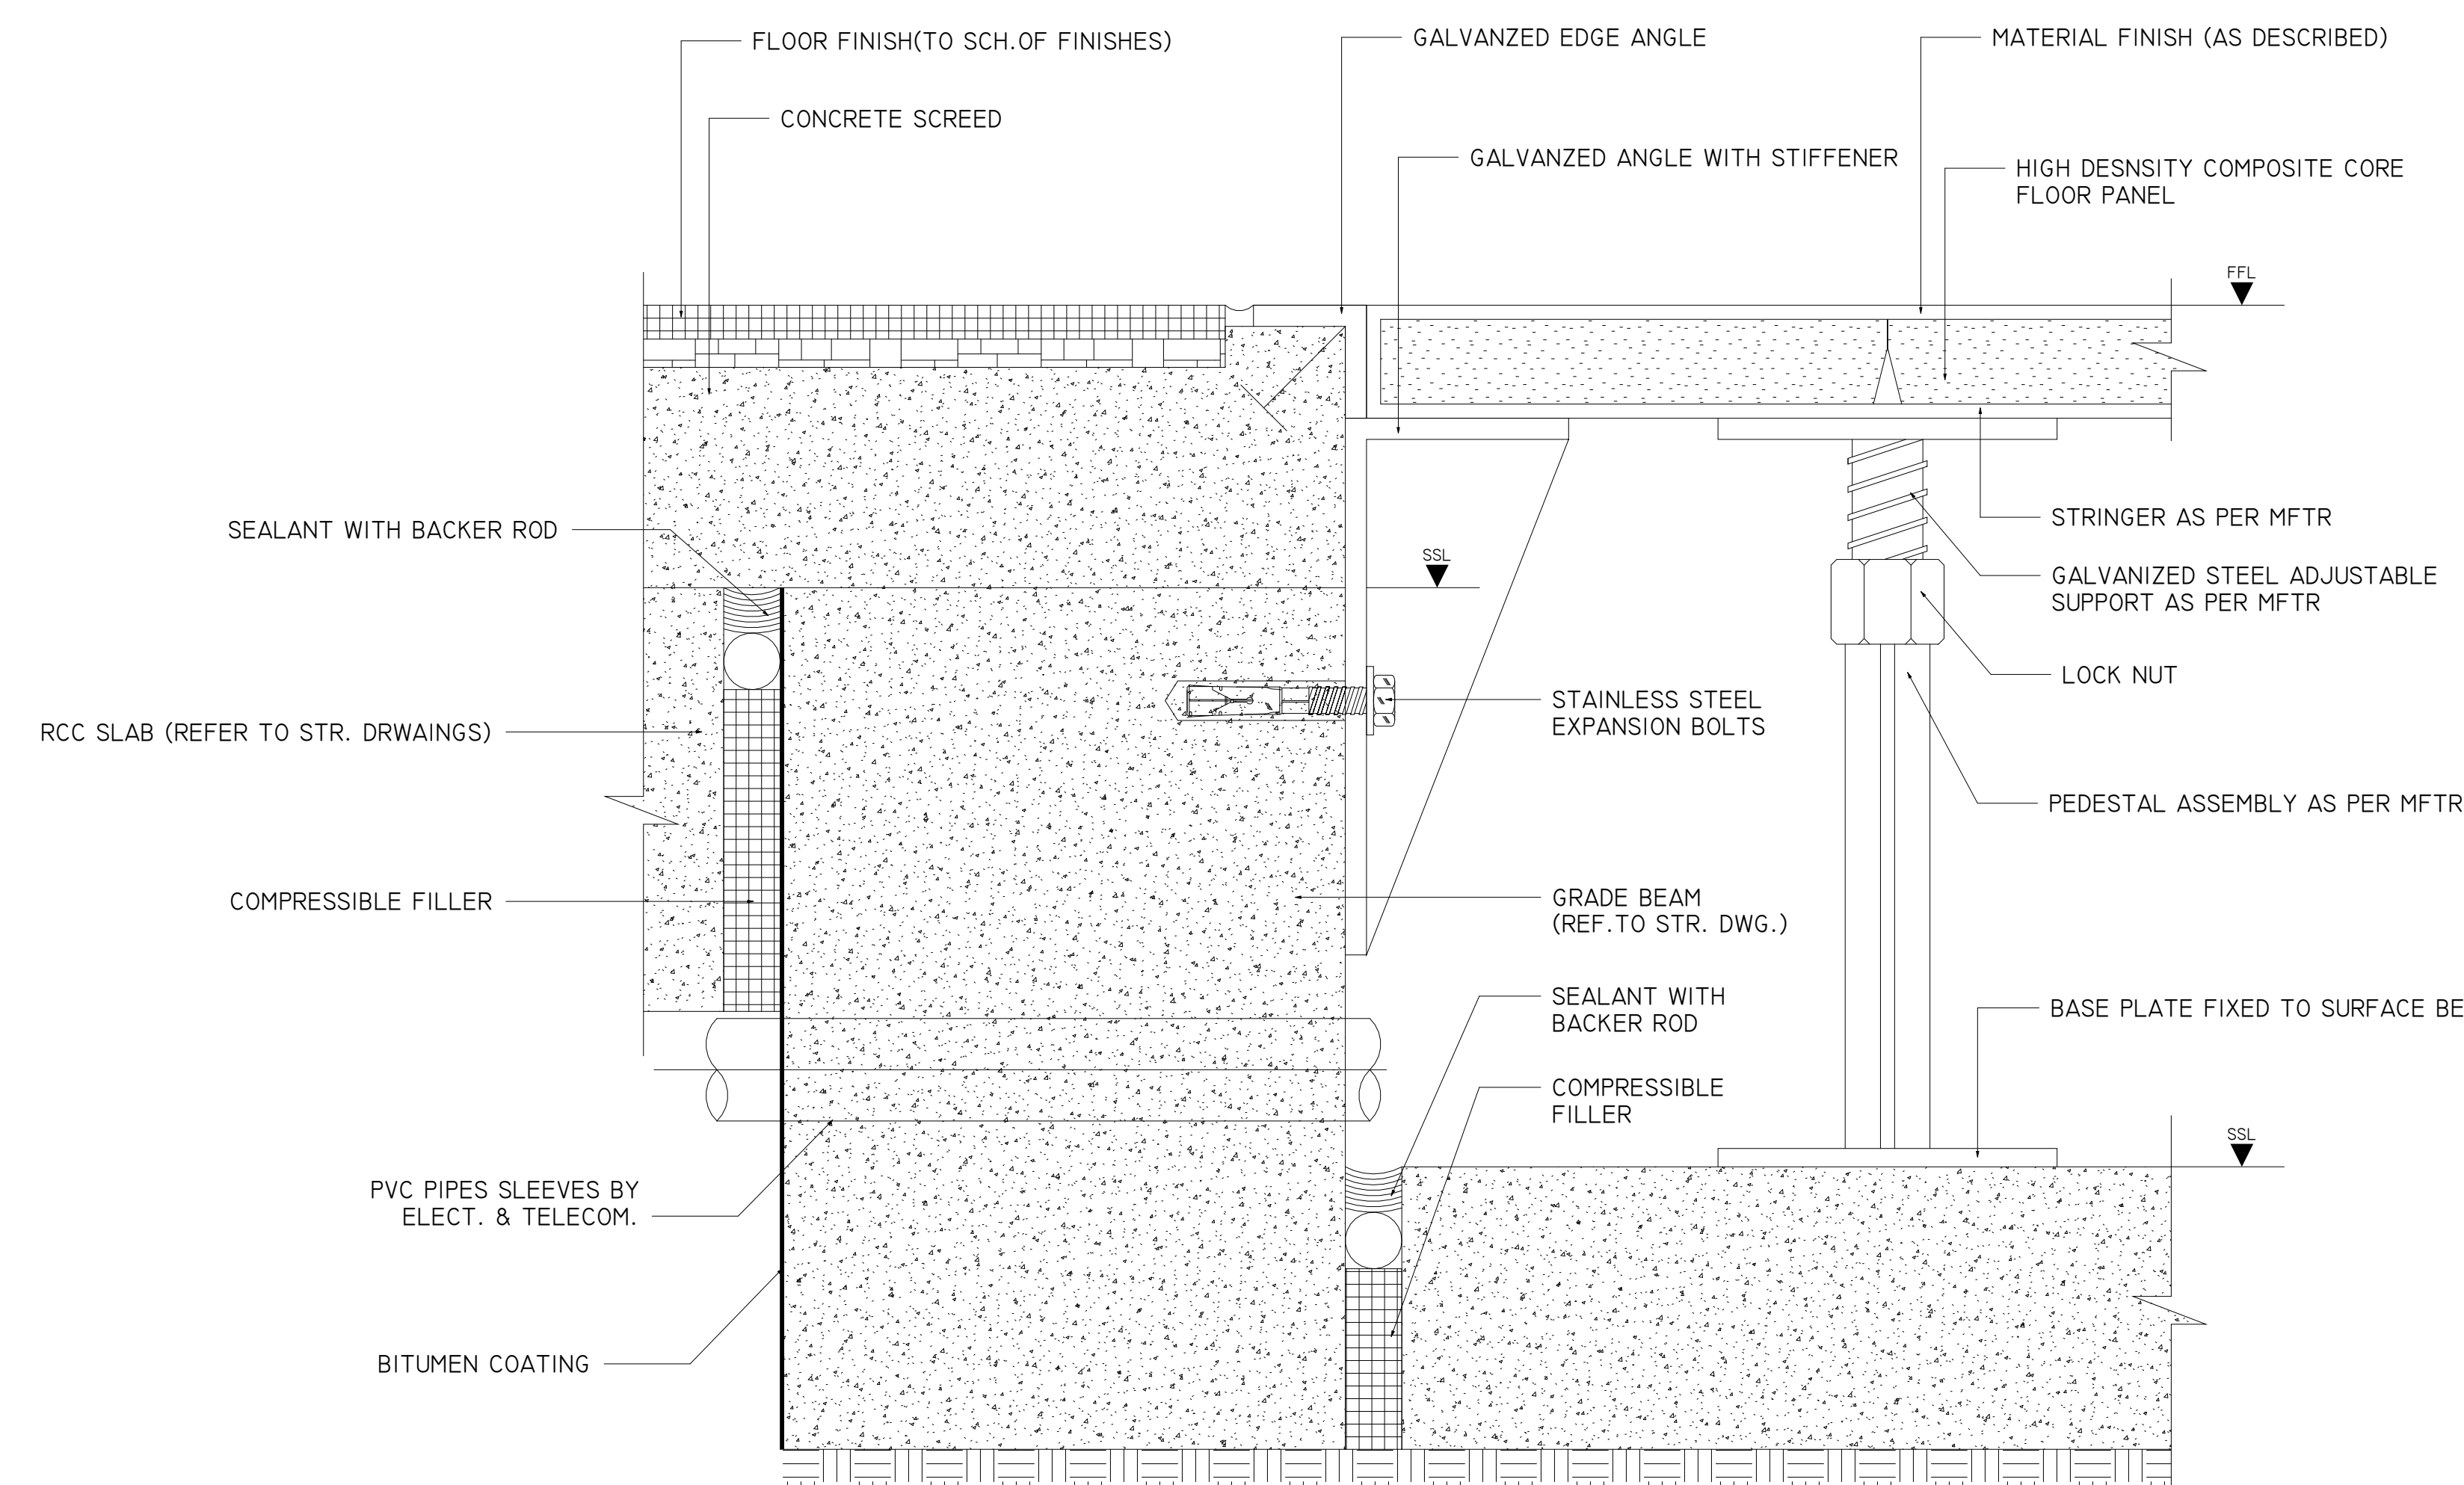

10 RAISED FLOOR DETAIL (INTERNAL)
1 : 2

KEY PLAN :

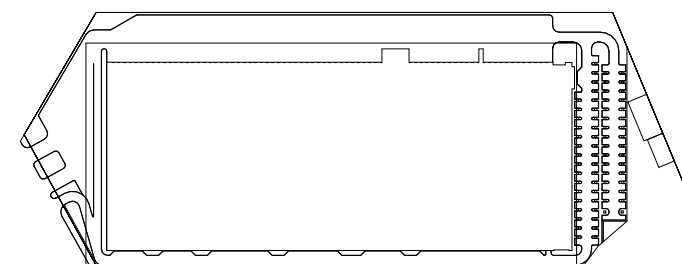

REV.	DATE	DESCRIPTION OF REVISION
00	11/12/2025	ISSUE FOR DETAILED DESIGN

SEAL & SIGNATURE:

DRAWN BY	CHECKED BY	DATE (DD.MM.YYYY)
IBR	ALN	22.05.2025

NUPCO WAREHOUSE
ASEER, KSA

CLIENT:



PROJECT MANAGER:



PROJECT PROGRAM MANAGER



شركة الرامسات للمقاولات
Al Ramsat contracting company

ARCHITECTURE & ENGINEERING CONSULTANT:



PHASE & DISCIPLINE:

DETAIL DESIGN
ARCHITECTURE

DRAWING TITLE:

MISCELLANEOUS DETAILS
4/4

PROJECT NO.	DRAWING NUMBER	REV
102	RCC-NPC-ASR-ARC-DD-00703	00

