




THIS DRAWING AND THE DESIGN IT COVERS ARE THE PROPERTY OF GULF CONSULT. ARCHITECTS AND ENGINEERS THE USER SHALL NOT REPRODUCE, COPY, SHARE, ENHANCE, NOR USE EXCEPT IN A LIMITED WAY AND PRIVATE USE PERMITTED BY WRITTEN CONSENT GIVEN BY THE CONSULTANT.

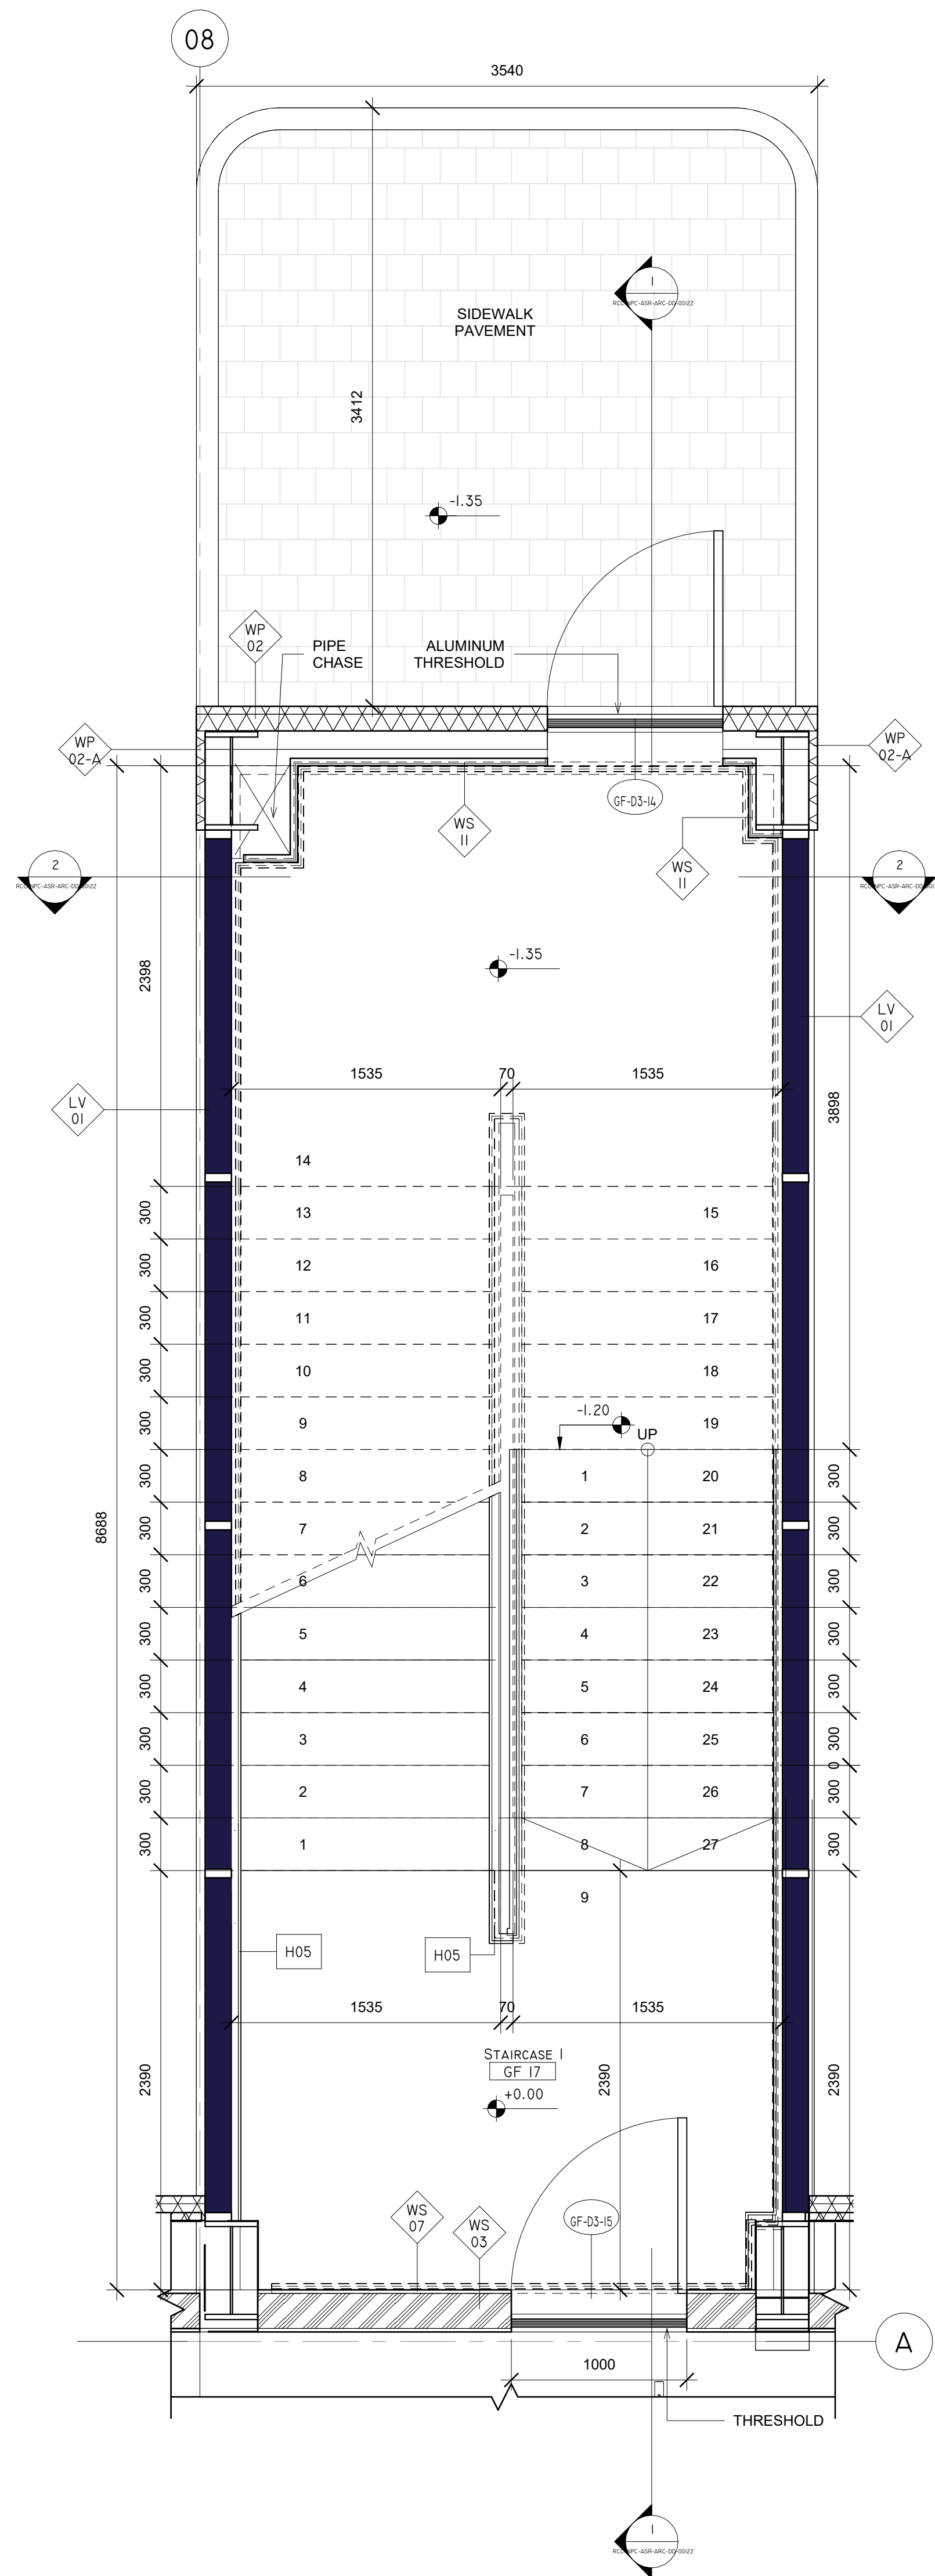


01 GROUND FLOOR PLAN (STAIRCASE -I)
1 : 25

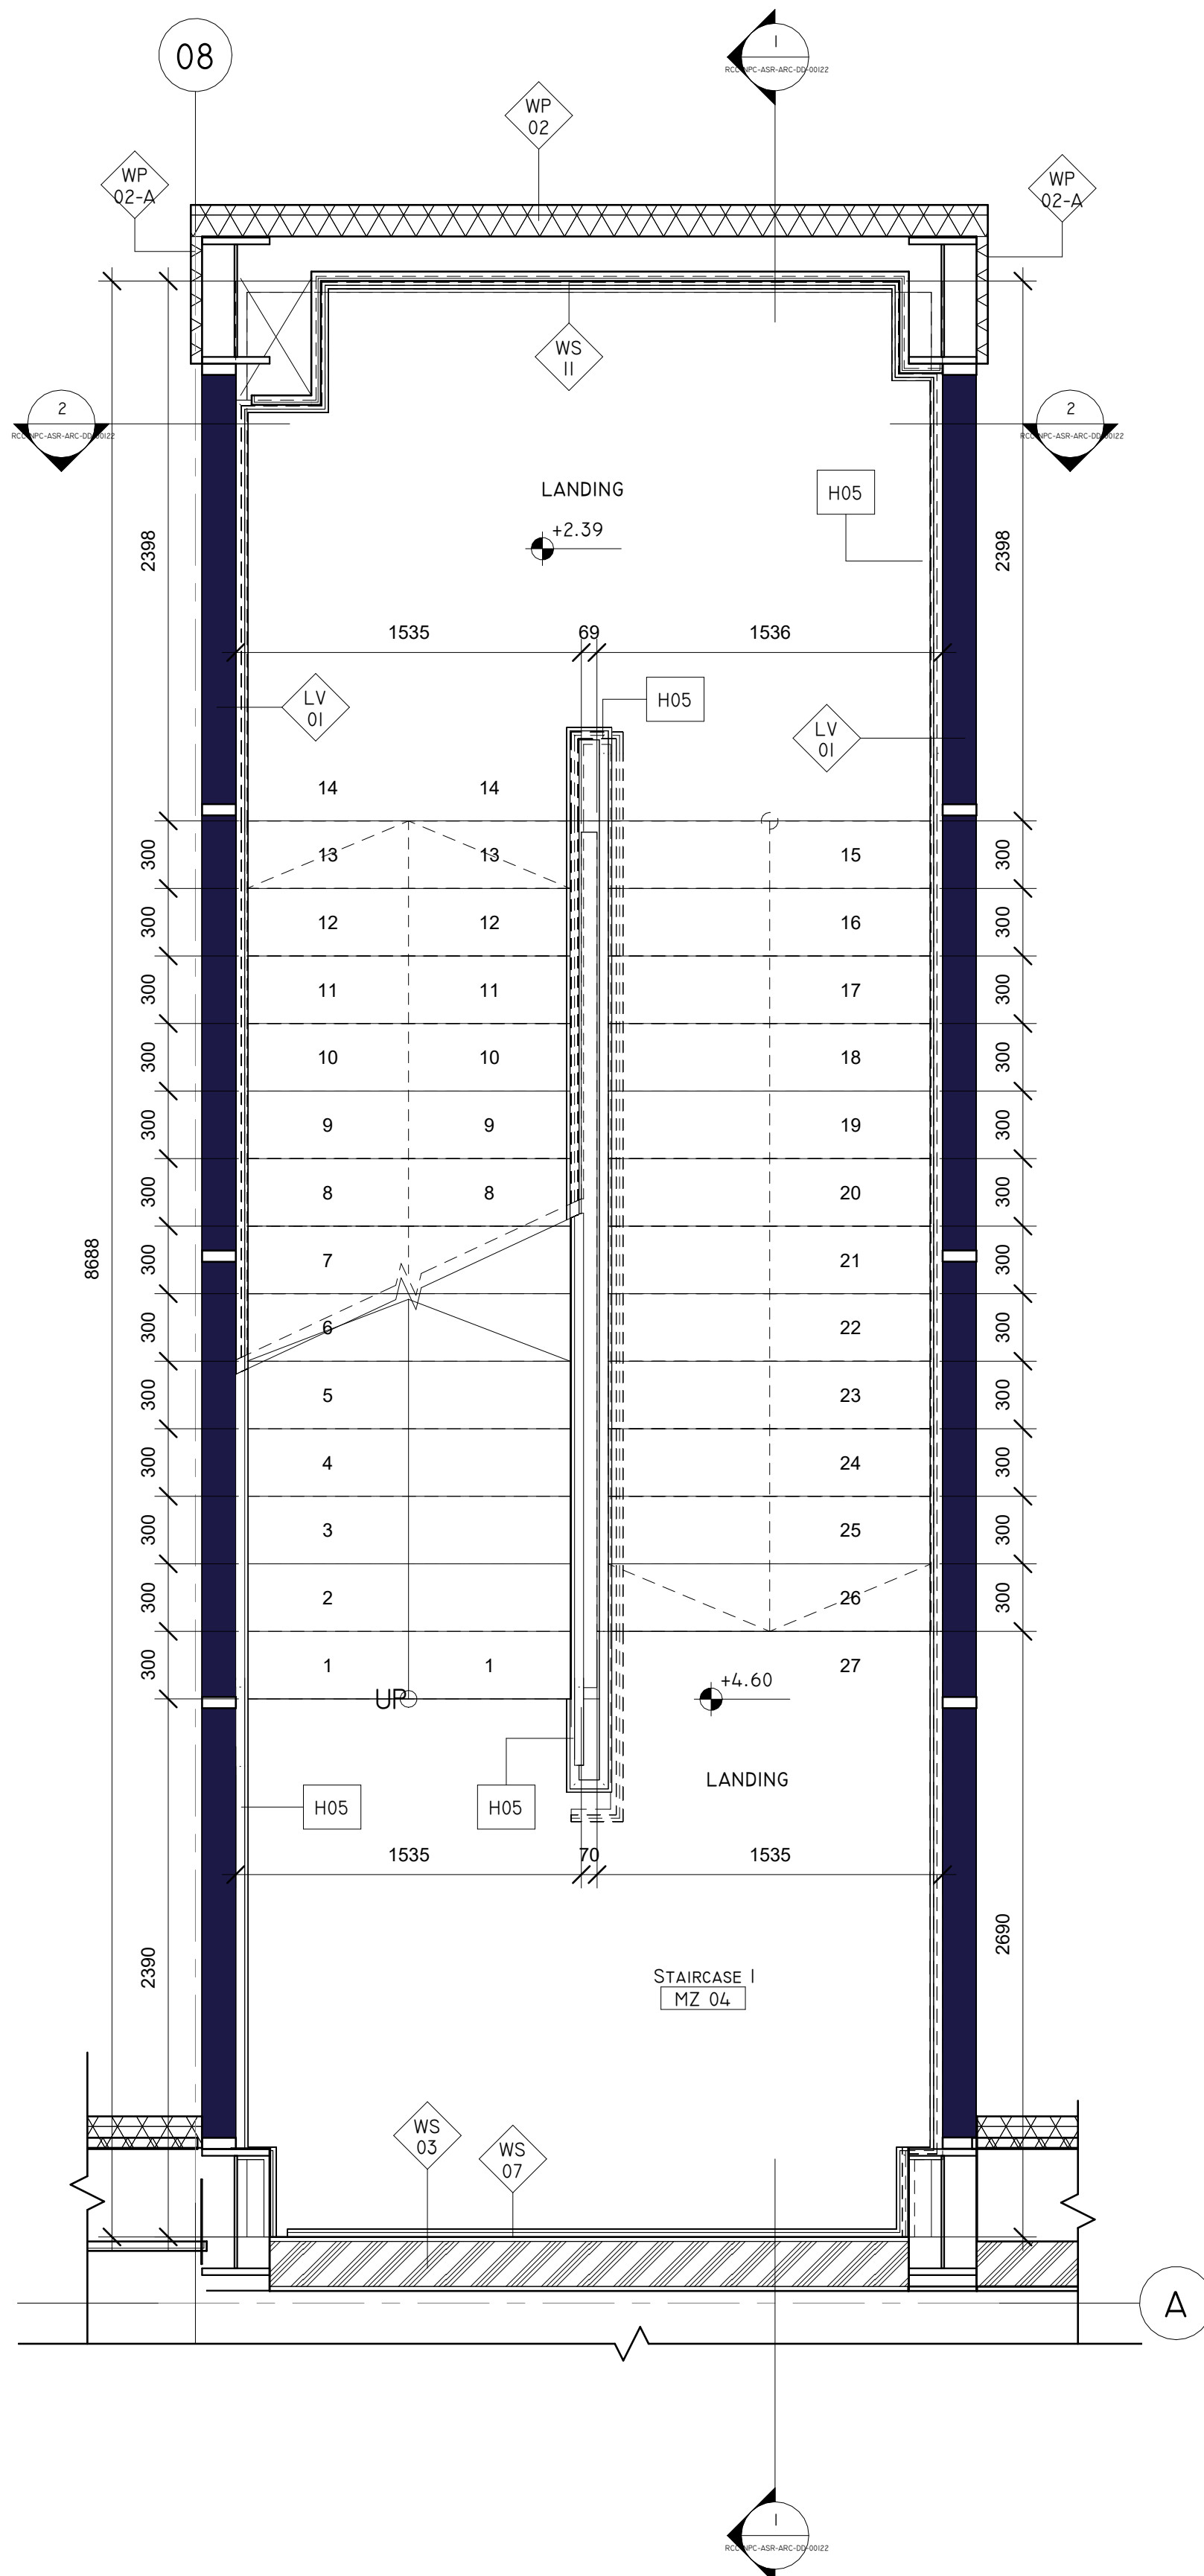

02 MEZZANINE FLOOR PLAN (STAIRCASE -I)
1 : 25

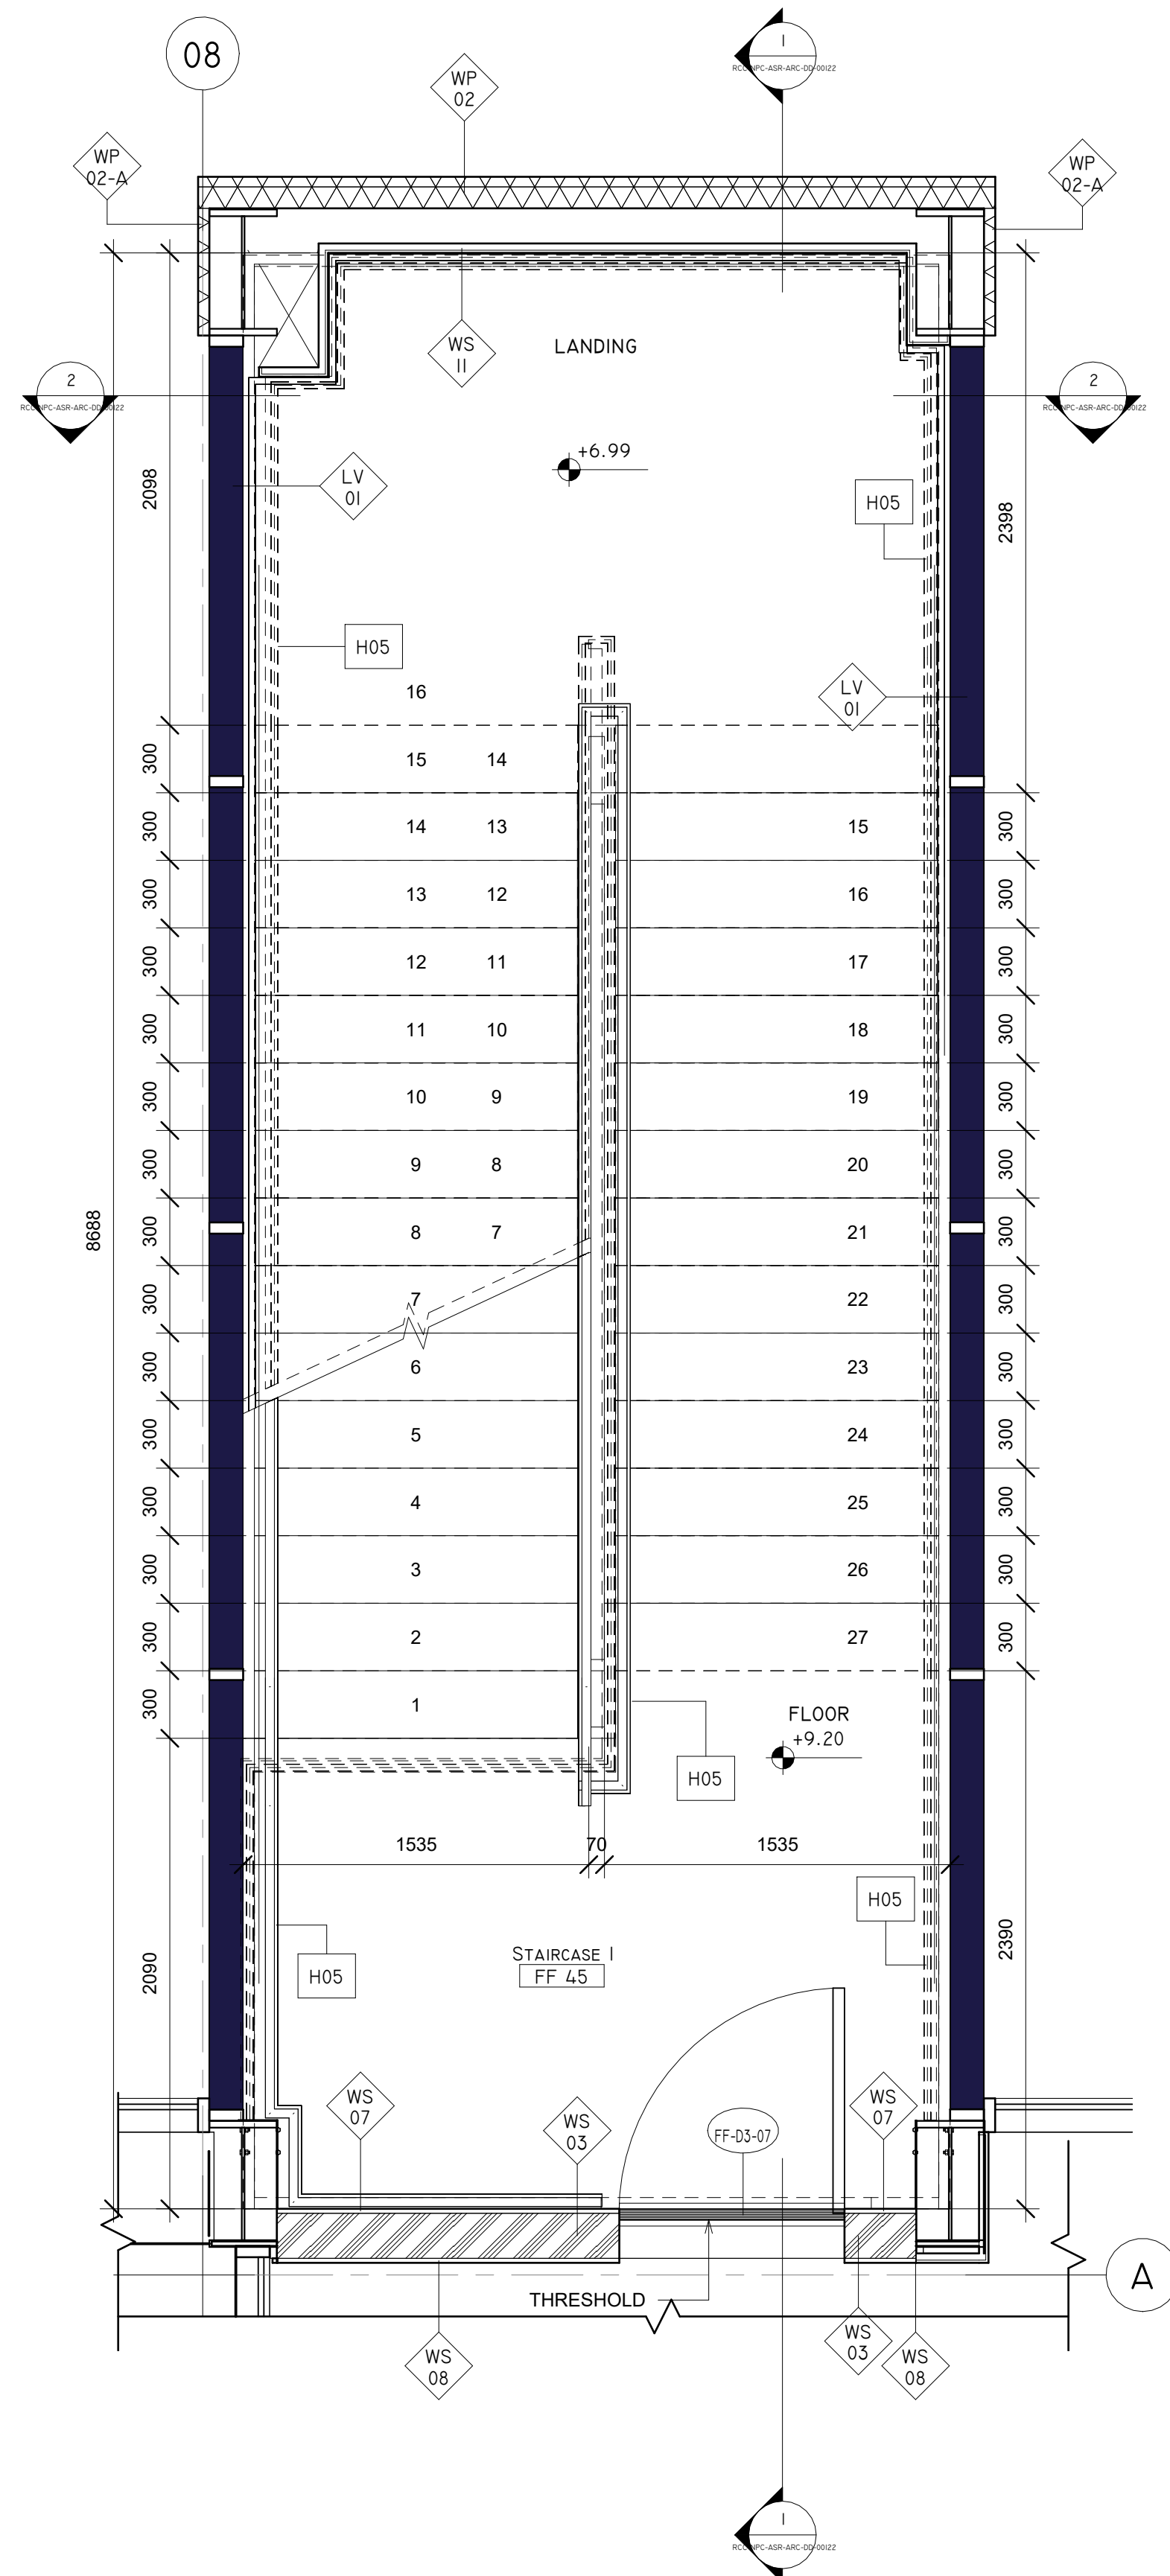

03 FIRST FLOOR PLAN (STAIRCASE -I)
1 : 25

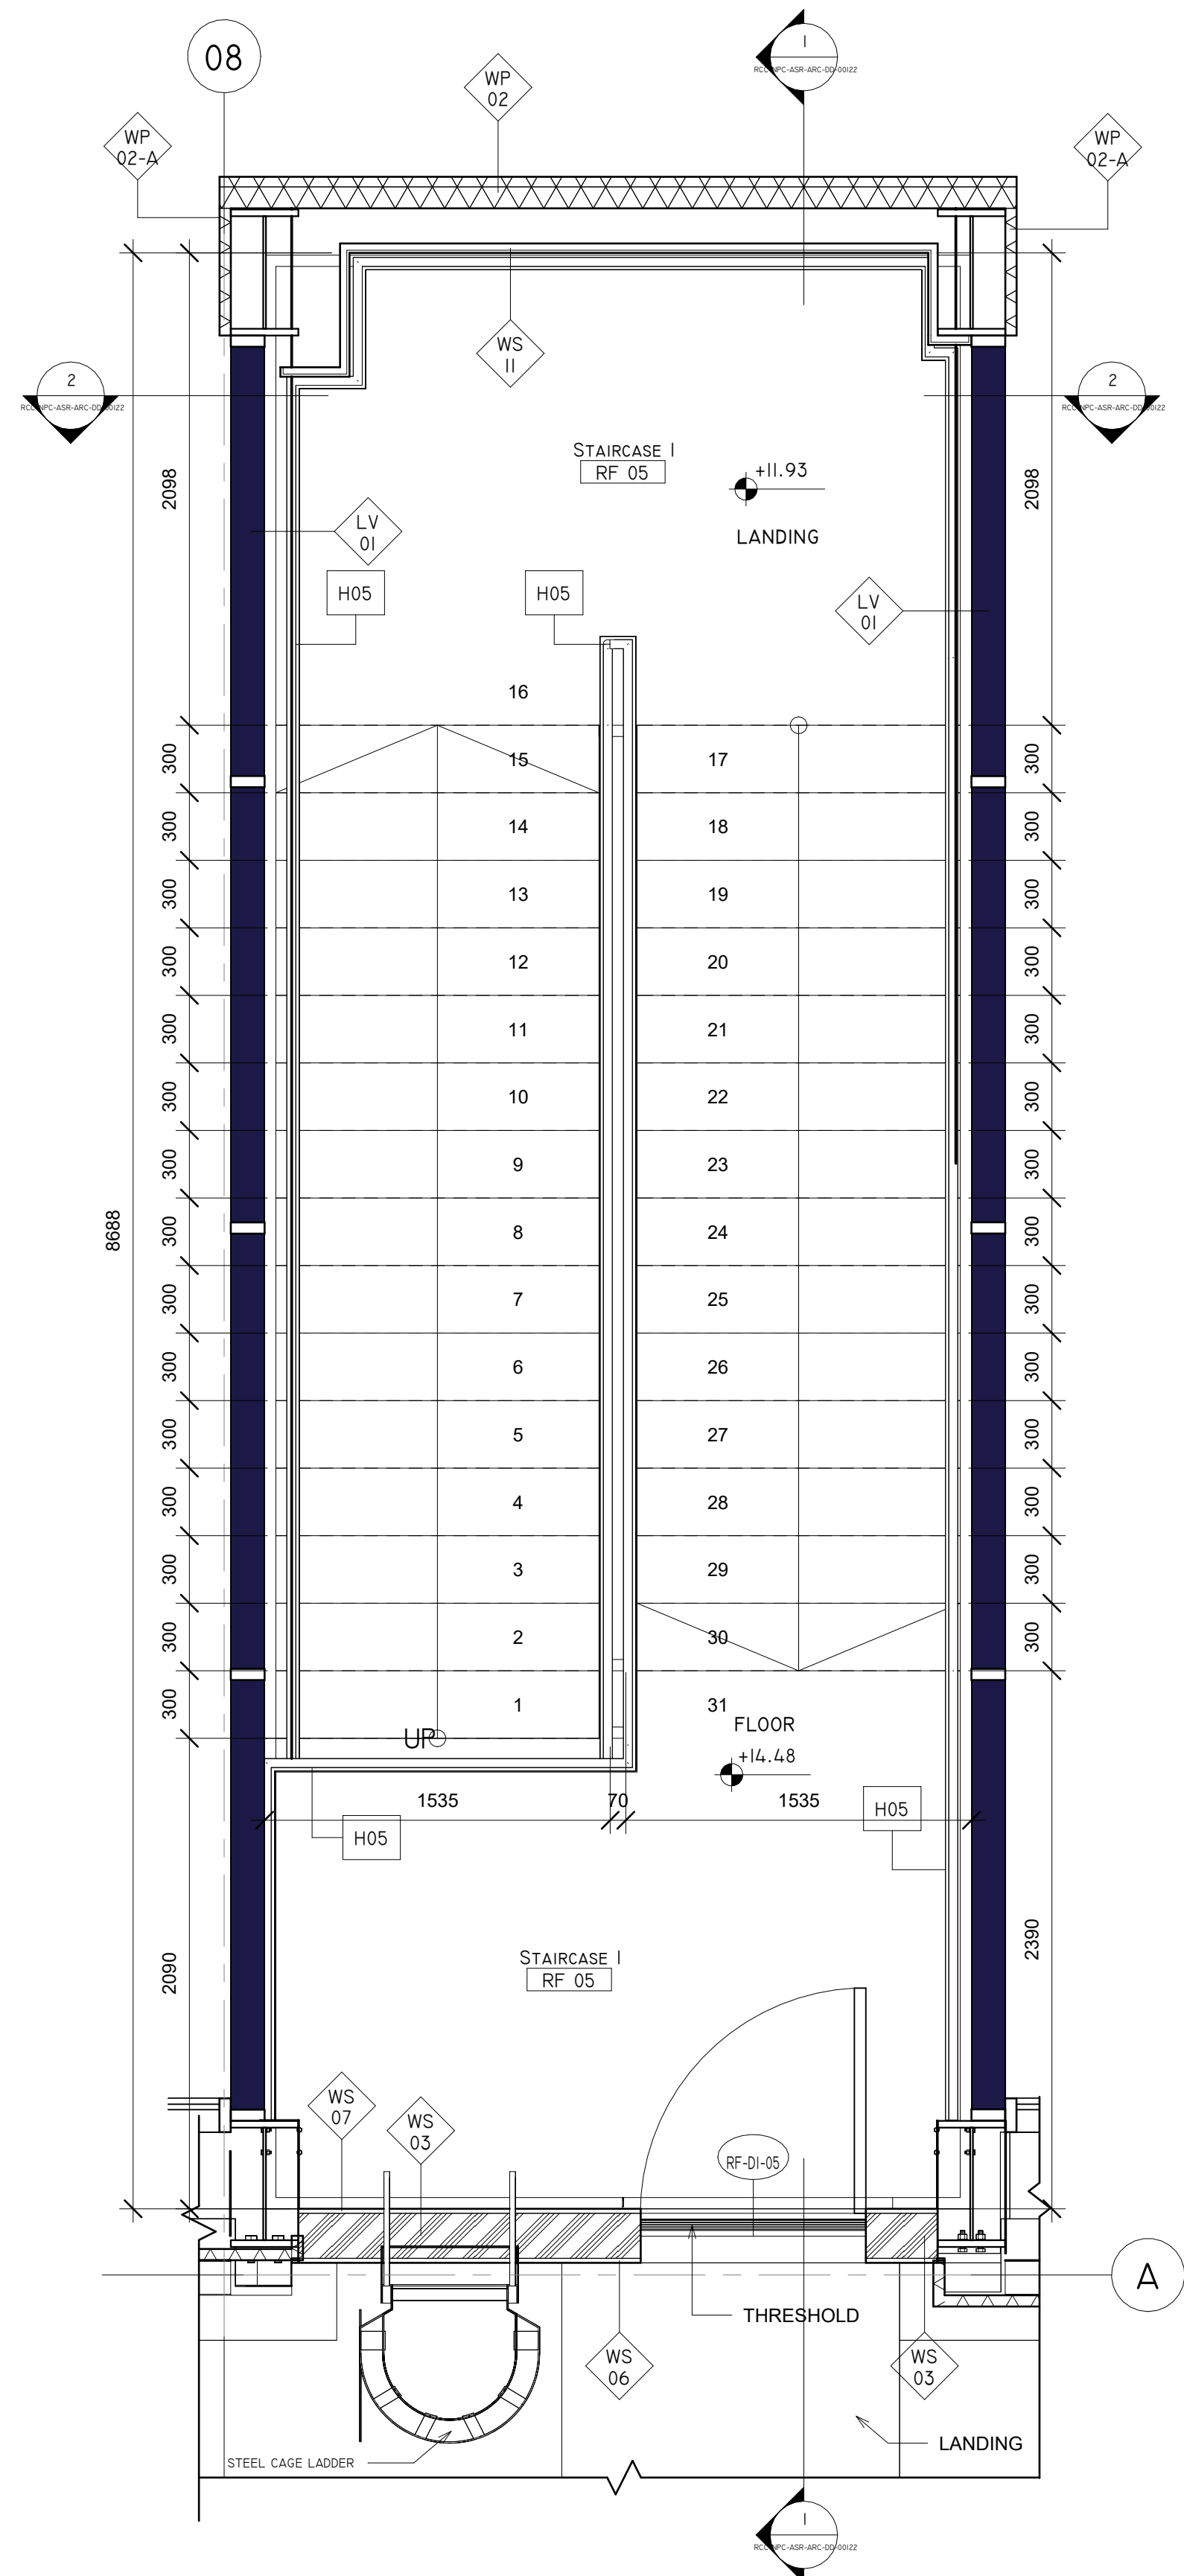

04 ROOF FLOOR PLAN (STAIRCASE -I)
1 : 25

HANDRAIL LEGEND

REF	DESCRIPTION
H01	1000MM GALVANIZED STEEL HANDRAIL - EPOXY PAINTED
H02	1000MM STAINLESS STEEL HANDRAIL
H03	1000MM STAINLESS STEEL HANDRAIL WITH GLASS
H04	1000MM STAINLESS STEEL HANDRAIL WALL MOUNTED
H05	1000MM GALVANIZED STEEL HANDRAIL WALL MOUNTED RAL 5013
H06	1000MM GALVANIZED STEEL HANDRAIL POWDER COATED RAL 5013




NOTES & LEGENDS:
1. ALL DIMENSIONS ARE IN MILLIMETERS AND ALL LEVELS GIVEN IN METERS UNLESS OTHERWISE NOTED.
2. FINISHED FLOOR AND ELEVATION - F.F.L. +0.00 METERS SHOWN IN THIS DRAWING IS EQUIVALENT TO F.F.L. +0.00 M AS REFERENCED TO SITE GRADING LAYOUT DWG NO. RCC-NPC-ASR-GY-001.
3. THIS DRAWING SHALL BE READ IN CONJUNCTION WITH RELEVANT ELECTRICAL, MECHANICAL, TELECOM AND STRUCTURAL DRAWINGS.
4. CONTRACTOR TO VERIFY ALL DIMENSIONS AND CONDITIONS ON SITE PRIOR TO THE START OF CONSTRUCTION. ANY DISCREPANCY SHOULD BE BROUGHT TO THE ATTENTION OF THE CLIENT FOR CLARIFICATION BEFORE PROCEEDING WITH THE AFFECTED PART OF WORK.

0	COLUMNS GRID	XX	SPOT ELEVATION
XX	HANDRAIL TAG	YY & ZZ	ROOM NAME & NUMBER
YY & ZZ	DOOR TAGS	ISO M2	WALL/FINISH TYPE

WALLS LEGEND

TYPE	DESCRIPTION
CW 02	GLAZED CURTAIN WALL PANELS
CW 03	SPANDREL PANELS
CW 04	FRAMELESS GLASS PARTITION
LV 01	CURTAIN LOUVER PARTITION
WP 02	EXTERIOR WALL PANEL SYSTEM 100MM THICK - COLOR WHITE
WP 03	EXTERIOR WALL PANEL SYSTEM 100MM THICK - COLOR WHITE
WP 04	EXTERIOR WALL PANEL SYSTEM 100MM THICK - COLOR WHITE
WP 05	INTERIOR WALL PANEL SYSTEM 100MM THICK 1-HR FIRE RATED
WP 06	WALL PANEL SYSTEM 100MM THICK FOR STAGING AREA
WP 07	WALL PANEL SYSTEM 100MM THICK FOR STAGING AREA
WP 08	ON-INSULATED WALL PANEL SYSTEM 100MM THICK
WP 09	SOLID POLYMER FABRICATION RESIN TOILET COMPARTMENTS
WP 10	SOLID POLYMER FABRICATION RESIN TOILET COMPARTMENTS
WP 11	SOLID POLYMER FABRICATION RESIN TOILET COMPARTMENTS
WP 12	ACP CLADDING 12MM THICK
WP 13	EXTERIOR WALL PANEL SYSTEM 100MM THICK - COLOR WHITE
WP 14	EXTERIOR WALL PANEL SYSTEM 100MM THICK - COLOR WHITE
WP 15	COMPOSITE PANEL CLADDING 200MM THICK
WP 16	WALL PANEL SYSTEM 100MM THICK FOR CHILLED & FREEZER ROOMS
WP 17	GREEN WALL
WP 18	EXTERIOR WALL PANEL SYSTEM 100MM THICK - COLOR WHITE
WP 19	DECORATIVE WOOD WALL PANELS
WS 01	CONCRETE MASONRY UNIT WALL (UNIT: 400X200; 100MM THICK)
WS 02	CONCRETE MASONRY UNIT WALL (UNIT: 400X200; 100MM THICK)
WS 03	CONCRETE MASONRY UNIT WALL (UNIT: 400X200; 200MM THICK)
WS 04	CONCRETE MASONRY UNIT WALL (UNIT: 400X200; 200MM THICK)
WS 05	CONCRETE MASONRY UNIT WALL (UNIT: 400X200; 200MM THICK)
WS 06	CONCRETE MASONRY UNIT WALL (UNIT: 400X200; 100MM THICK)
WS 07	CONCRETE MASONRY UNIT WALL (UNIT: 400X200; 100MM THICK)
WT 01	PAINTING FINISHING

KEY PLAN :

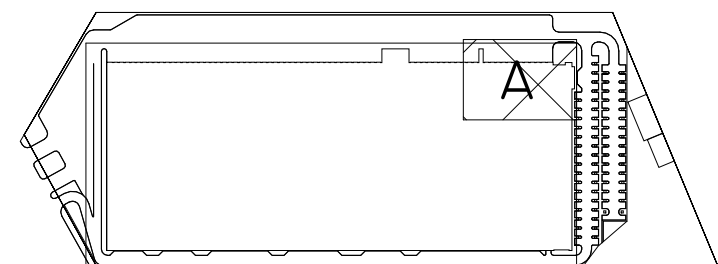

REV	DATE	DESCRIPTION
01	11/08/2025	ISSUE FOR DETAILED DESIGN
02	03/09/2025	ISSUE FOR DETAILED DESIGN
03	20/10/2025	ISSUE FOR DETAILED DESIGN

SEAL & SIGNATURE:

DRAWN BY	CHECKED BY	DATE (DD.MM.YYYY)
IBR	ZYD	03/07/2025

NUPCO WAREHOUSE
ASER, KSA

CLIENT:



PROJECT MANAGER:



PROJECT PROGRAM MANAGER



ARCHITECTURE & ENGINEERING CONSULTANT:



PHASE & DISCIPLINE:

DETAIL DESIGN
ARCHITECTURE

DRAWING TITLE:

STAIRCASE I - PLANS

PROJECT NO.	DRAWING NUMBER	REV
102	RCC-NPC-ASR-ARC-DD-00121	02
SCALE (A0)	AS INDICATED	

PLOT DATE & TIME: 07/20/2025 12:02:46 PM FILE: D:\BACX\JPNPC-RCC-30H-BH-ASR-WH-001-LANDS-WAREHOUSE-WT