


THIS DRAWING AND THE DESIGN IT COVERS ARE THE PROPERTY OF GULF CONSULT. ARCHITECTS AND ENGINEERS THE USER SHALL NOT REPRODUCE, COPY, SHARE, EXHIBIT, NOR USE EXCEPT IN A LIMITED WAY AND PRIVATE USE PERMITTED BY WRITTEN CONSENT GIVEN BY THE CONSULTANT.

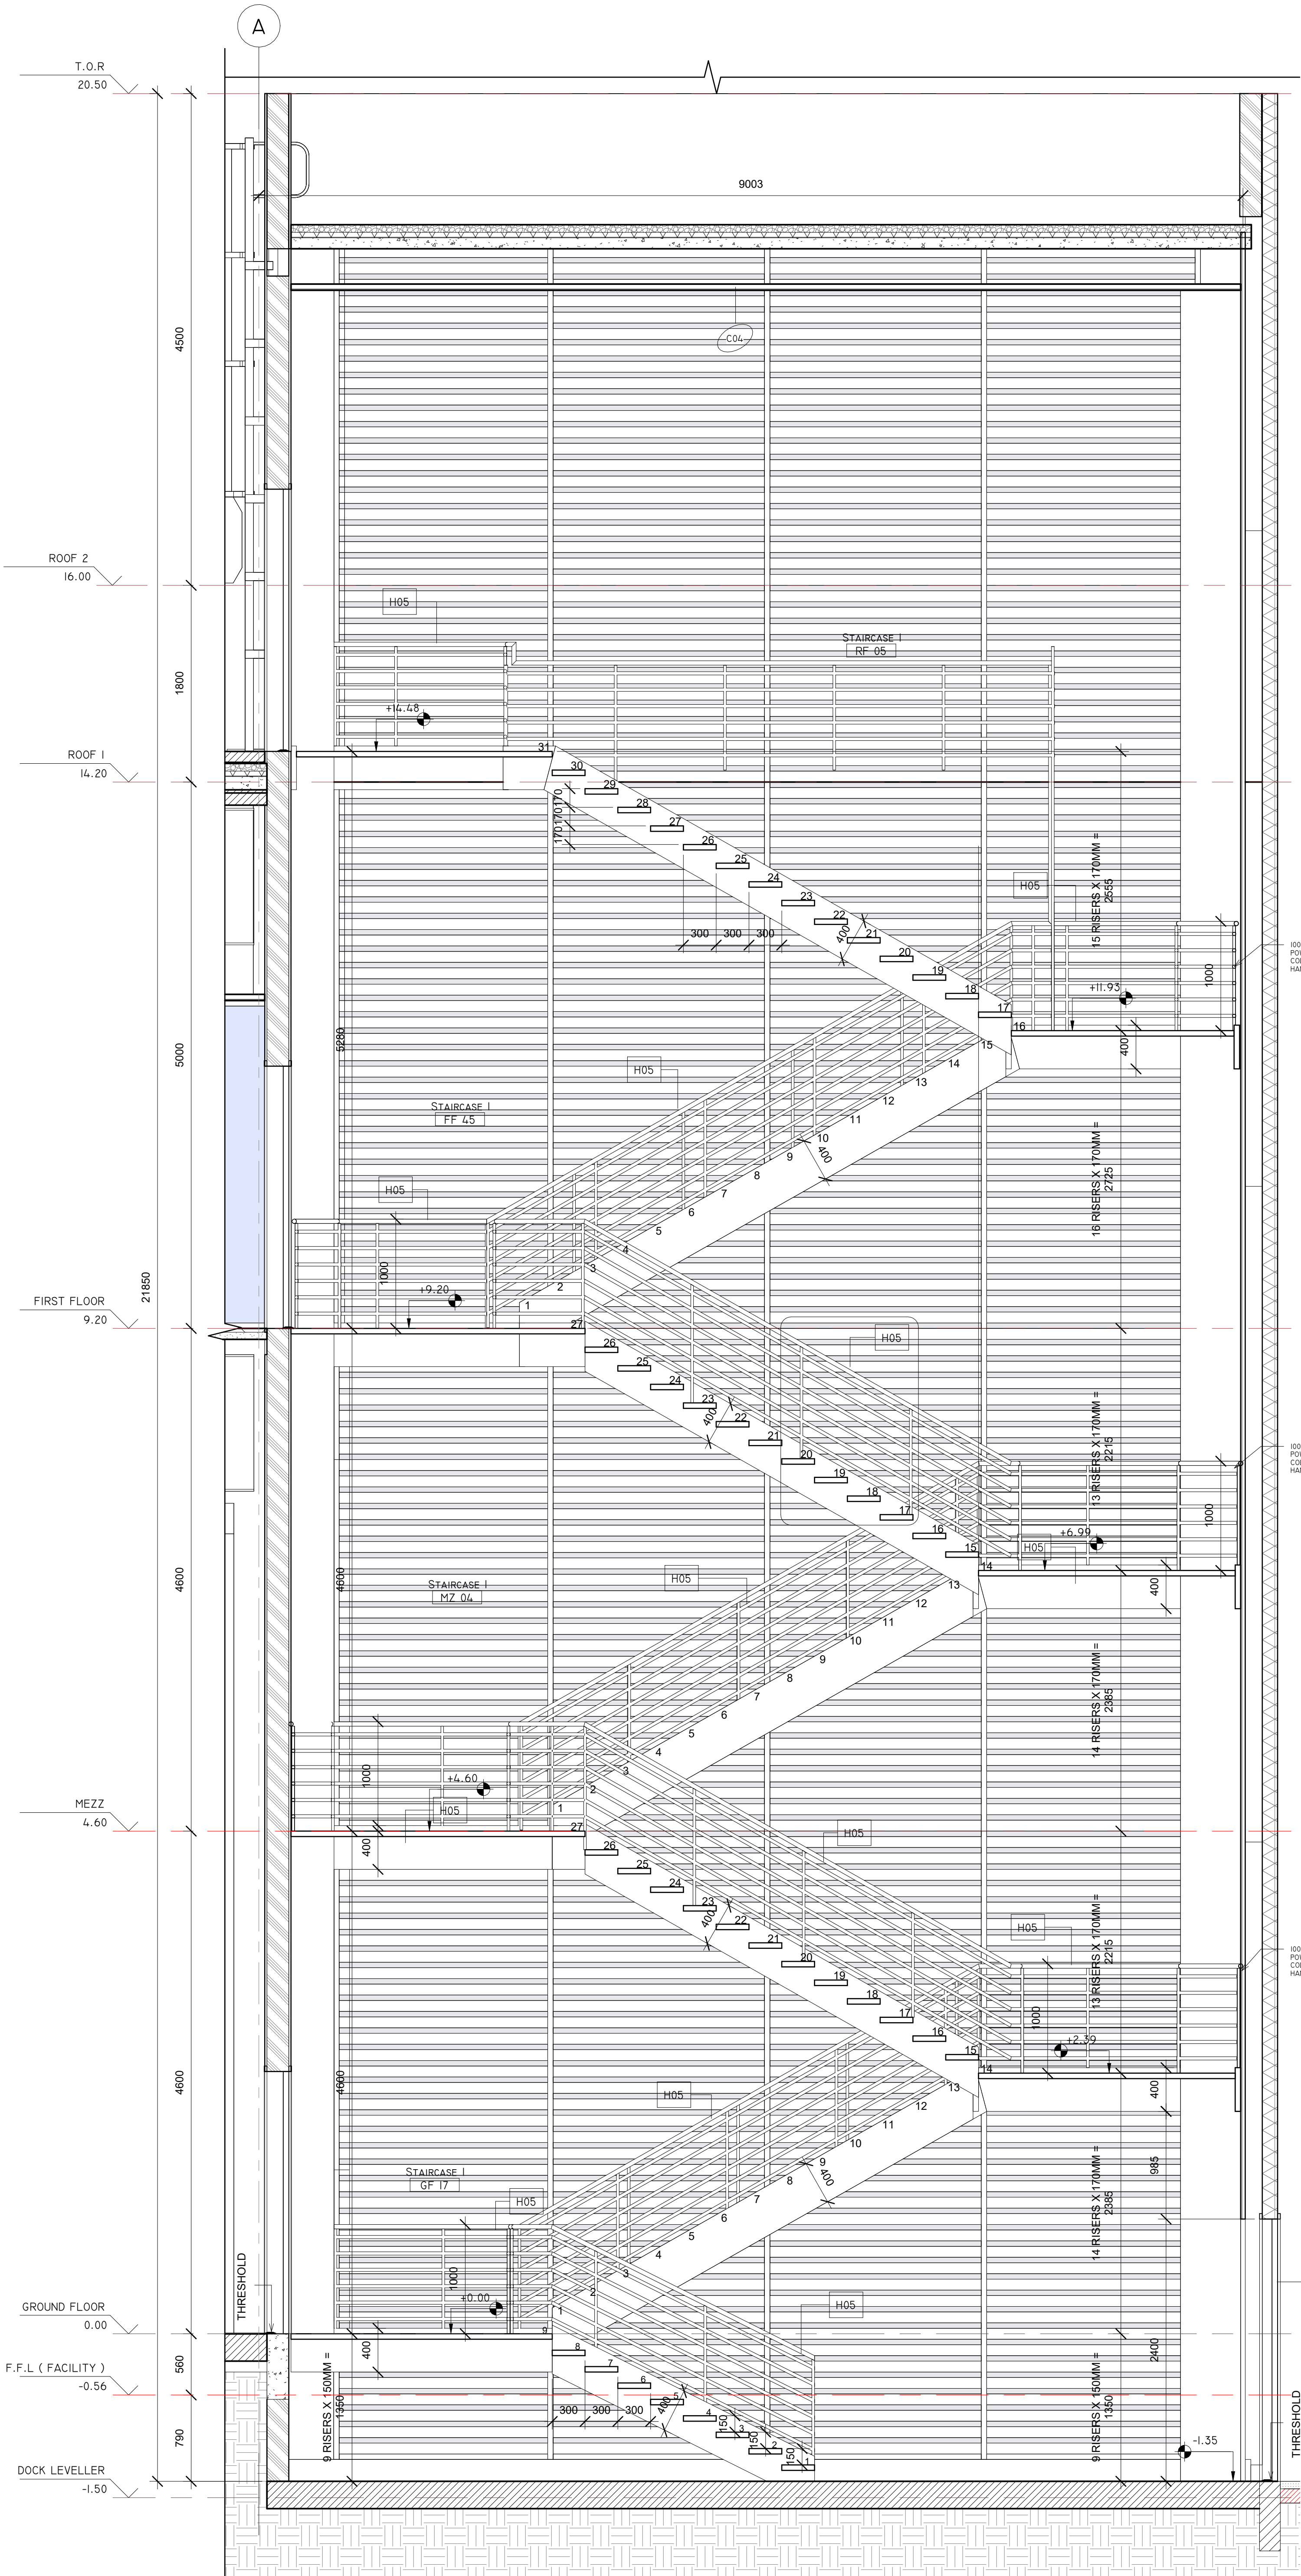

1 SECTION-I (STAIRCASE -I)
1 : 30

2 SECTION -2 (STAIRCASE -I)
1 : 30

HANDRAIL LEGEND

REF	DESCRIPTION
H01	100MM GALVANIZED STEEL HANDRAIL - EPOXY PAINTED
H02	100MM STAINLESS STEEL HANDRAIL
H03	100MM STAINLESS STEEL HANDRAIL WITH GLASS
H04	100MM STAINLESS STEEL HANDRAIL WALL MOUNTED
H05	100MM GALVANIZED STEEL HANDRAIL WALL MOUNTED
H06	100MM GALVANIZED STEEL HANDRAIL POWDER COATED

CEILING LEGEND

REF	DESCRIPTION
C01	FIBER GYPSUM CEILING 600X600 MM
C02	PERFORATED METAL CEILING- 600X600MM GRID- MOISTURE RESISTANT
C03	FIBER GYPSUM CEILING 600X200 MM
C04	PAINTED GYPSUM BOARD SUSPENDED CEILING
C05	INSULATED ROOF SANDWICH PANEL - 150MM THICK
C06	COLD ROOM INSULATED PANELS - 200MM THICK
C07	BAFFLE CEILING




NOTES & LEGENDS:

1. ALL DIMENSIONS ARE IN MILLIMETERS AND ALL LEVELS GIVEN IN METERS UNLESS OTHERWISE NOTED.
2. FINISHED FLOOR AND ELEVATION: F.F.L. +0.00 METERS SHOWN IN THIS DRAWING IS EQUIVALENT TO F.F.L. +0.00 M AS REFERENCED TO SITE GRADING LAYOUT DWG NO. RCC-NPC-ASR-CIV-001-001.
3. THIS DRAWING SHALL BE READ IN CONJUNCTION WITH RELEVANT ELECTRICAL, MECHANICAL, TELECOM AND STRUCTURAL DRAWINGS.
4. CONTRACTOR TO VERIFY ALL DIMENSIONS AND CONDITIONS ON SITE PRIOR TO THE START OF CONSTRUCTION. ANY DISCREPANCY SHOULD BE BROUGHT TO THE ATTENTION OF THE CLIENT FOR CLARIFICATION BEFORE PROCEEDING WITH THE AFFECTED PART OF WORK.

0	COLUMN GRID	XX	SPOT ELEVATION
01	FURNITURE TAG	YY A ZZ	ROOM NAME & NUMBER
02	DOOR TAGS	R0 M2	WALL/FINISH TYPE


WALLS LEGEND

TYPE	DESCRIPTION
CW 02	GLAZED CURTAIN WALL PANELS
CW 03	SPANREL PANELS
CW 04	FRAMELESS GLASS PARTITION
LV 01	CURTAIN COVER PARTITION
WP 02	EXTERIOR WALL PANEL SYSTEM 150MM THICK - COLOR WHITE
WP 03	EXTERIOR WALL PANEL SYSTEM 150MM THICK - COLOR WHITE
WP 04	INTERIOR WALL PANEL SYSTEM 150MM THICK 1-HR FIRE RATED
WP 05	WALL PANEL SYSTEM 100MM THICK FOR STAGING AREA
WP 06	WALL PANEL SYSTEM 100MM THICK FOR STAGING AREA
WP 07	ON-INSULATED WALL PANEL SYSTEM 150MM THICK
WP 08	SOLID POLYMER FABRICATION RESIN TOILET COMPARTMENTS
WP 09	SOLID POLYMER FABRICATION RESIN TOILET COMPARTMENTS
WP 10	SOLID POLYMER FABRICATION RESIN TOILET COMPARTMENTS
WP 11	ACF CLADDING 1MM THICK
WP 12	EXTERIOR WALL PANEL SYSTEM 150MM THICK - COLOR WHITE
WP 13	EXTERIOR WALL PANEL SYSTEM 150MM THICK - COLOR WHITE
WP 14	COMPOSITE PANEL CLADDING 20MM THICK
WP 15	WALL PANEL SYSTEM 150MM THICK FOR CHILLED & FREEZER ROOMS
WP 16	GREEN WALL
WP 17	EXTERIOR WALL PANEL SYSTEM 150MM THICK - COLOR WHITE
WP 18	DECORATIVE WOOD WALL PANELS
WS 01	CONCRETE MASONRY UNIT WALL (UNIT: 400X200; 150MM THICK)
WS 02	CONCRETE MASONRY UNIT WALL (UNIT: 400X200; 150MM THICK)
WS 03	CONCRETE MASONRY UNIT WALL (UNIT: 400X200; 200MM THICK)
WS 04	CONCRETE MASONRY UNIT WALL (UNIT: 400X200; 200MM THICK)
WS 05	CONCRETE MASONRY UNIT WALL (UNIT: 400X200; 150MM THICK)
WS 06	CONCRETE MASONRY UNIT WALL (UNIT: 400X200; 150MM THICK)
WS 07	20MM THICK SAND CEMENT PLASTER TO EXTERNAL WALLS INCLUDING EXTERNAL PAINT
WS 08	20MM THICK SAND CEMENT PLASTER TO INTERNAL WALLS WITH WASHABLE OIL PAINT
WS 09	20MM THICK SAND CEMENT PLASTER TO INTERNAL WALLS INCLUDING EMULSION PAINT
WS 10	20MM THICK INSULATED TWO LAYERS OF GYPSUM BOARD FROM EACH SIDE - WALL PARTITIONS
WS 11	20MM THICK INSULATED GYPSUM DRYWALL CLADDING
WS 12	20MM THICK INSULATED GYPSUM DRYWALL CLADDING
WS 13	20MM THICK INSULATED GYPSUM DRYWALL CLADDING
WS 14	20MM THICK INSULATED GYPSUM BOARD WALL PANELS
WT 01	PAINTING FINISHING

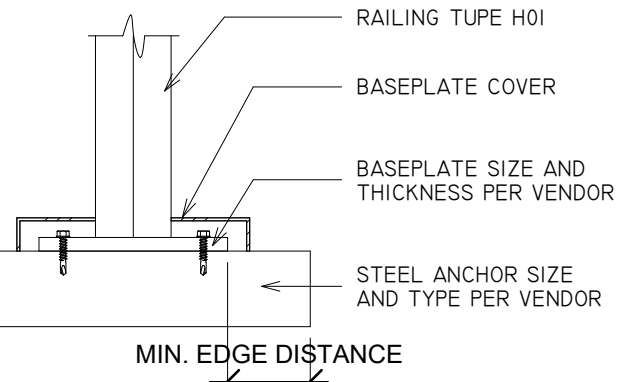


RAILING DETAILS

1 : 5

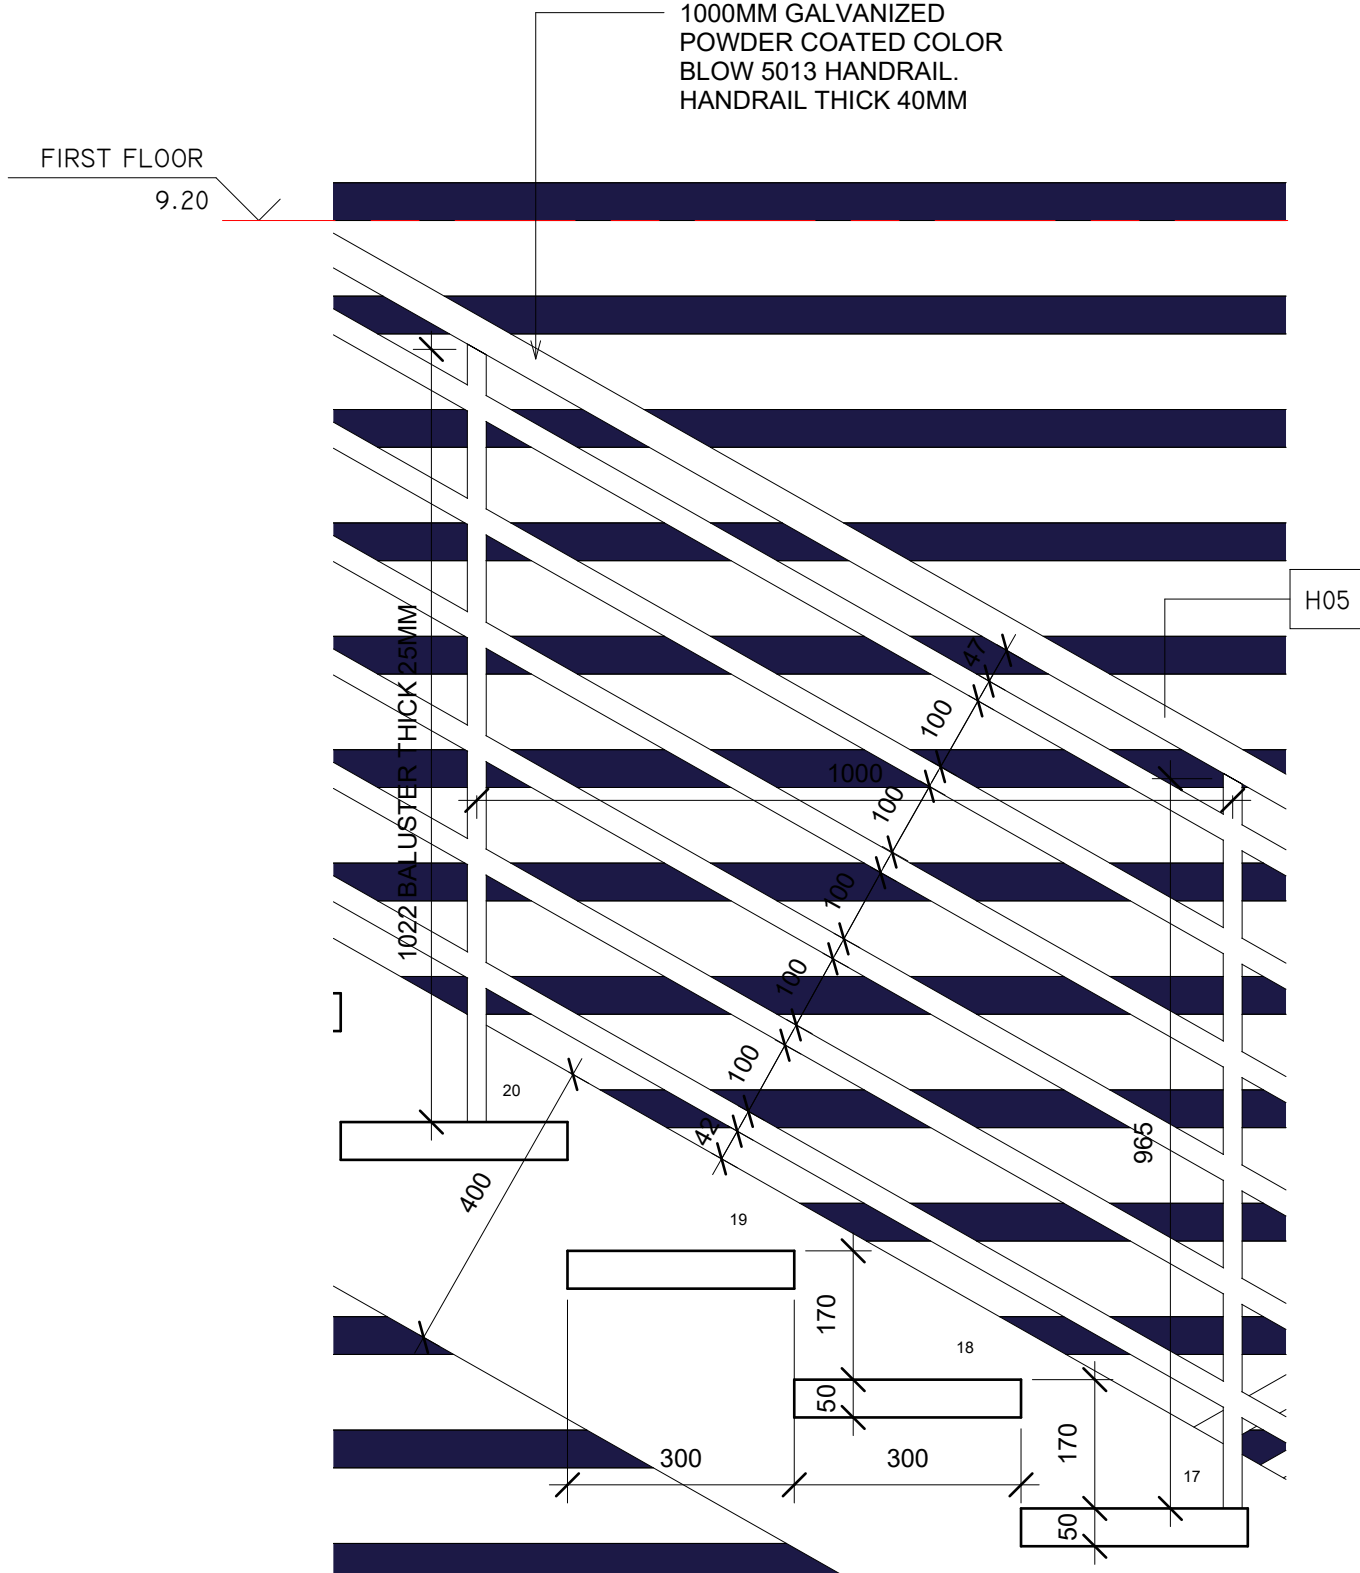

4 SECTION-I (STAIRCASE -I) - CALLOUT I
1 : 10

KEY PLAN :

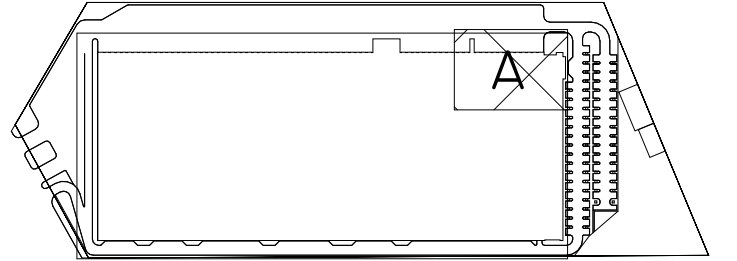

REV.	DATE	DESCRIPTION OF REVISION
00	16/08/2025	ISSUE FOR DETAILED DESIGN
01	03/09/2025	ISSUE FOR DETAILED DESIGN
02	20/10/2025	ISSUE FOR DETAILED DESIGN

SEAL & SIGNATURE:

DRAWN BY	CHECKED BY	DATE (DD.MM.YYYY)
AHM	ZYD	03/07/2025

NUPCO WAREHOUSE
ASER, KSA

CLIENT:



PROJECT MANAGER:



PROJECT PROGRAM MANAGER:



ARCHITECTURE & ENGINEERING CONSULTANT:



PHASE & DISCIPLINE:

DETAIL DESIGN
ARCHITECTURE

DRAWING TITLE:

STAIRCASE I - SECTIONS

PROJECT NO.	DRAWING NUMBER	REV
102	RCC-NPC-ASR-ARC-DD-00122	02
SCALE (A0)	AS INDICATED	

PLOT DATE & TIME: 03/07/2025 12:02:50 PM FILE: D:\BACKUP\NUPCO\RCC-30M-SH-ASR-WH-001-LANDS-WAREHOUSE-INT