




THIS DRAWING AND THE DESIGN IT COVERS ARE THE PROPERTY OF GULF CONSULT. ARCHITECTS AND ENGINEERS THE USER SHALL NOT REPRODUCE, COPY, SHARE, ENHANCE, NOR USE EXCEPT IN A LIMITED WAY AND PRIVATE USE PERMITTED BY WRITTEN CONSENT GIVEN BY THE CONSULTANT.

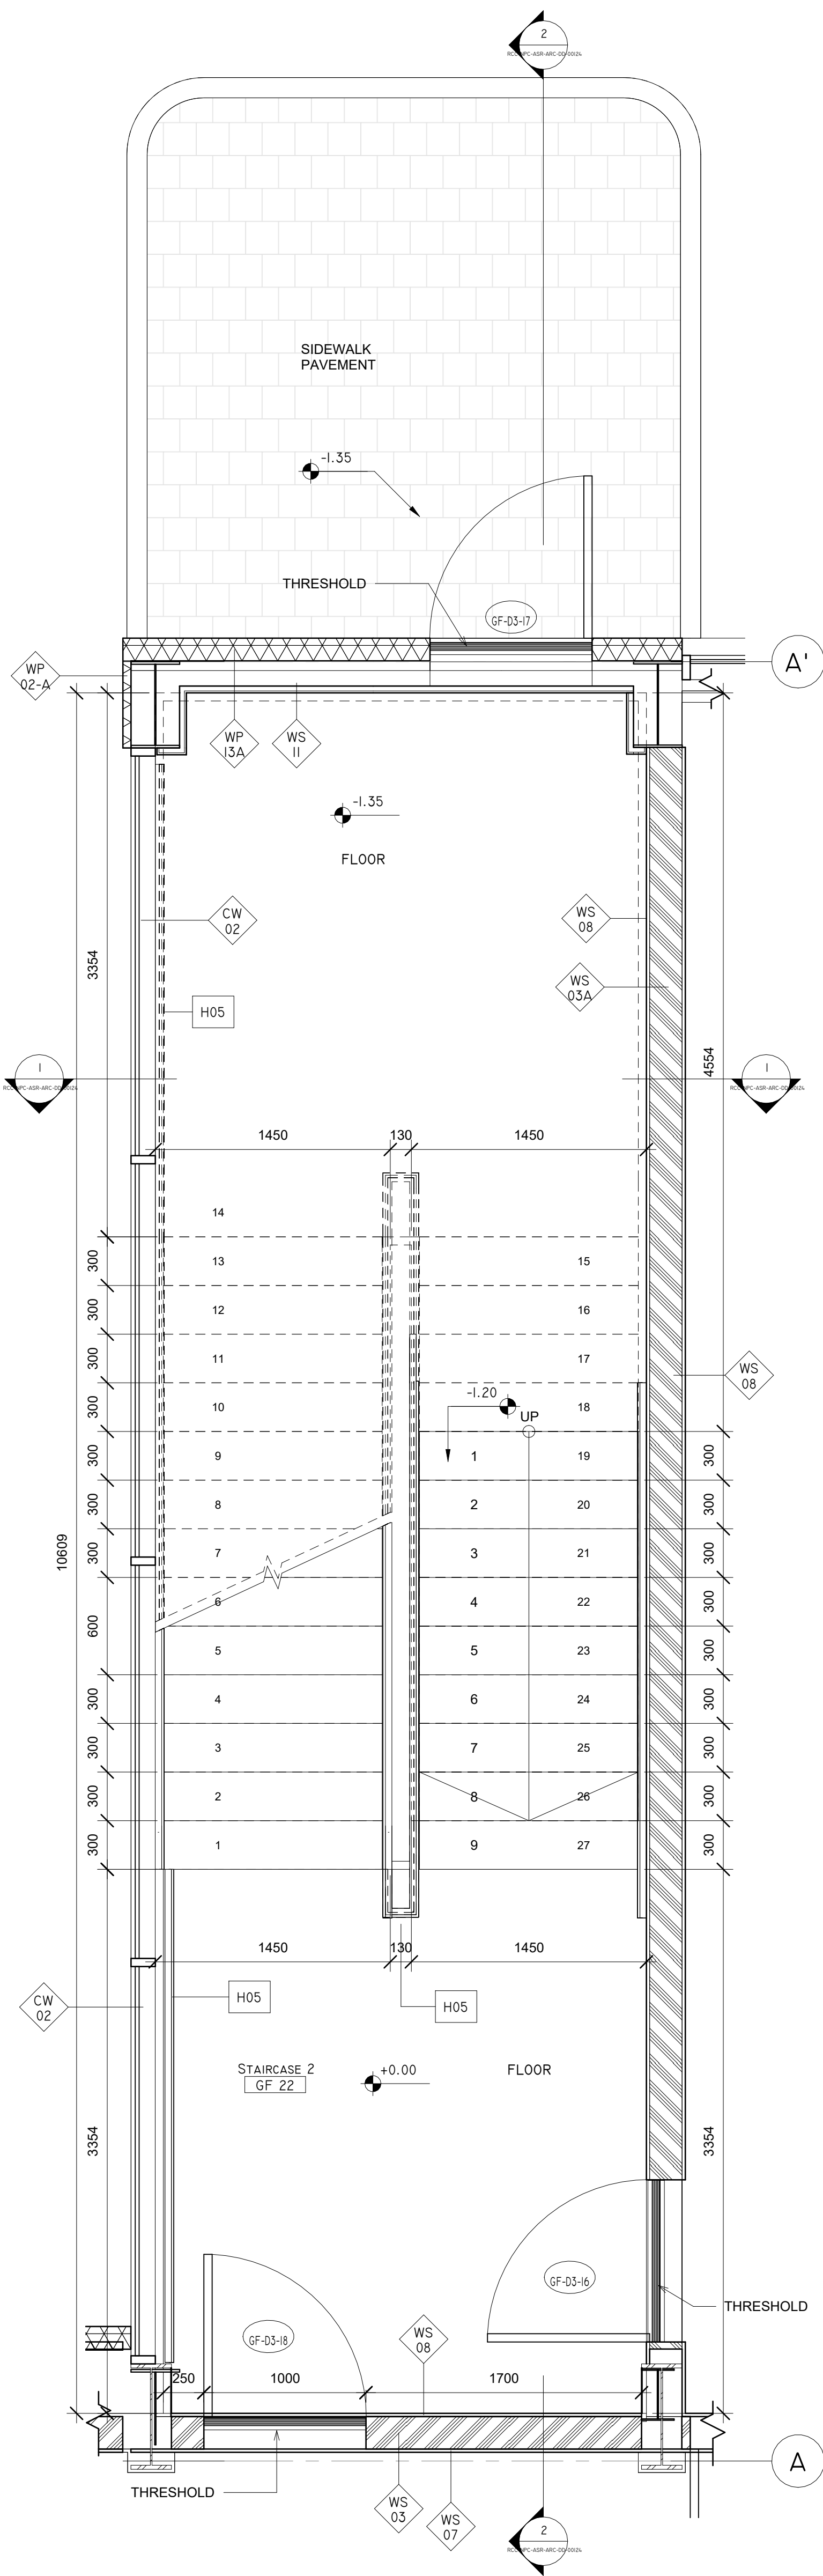


01 GROUND FLOOR PLAN (STAIRCASE -2)
1 : 25

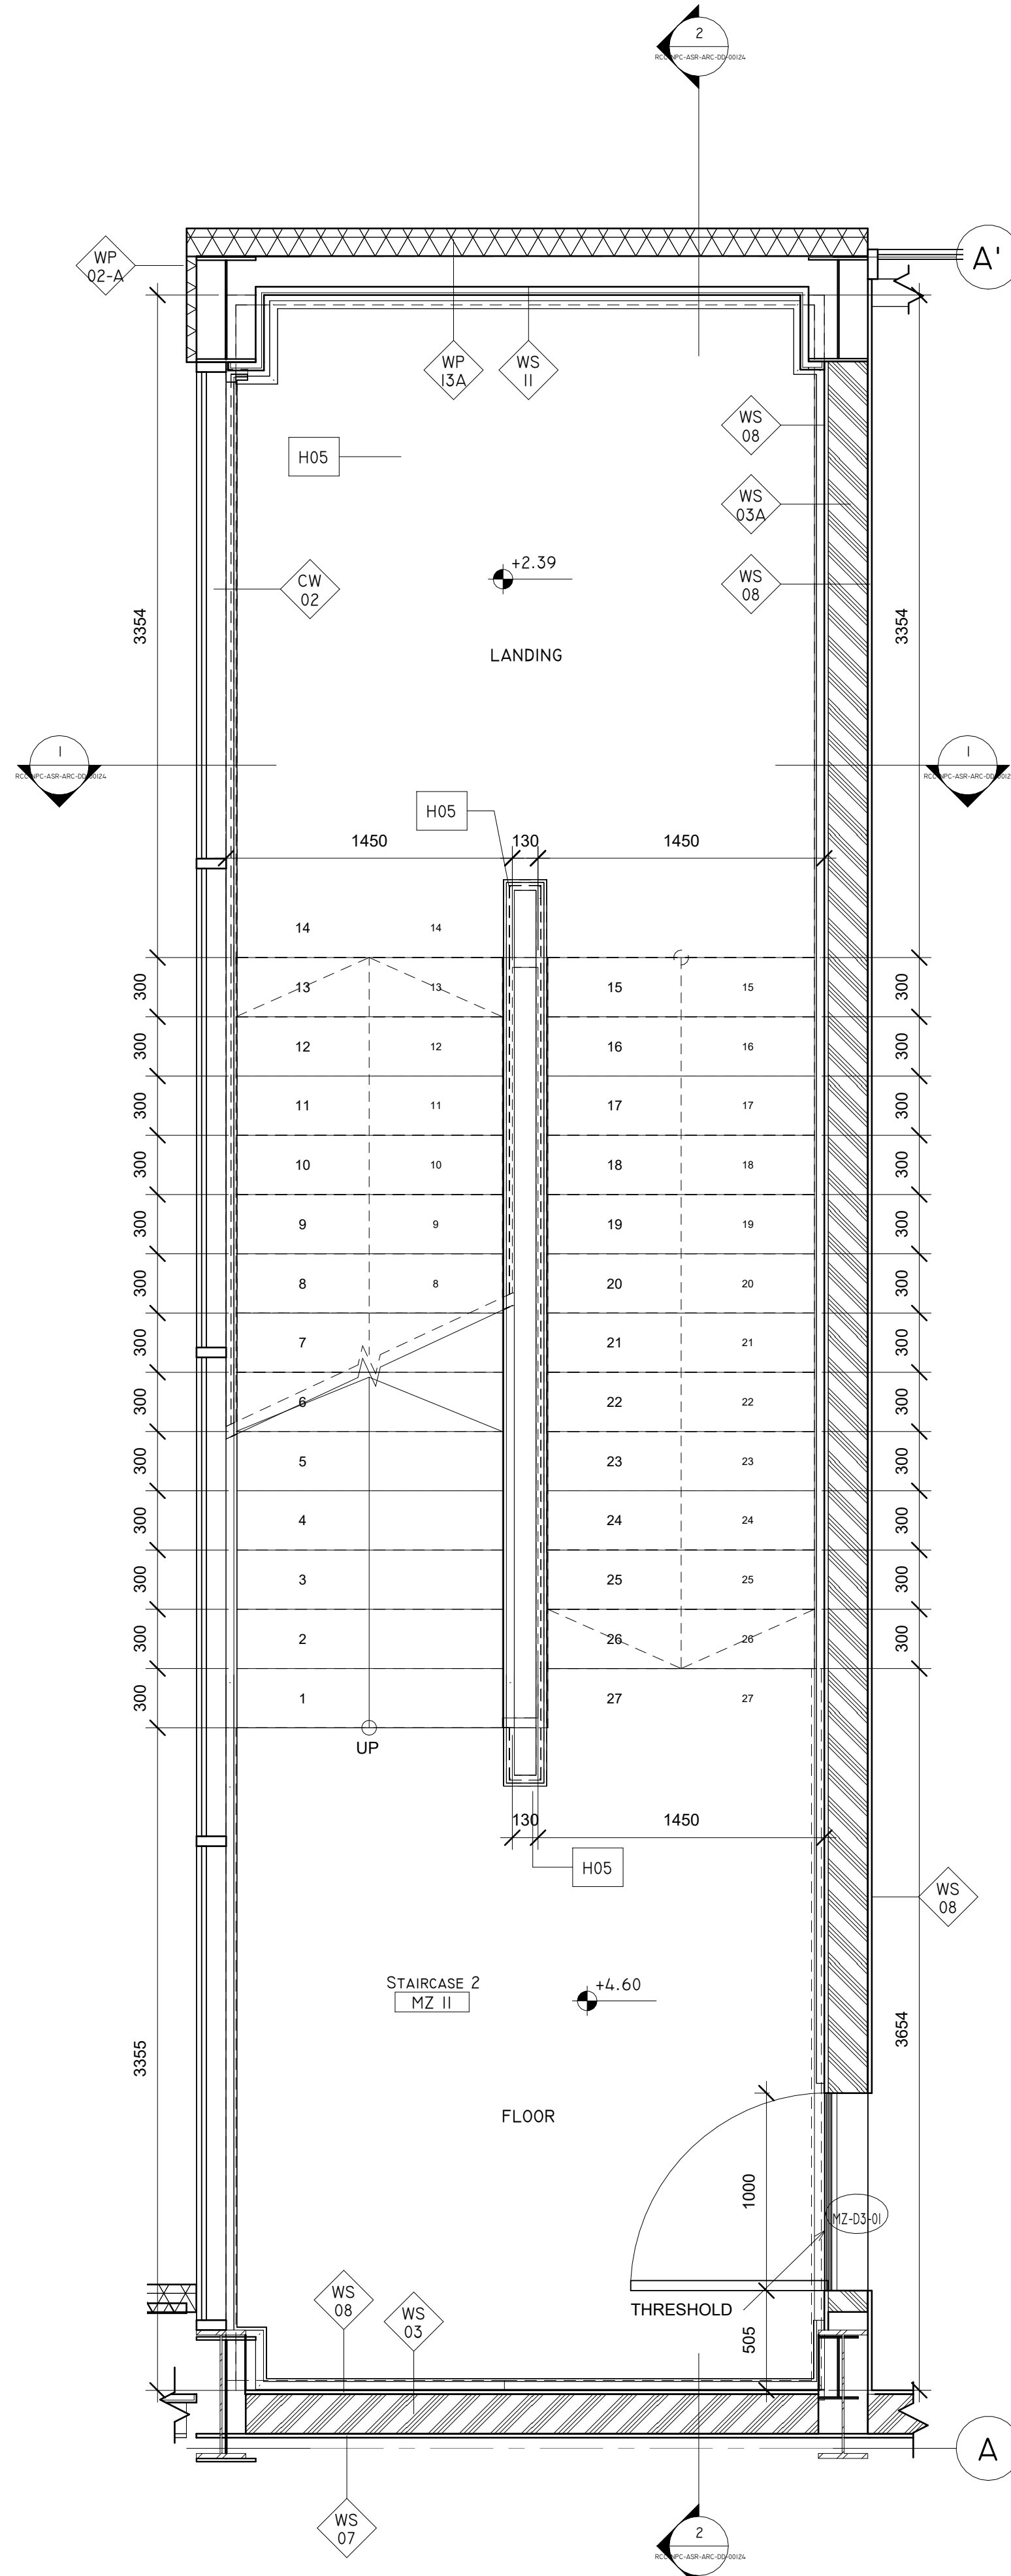

02 MEZZANINE FLOOR PLAN (STAIRCASE -2)
1 : 25

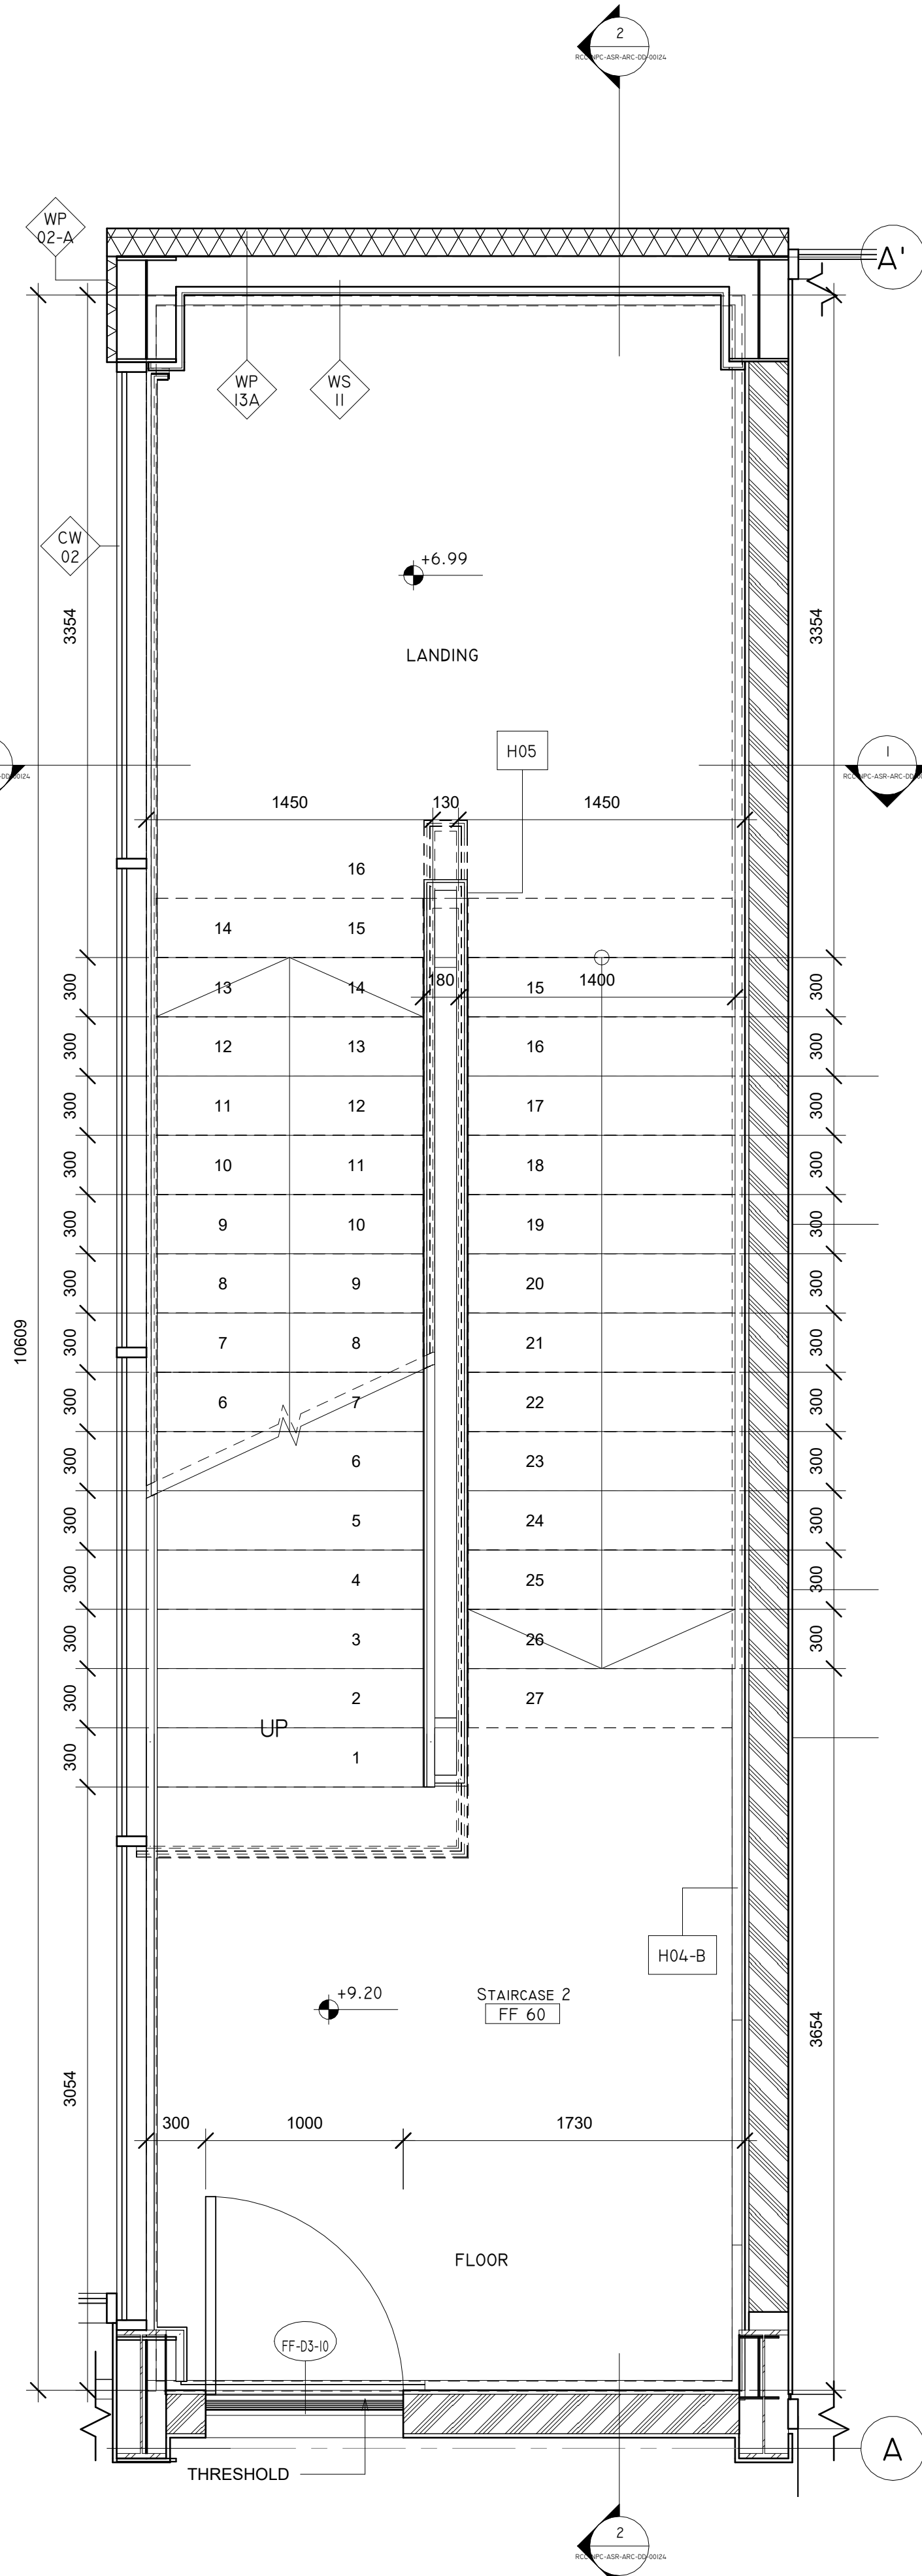

03 FIRST FLOOR PLAN (STAIRCASE -2)
1 : 25

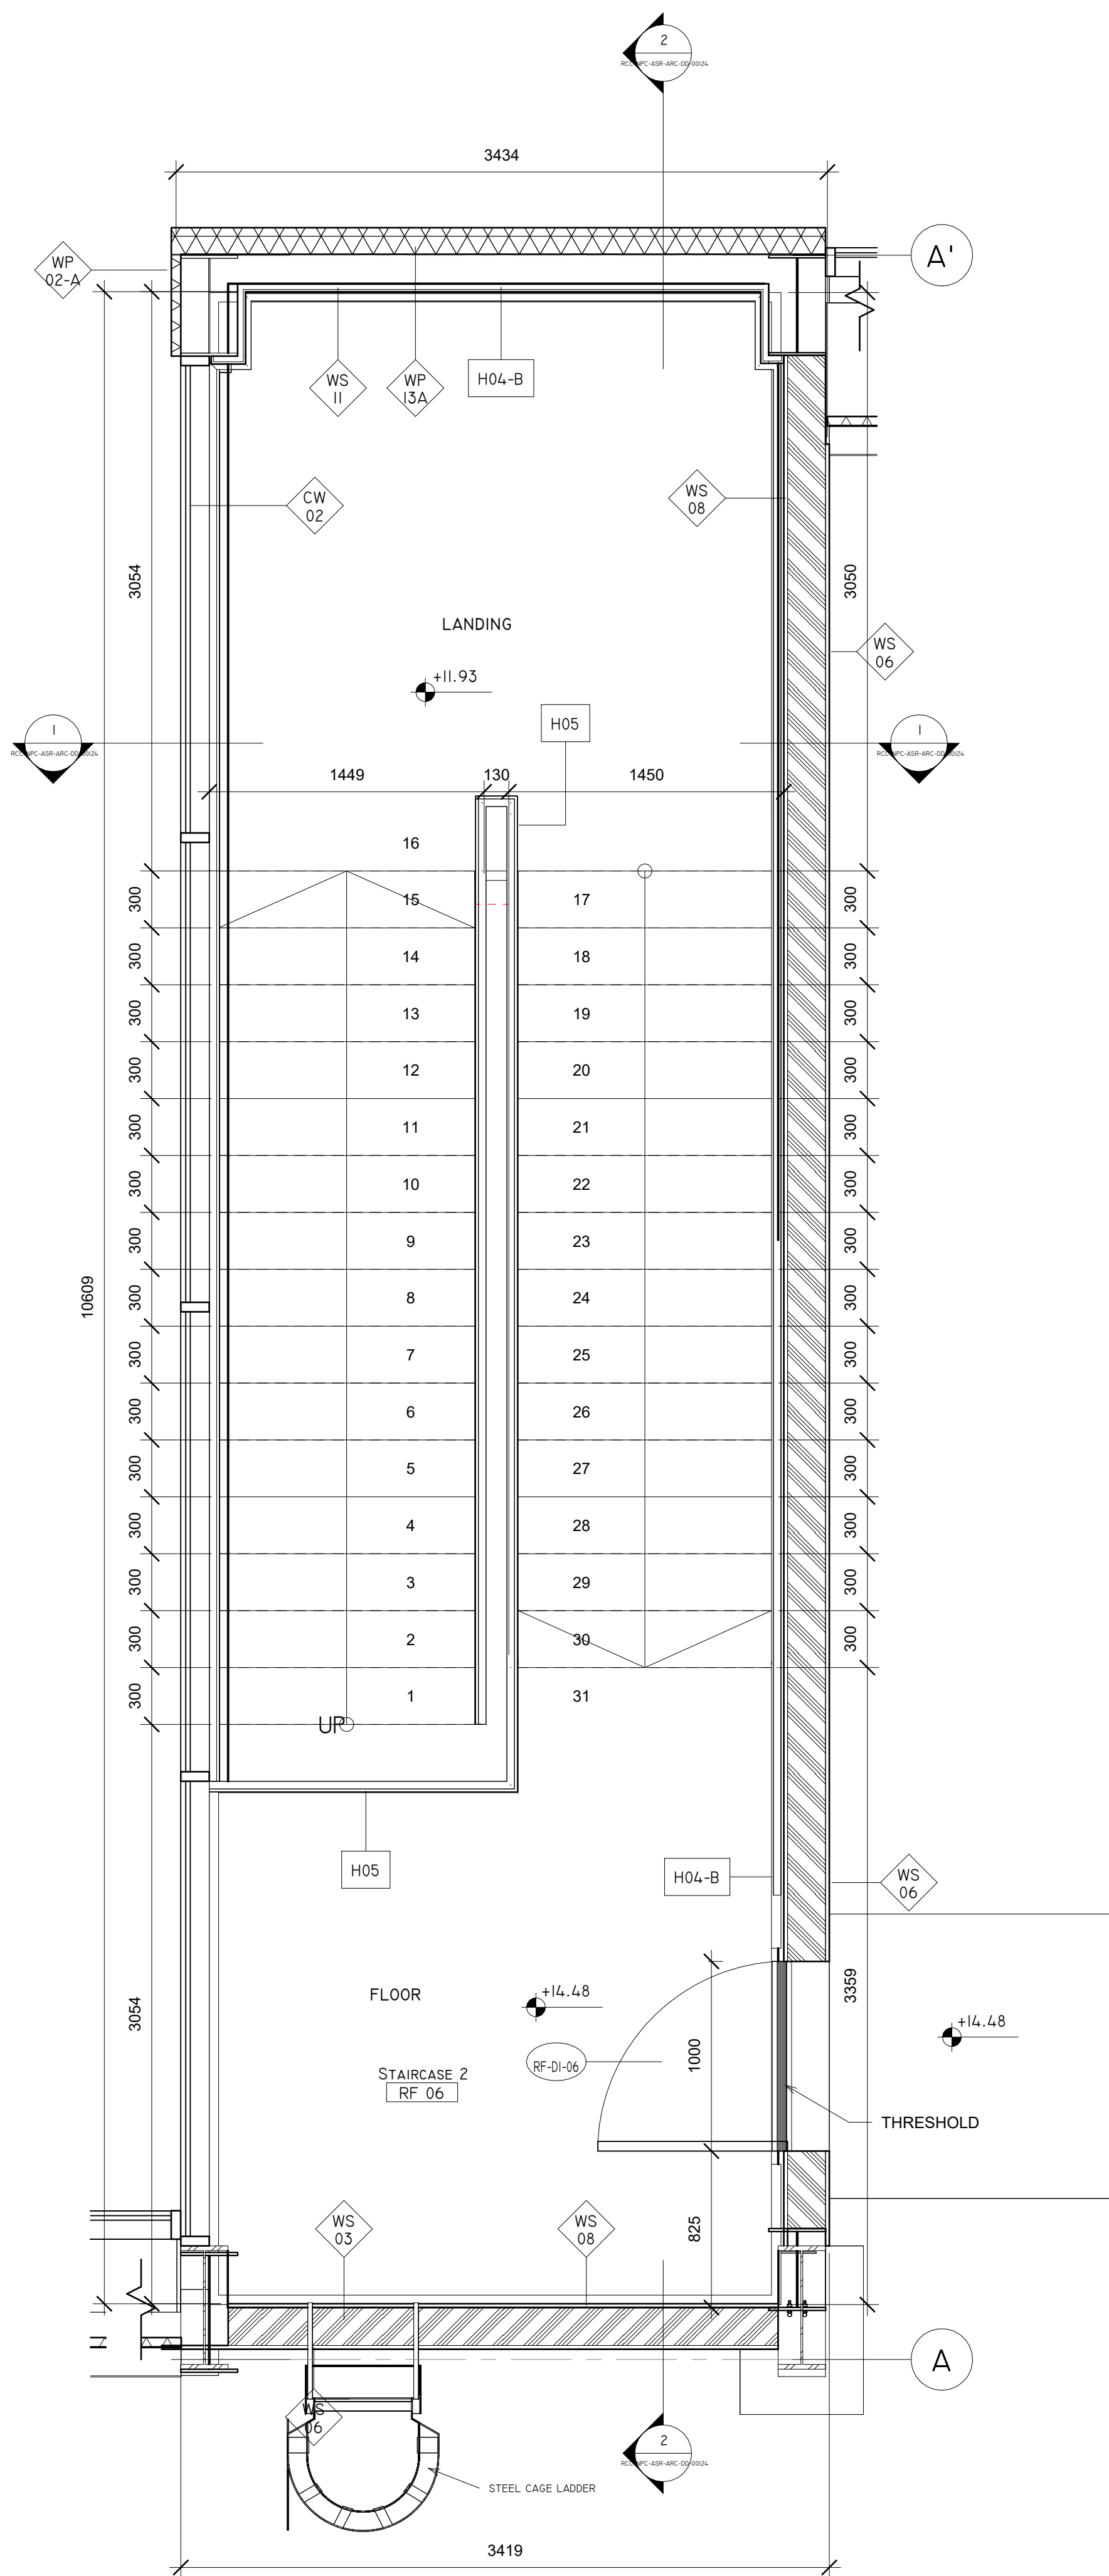

04 ROOF FLOOR PLAN (STAIRCASE -2)
1 : 25

HANDRAIL LEGEND

REF	DESCRIPTION
H01	1000MM GALVANIZED STEEL HANDRAIL - EPOXY PAINTED
H02	1000MM STAINLESS STEEL HANDRAIL
H03	1000MM STAINLESS STEEL HANDRAIL WITH GLASS
H04	1000MM STAINLESS STEEL HANDRAIL WALL MOUNTED
H05	1000MM GALVANIZED STEEL HANDRAIL WALL MOUNTED
H06	1000MM GALVANIZED STEEL HANDRAIL POWDER COATED
H07	1000MM GALVANIZED STEEL HANDRAIL POWDER COATED

NOTES & LEGENDS:


1. ALL DIMENSIONS ARE IN MILLIMETERS AND ALL LEVELS GIVEN IN METERS UNLESS OTHERWISE NOTED.
2. FINISHED FLOOR AND ELEVATION: F.F.L. +0.00 METERS SHOWN IN THIS DRAWING IS EQUIVALENT TO F.F.L. +0.00 M AS REFERENCED TO SITE GRADING LAYOUT DWG NO. RCC-NPC-ASR-CIV-DD-0001.
3. THIS DRAWING SHALL BE READ IN CONJUNCTION WITH THE MECHANICAL, ELECTRICAL, MECHANICAL, TELECOM AND STRUCTURAL DRAWINGS.
4. CONTRACTOR SHALL BE RESPONSIBLE FOR OBTAINING ALL NECESSARY PERMITS PRIOR TO THE START OF CONSTRUCTION. ANY DISCREPANCY SHOULD BE BROUGHT TO THE ATTENTION OF THE CLIENT FOR CLARIFICATION BEFORE PROCEEDING WITH THE AFFECTED PART OF WORK.

0	COLUMN GRID	XX	SPOT ELEVATION
05	FURNITURE TAG	YY A ZZ	ROOM NAME & NUMBER
06	DOOR TAGS	R0 M2	WALL FINISH TYPE
07		00	

WALLS LEGEND

TYPE	DESCRIPTION
CW 02	GLAZED CURTAIN WALL PANELS
CW 03	SPANDREL PANELS
CW 04	FRAMELESS GLASS PARTITION
LV 01	CURTAIN LOUVER PARTITION
WP 02	EXTERIOR WALL PANEL SYSTEM 100MM THICK - COLOR WHITE
WP 03	EXTERIOR WALL PANEL SYSTEM 100MM THICK - COLOR WHITE
WP 04	INTERIOR WALL PANEL SYSTEM 100MM THICK - 1HR FIRE RATED
WP 05	WALL PANEL SYSTEM 100MM THICK FOR STAGING AREA
WP 06	WALL PANEL SYSTEM 100MM THICK FOR STAGING AREA
WP 07	UN-INSULATED WALL PANEL SYSTEM 100MM THICK
WP 08	SOLID POLYMER FABRICATION RESIN TOILET COMPARTMENTS
WP 09	SOLID POLYMER FABRICATION RESIN TOILET COMPARTMENTS
WP 10	ACP CLADDING 4MM THICK
WP 11	EXTERIOR WALL PANEL SYSTEM 100MM THICK - COLOR WHITE
WP 12	EXTERIOR WALL PANEL SYSTEM 100MM THICK - COLOR WHITE
WP 13	COMPOSITE PANEL CLADDING 20MM THICK
WP 14	WALL PANEL SYSTEM 100MM THICK FOR CHILLED & FREEZER ROOMS
WP 15	GREEN WALL
WP 16	EXTERIOR WALL PANEL SYSTEM 100MM THICK - COLOR WHITE
WP 17	EXTERIOR WALL PANEL SYSTEM 100MM THICK - COLOR WHITE
WP 18	CONCRETE MASONRY UNIT WALL (UNIT: 400X200; 100MM THICK)
WP 19	CONCRETE MASONRY UNIT WALL (UNIT: 400X200; 100MM THICK)
KEY PLAN :

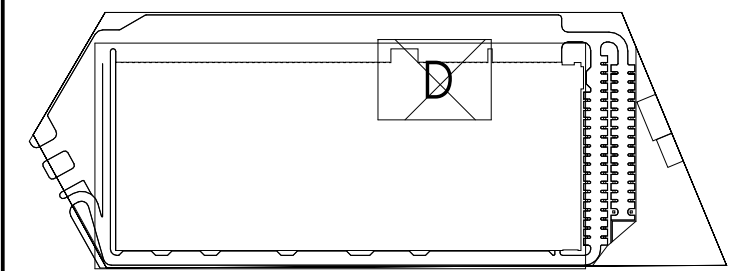

REV.	DATE	DESCRIPTION OF REVISION
00	11/08/2025	ISSUE FOR DETAILED DESIGN
01	03/09/2025	ISSUE FOR DETAILED DESIGN
02	20/10/2025	ISSUE FOR DETAILED DESIGN

SEAL & SIGNATURE:

DRAWN BY	CHECKED BY	DATE (DD.MM.YYYY)
AMM	ZYD	03/07/2025

NUPCO WAREHOUSE ASER, KSA

CLIENT:



PROJECT MANAGER:



PROJECT PROGRAM MANAGER:



ARCHITECTURE & ENGINEERING CONSULTANT:



PHASE & DISCIPLINE:

DETAIL DESIGN
ARCHITECTURE

DRAWING TITLE:

STAIRCASE 2 - PLANS

PROJECT NO.	DRAWING NUMBER	REV
102	RCC-NPC-ASR-ARC-DD-00123	02
SCALE (A0)	AS INDICATED	



PLOT DATE & TIME: 03/07/2025 12:02:52 PM FILE: D:\BACX\JPNPC-RCC-30N-BTN-ASR-WRH-001-LANDS-WAREHOUSE-INT