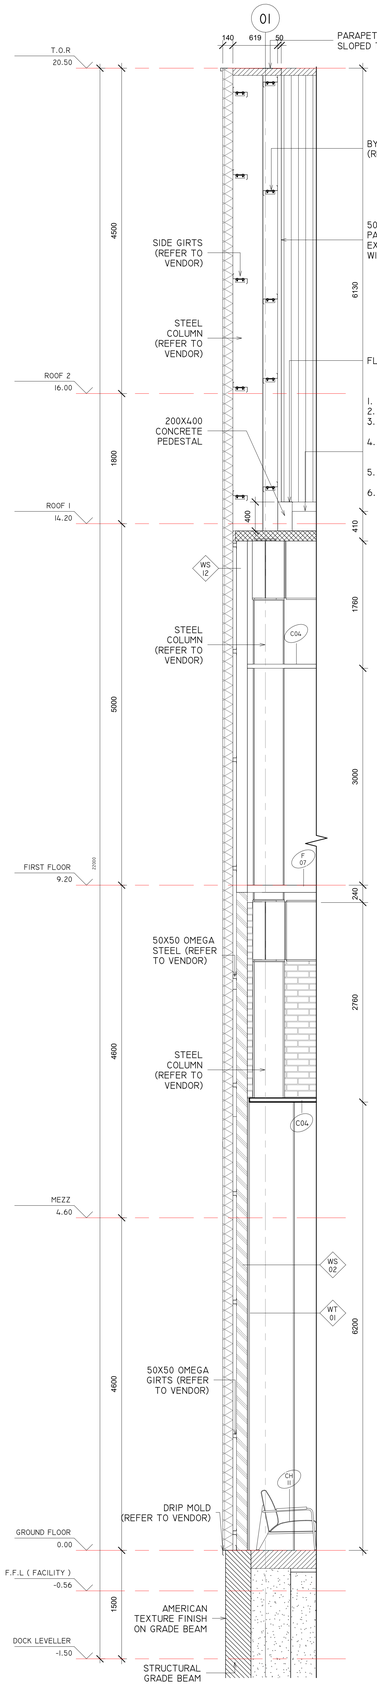

1 WALL SECTION 1
1 : 30

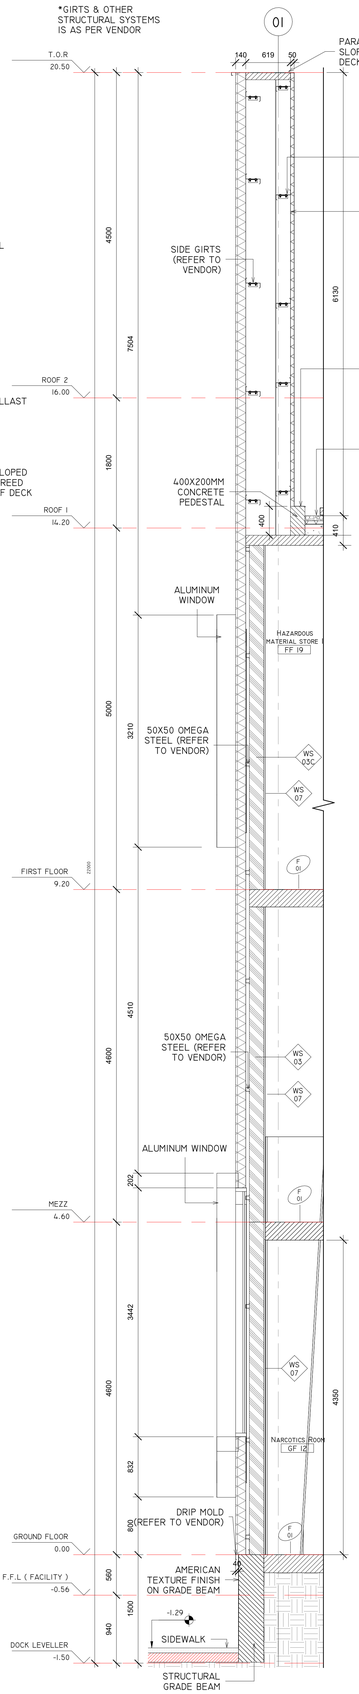

2 WALL SECTION 2
1 : 30

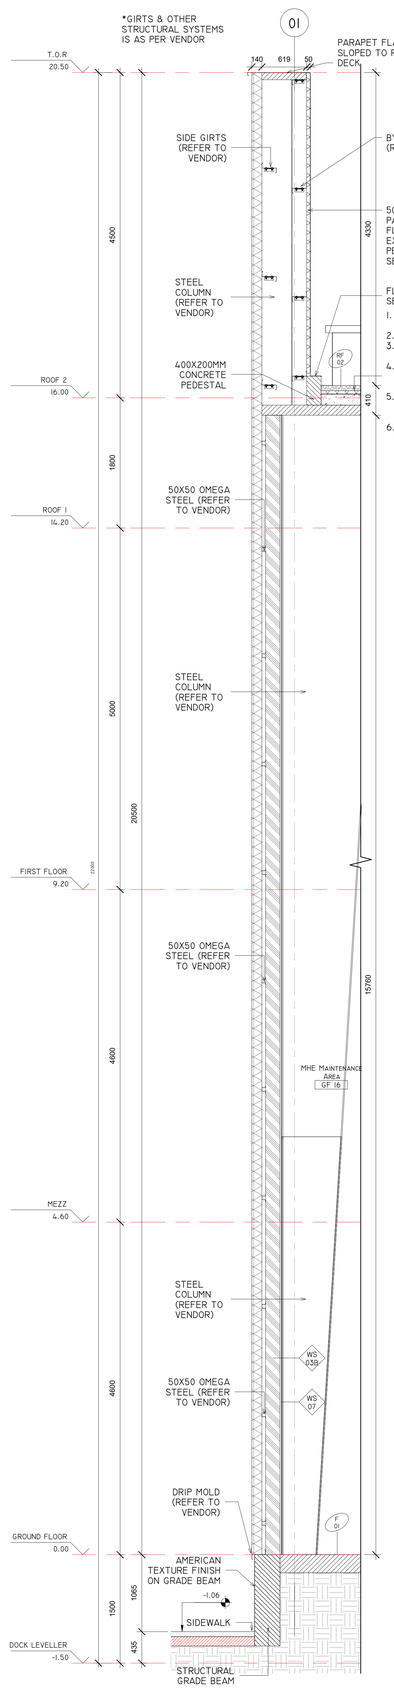

3 WALL SECTION 3
1 : 30

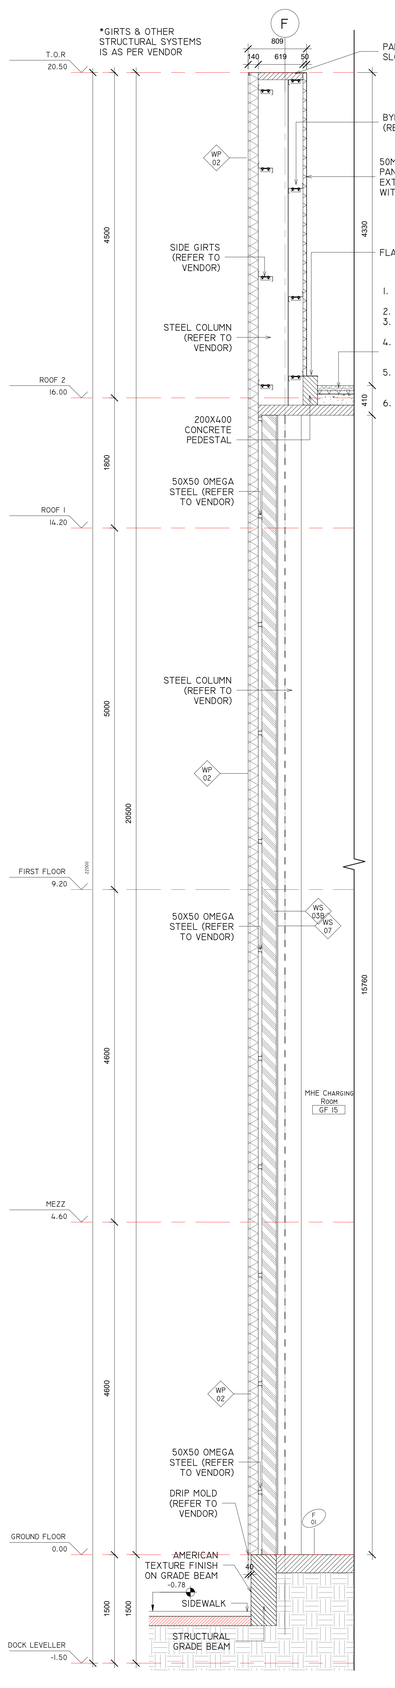

4 WALL SECTION 4
1 : 30

WALLS LEGEND

TYPE	Description
CW 02	GLAZED CURTAIN WALL PANELS
CW 03	SPANDREL PANELS
CW 04	FRAMELESS GLASS PARTITION
LV 01	CURTAIN LOUVER PARTITION
WI	COMPOSITE PANEL CLADDING
WP 02	EXTERIOR WALL PANEL SYSTEM 140MM THICK - COLOR WHITE
WP 02-A	EXTERIOR WALL PANEL SYSTEM 140MM THICK - COLOR WHITE
WP 02-B	EXTERIOR WALL PANEL SYSTEM 140MM THICK - COLOR WHITE 2-HRS FIRE RATED
WP 02A	EXTERIOR WALL PANEL SYSTEM 140MM THICK - COLOR WHITE 2-HRS FIRE RATED
WP 04B	INTERIOR WALL PANEL SYSTEM 150MM THICK 2-HR FIRE RATED
WP 05	WALL PANEL SYSTEM 100MM THICK FOR STAGING AREA
WP 05B	WALL PANEL SYSTEM 100MM THICK FOR STAGING AREA 30-MIN FIRE RATED
WP 06	WALL PANEL SYSTEM 150MM THICK FOR STAGING AREA
WP 06B	WALL PANEL SYSTEM 150MM THICK FOR STAGING AREA 2-HRS FIR RATED
WP 06C	WALL PANEL SYSTEM 150MM THICK FOR STAGING AREA 30-MIN FIR RATED
WP 07	UN-INSULATED WALL PANEL SYSTEM 50MM THICK
WP 08	SOLID POLYMER FABRICATION RESIN TOILET COMPARTMENTS
WP 08A	SOLID POLYMER FABRICATION RESIN TOILET COMPARTMENTS 13MM
WP 08B	SOLID POLYMER FABRICATION RESIN TOILET COMPARTMENTS
WP 10	ACP CLADDING 4MM THICK
WP 13	EXTERIOR WALL PANEL SYSTEM 140MM THICK - COLOR WHITE
WP 13A	EXTERIOR WALL PANEL SYSTEM 140MM THICK - COLOR WHITE FIRE RATED 2HR
WP 14	COMPOSITE PANEL CLADDING 20MM THICK
WP 15	<VARIES>
WP 16	GREEN WALL
WP 17	EXTERIOR WALL PANEL SYSTEM 150MM THICK - COLOR WHITE
WP 18	DECORATIVE WOOD WALL PANELS
WS 01	CONCRETE MASONRY UNIT WALL (UNIT: 400X200; 100MM THICK)
WS 02	CONCRETE MASONRY UNIT WALL (UNIT: 400X200; 150MM THICK)
WS 02A	CONCRETE MASONRY UNIT WALL 1-HRS FIRE RATED (UNIT: 400X200; 150MM THICK)
WS 02B	CONCRETE MASONRY UNIT WALL 2-HRS FIRE RATED (UNIT: 400X200; 150MM THICK)
WS 03	CONCRETE MASONRY UNIT WALL (UNIT: 400X200; 200MM THICK)
WS 03A	CONCRETE MASONRY UNIT WALL 1-HR FIRE RATED (UNIT: 400X200; 200MM THICK)
WS 03B	CONCRETE MASONRY UNIT WALL 2-HRS FIRE RATED (UNIT: 400X200; 200MM THICK)
WS 03C	CONCRETE MASONRY UNIT WALL 3-HRS FIRE RATED (UNIT: 400X200; 200MM THICK)
WS 04	CONCRETE MASONRY UNIT WALL (UNIT: 400X200; 100MM THICK) + 50MM AIR SPACE & 30MM INSULATION + CONCRETE MASONRY UNIT WALL (UNIT: 400X200; 100MM THICK)
WS 04A	CONCRETE MASONRY UNIT WALL 1-HRS FIRE RATED (UNIT: 400X200; 100MM THICK) + 50MM AIR SPACE & 30MM INSULATION + CONCRETE MASONRY UNIT WALL (UNIT: 400X200; 100MM THICK)
WS 04B	CONCRETE MASONRY UNIT WALL 2-HRS FIRE RATED (UNIT: 400X200; 100MM THICK) + 50MM AIR SPACE & 30MM INSULATION + CONCRETE MASONRY UNIT WALL (UNIT: 400X200; 100MM THICK)
WS 05	CONCRETE MASONRY UNIT WALL (UNIT: 400X200; 150MM THICK) + 50MM AIR SPACE & 30MM INSULATION + SOLID CONCRETE MASONRY UNIT WALL (UNIT: 400X200; 150MM THICK)
WS 05A	CONCRETE MASONRY UNIT WALL 1-HRS FIRE RATED (UNIT: 400X200; 150MM THICK) + 50MM AIR SPACE & 30MM INSULATION + SOLID CONCRETE MASONRY UNIT WALL (UNIT: 400X200; 150MM THICK)
WS 06	20MM THICK SAND CEMENT PLASTER TO EXTERNAL WALLS INCLUDING EXTERNAL PAINT
WS 07	20MM THICK SAND CEMENT PLASTER TO INTERNAL WALLS WITH WASHABLE OIL PAINT
WS 08	20MM THICK SAND CEMENT PLASTER TO INTERNAL WALLS INCLUDING EMULSION PAINT
WS 09	120MM THICK INSULATED TWO LAYERS OF GYPSUM BOARD FROM EACH SIDE - WALL PARTITIONS
WS 10	2HRS FIRE RATED GYPSUM WALL - 2 LAYERS OF FIRE RATED GYPSUM FROM BOTH SIDES 12.5MM THICK FOR EACH LAYER INCLUDING ROCKWOOL INSULATION
WS 10A	1HRS FIRE RATED GYPSUM WALL - 2 LAYERS OF FIRE RATED GYPSUM FROM BOTH SIDES 12.5MM THICK FOR EACH LAYER INCLUDING ROCKWOOL INSULATION
WS 11	12MM THICK INSULATED GYPSUM DRYWALL CLADDING
WS 11A	12MM THICK INSULATED MOISTURE RESISTANT GYPSUM DRYWALL CLADDING
WS 12	12MM THICK INSULATED GYPSUM DRYWALL CLADDING
WS 13	150MM THICK INSULATED CEMENT BOARD WALL PARTITIONS ABOVE CURTAIN WALLS INCLUDING STEEL STRUCTURE & ROCK WOOL INSULATION
WS 14	12MM THICK INSULATED GYPSUM BOARD WALL PANELS
WT 01	PAINTING FINISHING

FLOOR LEGEND

REF	DESCRIPTION
F 01	HIGH PERFORMANCE EPOXY COATING
F 02	HIGH PERFORMANCE EPOXY COATING - COLOR YELLOW
F 03	PORCELAIN TILE: 30X20CM NON-SLIP - SLIP RESISTANCE R9- WAREHOUSE WET AREAS
F 04	PORCELAIN TILE: 60X60CM WAREHOUSE COMMON AREAS
F 05	PORCELAIN TILE: 60X60CM - FIRST FLOOR OFFICES & COMMON AREAS
F 06	FAIR-FACED CONCRETE
F 07	50X50CM CARPET TILES - COLOR GREY - GLUE FIXED ON TERRAZZO TILES
F 07.1	PRAYER ROOM CARPET ON TOP OF TILES
F 11	HIGH PERFORMANCE EPOXY COATING
F 12	SIDEWALK TILE
L 01	GROUND COVERS & GRASSES
RF 01	INVERTED WATERPROOFING - AVERAGE THICKNESS 100MM
RF 02	INVERTED WATERPROOFING - AVERAGE THICKNESS 150MM

CEILING LEGEND

REF	DESCRIPTION
C01	FIBER GYPSUM CEILING 600x600 MM
C02	PERFORATED METAL CEILING- 600X600MM GRID- MOISTURE RESISTANT
C03	FIBER GYPSUM CEILING 600X200 MM
C04	PAINTED GYPSUM BOARD SUSPENDED CEILING
C05	INSULATED ROOF SANDWICH PANEL- 150MM THICK
C06	COLD ROOM INSULATED PANELS - 200MM THICK
C07	BAFFLE CEILING

NOTES & LEGENDS:

1. ALL DIMENSIONS ARE IN MILLIMETERS AND ALL LEVELS GIVEN IN METERS UNLESS OTHERWISE NOTED.
2. FINISHED FLOOR AND ELEVATION - F.F.L.+0.00 METERS SHOWN IN THIS DRAWING IS EQUIVALENT TO FFL. 2129.50M AS REFERENCED TO SITE GRADING LAYOUT DWG NO. RCC-NPC-ASR-CIV-DD-00005.
3. THIS DRAWING SHALL BE READ IN CONJUNCTION WITH RELEVANT ELECTRICAL, MECHANICAL, TELECOM AND STRUCTURAL DRAWINGS.
4. CONTRACTOR TO VERIFY ALL DIMENSIONS AND CONDITION AT SITE PRIOR TO THE START OF CONSTRUCTION. ANY DISCREPANCY SHOULD BE SHALL BE BROUGHT TO THE ATTENTION OF THE CLIENT FOR CLARIFICATION BEFORE PROCEEDING WITH THE AFFECTED PART OF WORK.
5. FINAL RACKING POSITIONS TO BE PROVIDED BY VENDOR.
6. APPROVED FURNITURES TO BE PROVIDED BY AL RAMSAT.

0 COLUMN GRID — SPOT ELEVATION
F 06 furniture TAG — XX YY A ZZ ROOM NAME & NUMBER
X FLOOR NAME DOOR TAGS — 150 M2 00 WALL-FINISH TYPE

KEY PLAN :

REV	DATE DD.MM.YY	DESCRIPTION OF REVISION
00	05/08/2025	ISSUE FOR DETAILED DESIGN
01	29/10/2025	ISSUE FOR DETAILED DESIGN

SEAL & SIGNATURE:

DRAWN BY	CHECKED BY	DATE (DD.MM.YYYY)
AHM	ALN	03/07/2025

NUPCO WAREHOUSE
ASEER, KSA

CLIENT:

PROJECT MANAGER:

PROJECT PROGRAM MANAGER

ARCHITECTURE & ENGINEERING CONSULTANT:

PHASE & DISCIPLINE:

DETAIL DESIGN
ARCHITECTURE

DRAWING TITLE:

WALL SECTIONS 1/4

PROJECT NO:	DRAWING NUMBER	REV
102	RCC-NPC-ASR-ARC-DD-00143	01
SCALE (A0) AS INDICATED		