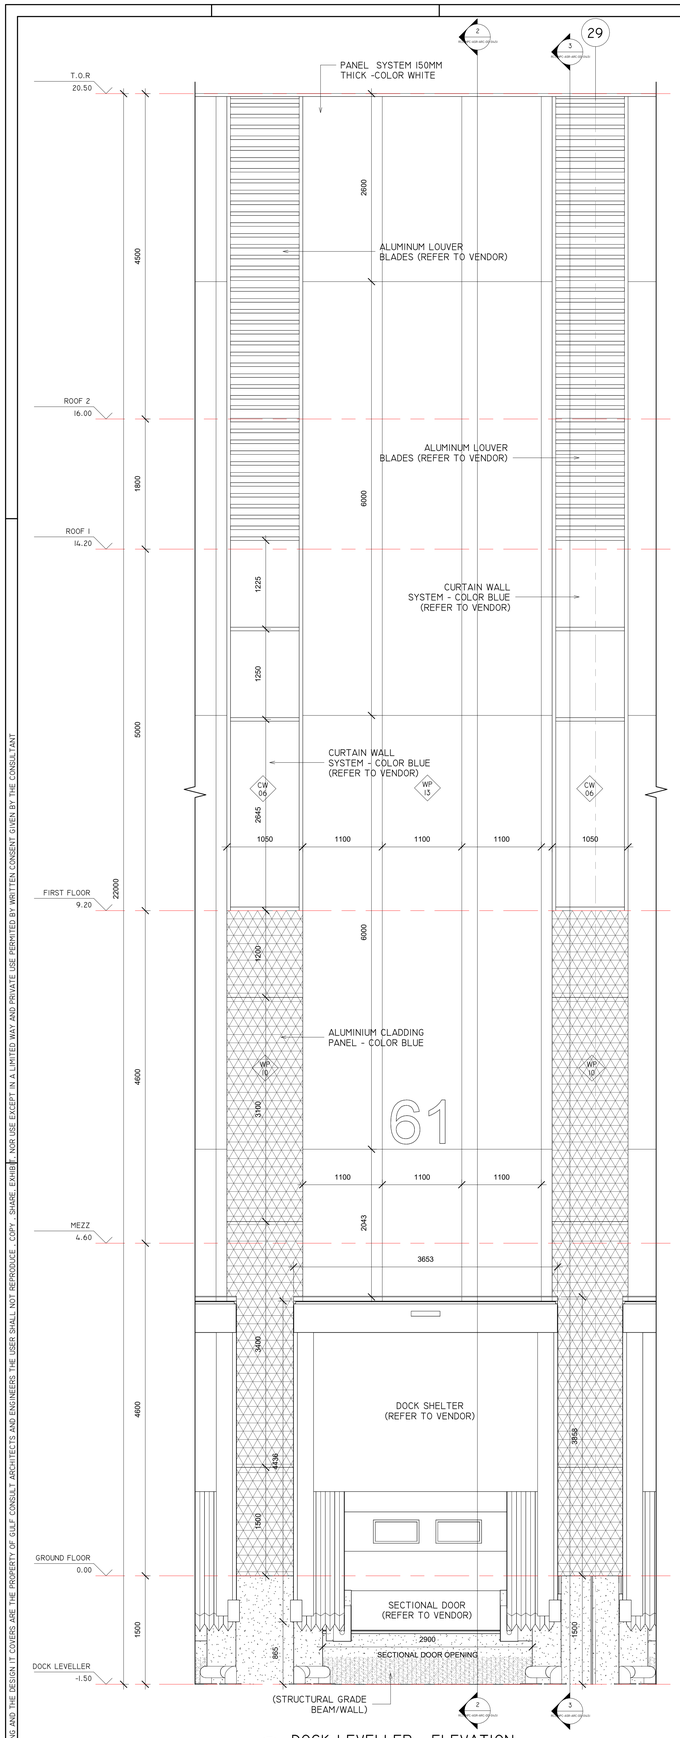

1 DOCK LEVELLER - ELEVATION
1 : 30

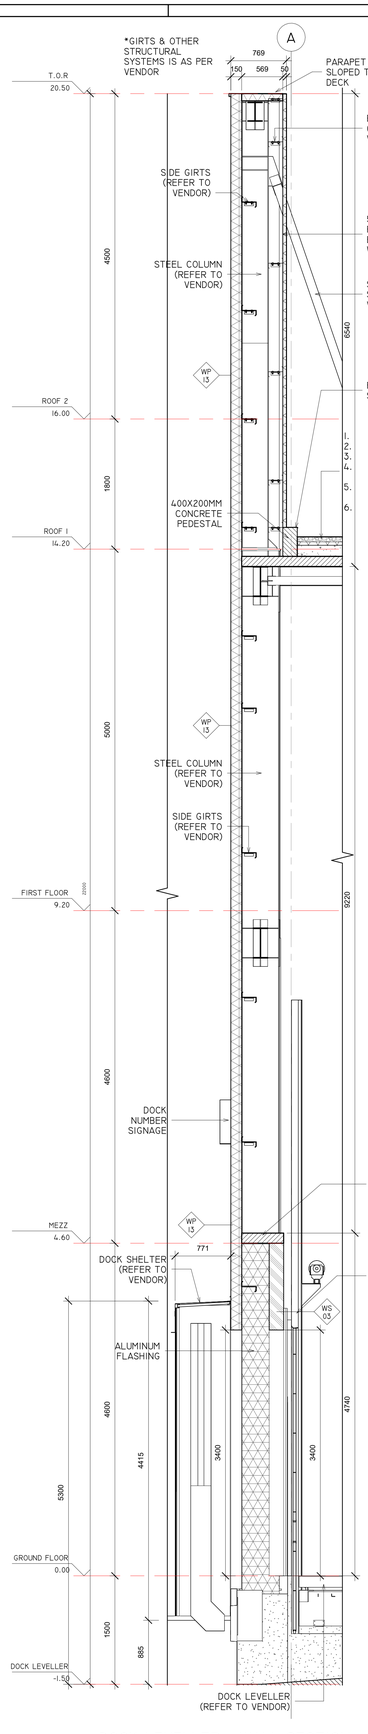

2 DOCK LEVELLER - WALL SECTION
1 : 30

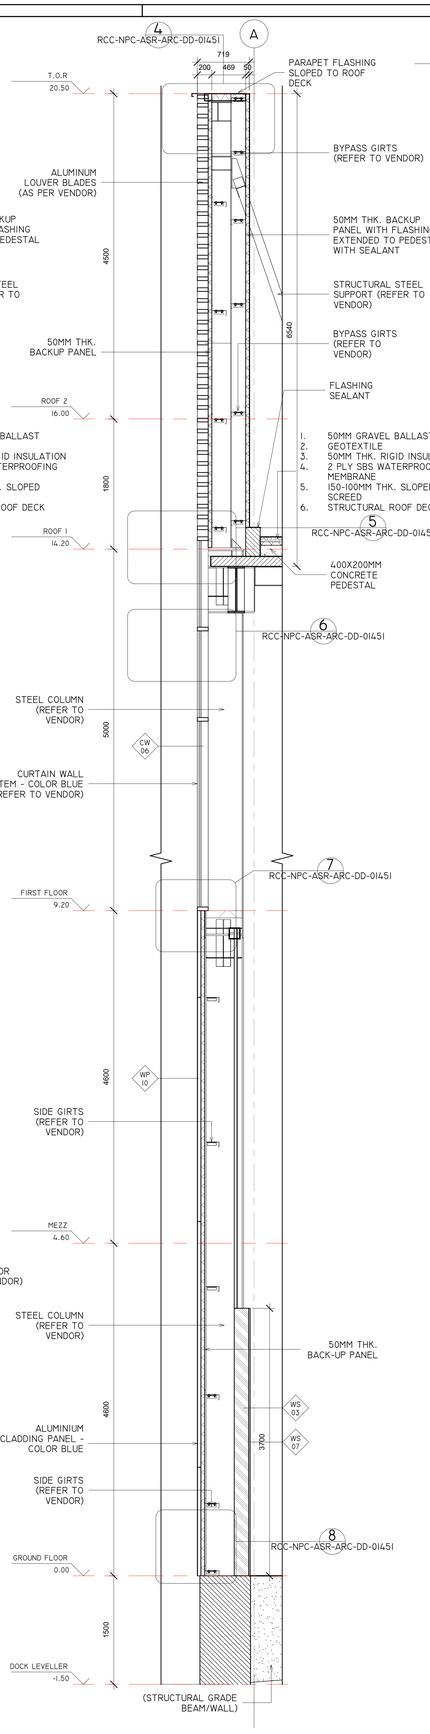

3 ALUM. PANEL & CURTAIN WALL - WALL SECTION
1 : 30

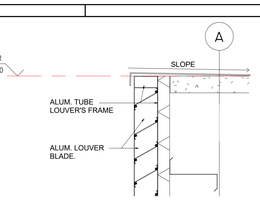

4 FLASHING DETAILS AT PARAPET
1 : 15

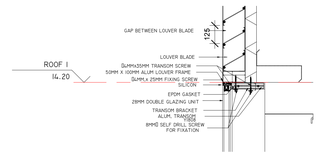

5 LOUVER TO CURTAIN WALL DETAILS
1 : 15

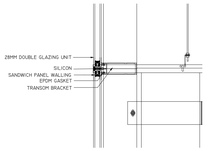

6 CURTAIN WALL CONNECTION
1 : 15

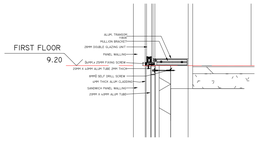

7 CURTAIN WALL CONNECTION ON SLAB DETAILS
1 : 15

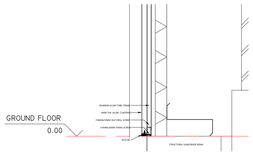

8 CURTAIN WALL TO RETAINING WALL
1 : 15

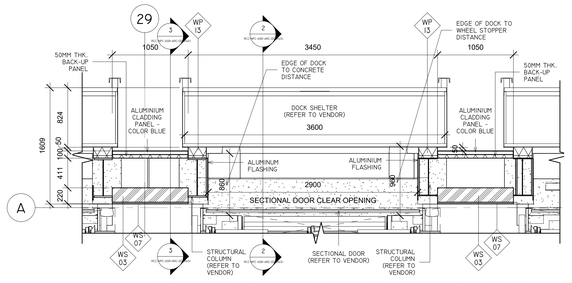

10 GROUND FLOOR DOCK LEVELER - ENLARGED PLAN
1 : 30

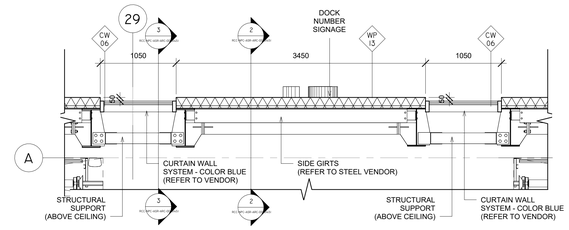

11 FIRST FLOOR CLADDING - ENLARGED PLAN
1 : 30

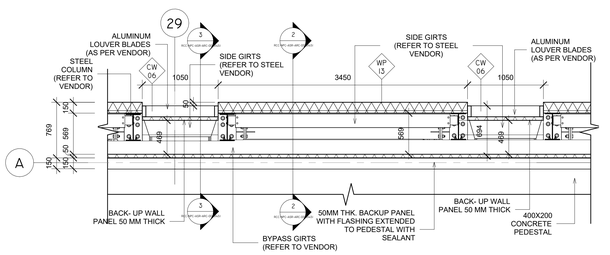

12 ROOF CLADDING - ENLARGED PLAN
1 : 30

NOTES & LEGENDS:

1. ALL DIMENSIONS ARE IN MILLIMETERS AND ALL LEVELS GIVEN IN METERS UNLESS OTHERWISE NOTED.
2. FINISHED FLOOR AND ELEVATION - F.F.L.+0.00 METERS SHOWN IN THIS DRAWING IS EQUIVALENT TO FFL. 2129.50M AS REFERENCED TO SITE GRADING LAYOUT DWG NO. RCC-NPC-ASR-CIV-DD-00005.
3. THIS DRAWING SHALL BE READ IN CONJUNCTION WITH RELEVANT ELECTRICAL, MECHANICAL, TELECOM AND STRUCTURAL DRAWINGS.
4. CONTRACTOR TO VERIFY ALL DIMENSIONS AND CONDITION AT SITE PRIOR TO THE START OF CONSTRUCTION. ANY DISCREPANCY SHOULD BE SHALL BE BROUGHT TO THE ATTENTION OF THE CLIENT FOR CLARIFICATION BEFORE PROCEEDING WITH THE AFFECTED PART OF WORK.
5. FINAL RACKING POSITIONS TO BE PROVIDED BY VENDOR.
6. APPROVED FURNITURES TO BE PROVIDED BY AL RAMSAT.
7. ALL VENDOR DETAILS WILL BE UPDATED IN THE SHOP DRAWINGS
8. STRUCTURAL ELEMENTS SIZES AND SPACING IS AS PER VENDOR

0 COLUMN GRID — SPOT ELEVATION

F 00 FURNITURE TAG — XX YY & ZZ ROOM NAME & NUMBER

150 M2

X YY & ZZ DOOR TAGS — 00 WALL/FINISH TYPE

WALLS LEGEND

TYPE	DESCRIPTION
CW 01	GLAZED CURTAIN WALL PANELS
CW 02	ALUMINUM & GLASS PARTITION
LV 01	CURTAIN LOUVER PARTITION
LV 02	CURTAIN LOUVER PARTITION
WI1	COMPOSITE PANEL CLADDING
WP 02	EXTERIOR WALL PANEL SYSTEM 150MM THICK - COLOR WHITE
WP 03	EXTERIOR WALL PANEL SYSTEM 150MM THICK - COLOR BLUE
WP 04A	INTERIOR WALL PANEL SYSTEM 150MM THICK 1-HR FIRE RATED
WP 05	WALL PANEL SYSTEM 150MM THICK FOR STAGING AREA
WP 06	WALL PANEL SYSTEM 150MM THICK FOR STAGING AREA
WP 07	UN-INSULATED WALL PANEL SYSTEM 50MM THICK
WP 08	SOLID POLYMER FABRICATION RESIN TOILET COMPARTMENTS
WP 08A	SOLID POLYMER FABRICATION RESIN TOILET COMPARTMENTS 15MM
WP 08B	SOLID POLYMER FABRICATION RESIN TOILET COMPARTMENTS
WP 10	ACP CLADDING 4MM THICK
WP 13	EXTERIOR WALL PANEL SYSTEM 150MM THICK - COLOR WHITE
WP 14	COMPOSITE PANEL CLADDING 25MM THICK
WP 15	WALL PANEL SYSTEM 150MM THICK FOR CHILLED & FREEZER ROOMS
WP 16	GREEN WALL
WP 17	EXTERIOR WALL PANEL SYSTEM 150MM THICK - COLOR WHITE
WS 01	CONCRETE MASONRY UNIT WALL (UNIT: 400X200; 100MM THICK)
WS 02	CONCRETE MASONRY UNIT WALL (UNIT: 400X200; 150MM THICK)
WS 03	CONCRETE MASONRY UNIT WALL (UNIT: 400X200; 200MM THICK)
WS 03A	CONCRETE MASONRY UNIT WALL 1-HR FIRE RATED (UNIT: 400X200; 200MM THICK)
WS 03B	CONCRETE MASONRY UNIT WALL 2-HRS FIRE RATED (UNIT: 400X200; 200MM THICK)
WS 04	CONCRETE MASONRY UNIT WALL (UNIT: 400X200; 100MM THICK) + 50MM AIR SPACE & 30MM INSULATION + CONCRETE MASONRY UNIT WALL (UNIT: 400X200; 100MM THICK)
WS 05	CONCRETE MASONRY UNIT WALL (UNIT: 400X200; 150MM THICK) + 50MM AIR SPACE & 30MM INSULATION + SOLID CONCRETE MASONRY UNIT WALL (UNIT: 400X200; 150MM THICK)
WS 06	20MM THICK SAND CEMENT PLASTER TO EXTERNAL WALLS INCLUDING EXTERNAL PAINT
WS 07	20MM THICK SAND CEMENT PLASTER TO INTERNAL WALLS WITH WASHABLE OIL PAINT
WS 08	20MM THICK SAND CEMENT PLASTER TO INTERNAL WALLS INCLUDING EMULSION PAINT
WS 09	120MM THICK INSULATED TWO LAYERS OF GYPSUM BOARD FROM EACH SIDE - WALL PARTITIONS
WS 10	2HRS FIRE RATED GYPSUM WALL - 2 LAYERS OF FIRE RATED GYPSUM FROM BOTH SIDES (2.5MM THICK FOR EACH LAYER INCLUDING ROCKWOOL INSULATION
WS 11	12MM THICK INSULATED GYPSUM DRYWALL CLADDING
WS 12	12MM THICK INSULATED GYPSUM DRYWALL CLADDING
WS 13	150MM THICK INSULATED CEMENT BOARD WALL PARTITIONS ABOVE CURTAIN WALLS INCLUDING STEEL STRUCTURE & ROCK WOOL INSULATION
WS 14	12MM THICK INSULATED GYPSUM BOARD WALL PANELS
WT 01	PAINTING FINISHING

KEY PLAN :

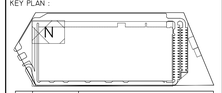

REV.	DATE DD.MM.YY	DESCRIPTION OF REVISION
00	02/10/2025	ISSUE FOR DETAILED DESIGN

SEAL & SIGNATURE:

DRAWN BY	CHECKED BY	DATE (DD.MM.YYYY)
AHM	ALN	29/09/2025

NUPCO WAREHOUSE
ASEER, KSA

CLIENT:

PROJECT MANAGER:

PROJECT PROGRAM MANAGER

شركة الرامسات للمقاولات
Al Ramsat contracting company

ARCHITECTURE & ENGINEERING CONSULTANT:

PHASE & DISCIPLINE:

DETAIL DESIGN
ARCHITECTURE

DRAWING TITLE:

WALL SECTIONS 4/4

PROJECT NO.	DRAWING NUMBER	REV
102	RCC-NPC-ASR-ARC-DD-01451	00
SCALE (A0)		
AS INDICATED		

THIS DRAWING AND THE DESIGN IT COVERS ARE THE PROPERTY OF GULF CONSULT ARCHITECTS AND ENGINEERS. THE USER SHALL NOT REPRODUCE , COPY , SHARE , EXHIBIT , NOR USE EXCEPT IN A LIMITED WAY AND PRIVATE USE PERMITED BY WRITTEN CONSENT GIVEN BY THE CONSULTANT

PLOT DATE & TIME: 02/10/2025, 1:55:53 PM FILE: C:\USERS\MSI\DOCUMENTS\NPC-ARCC-3DM-BIM-ARC-WRM-0001_ALN.RVT