


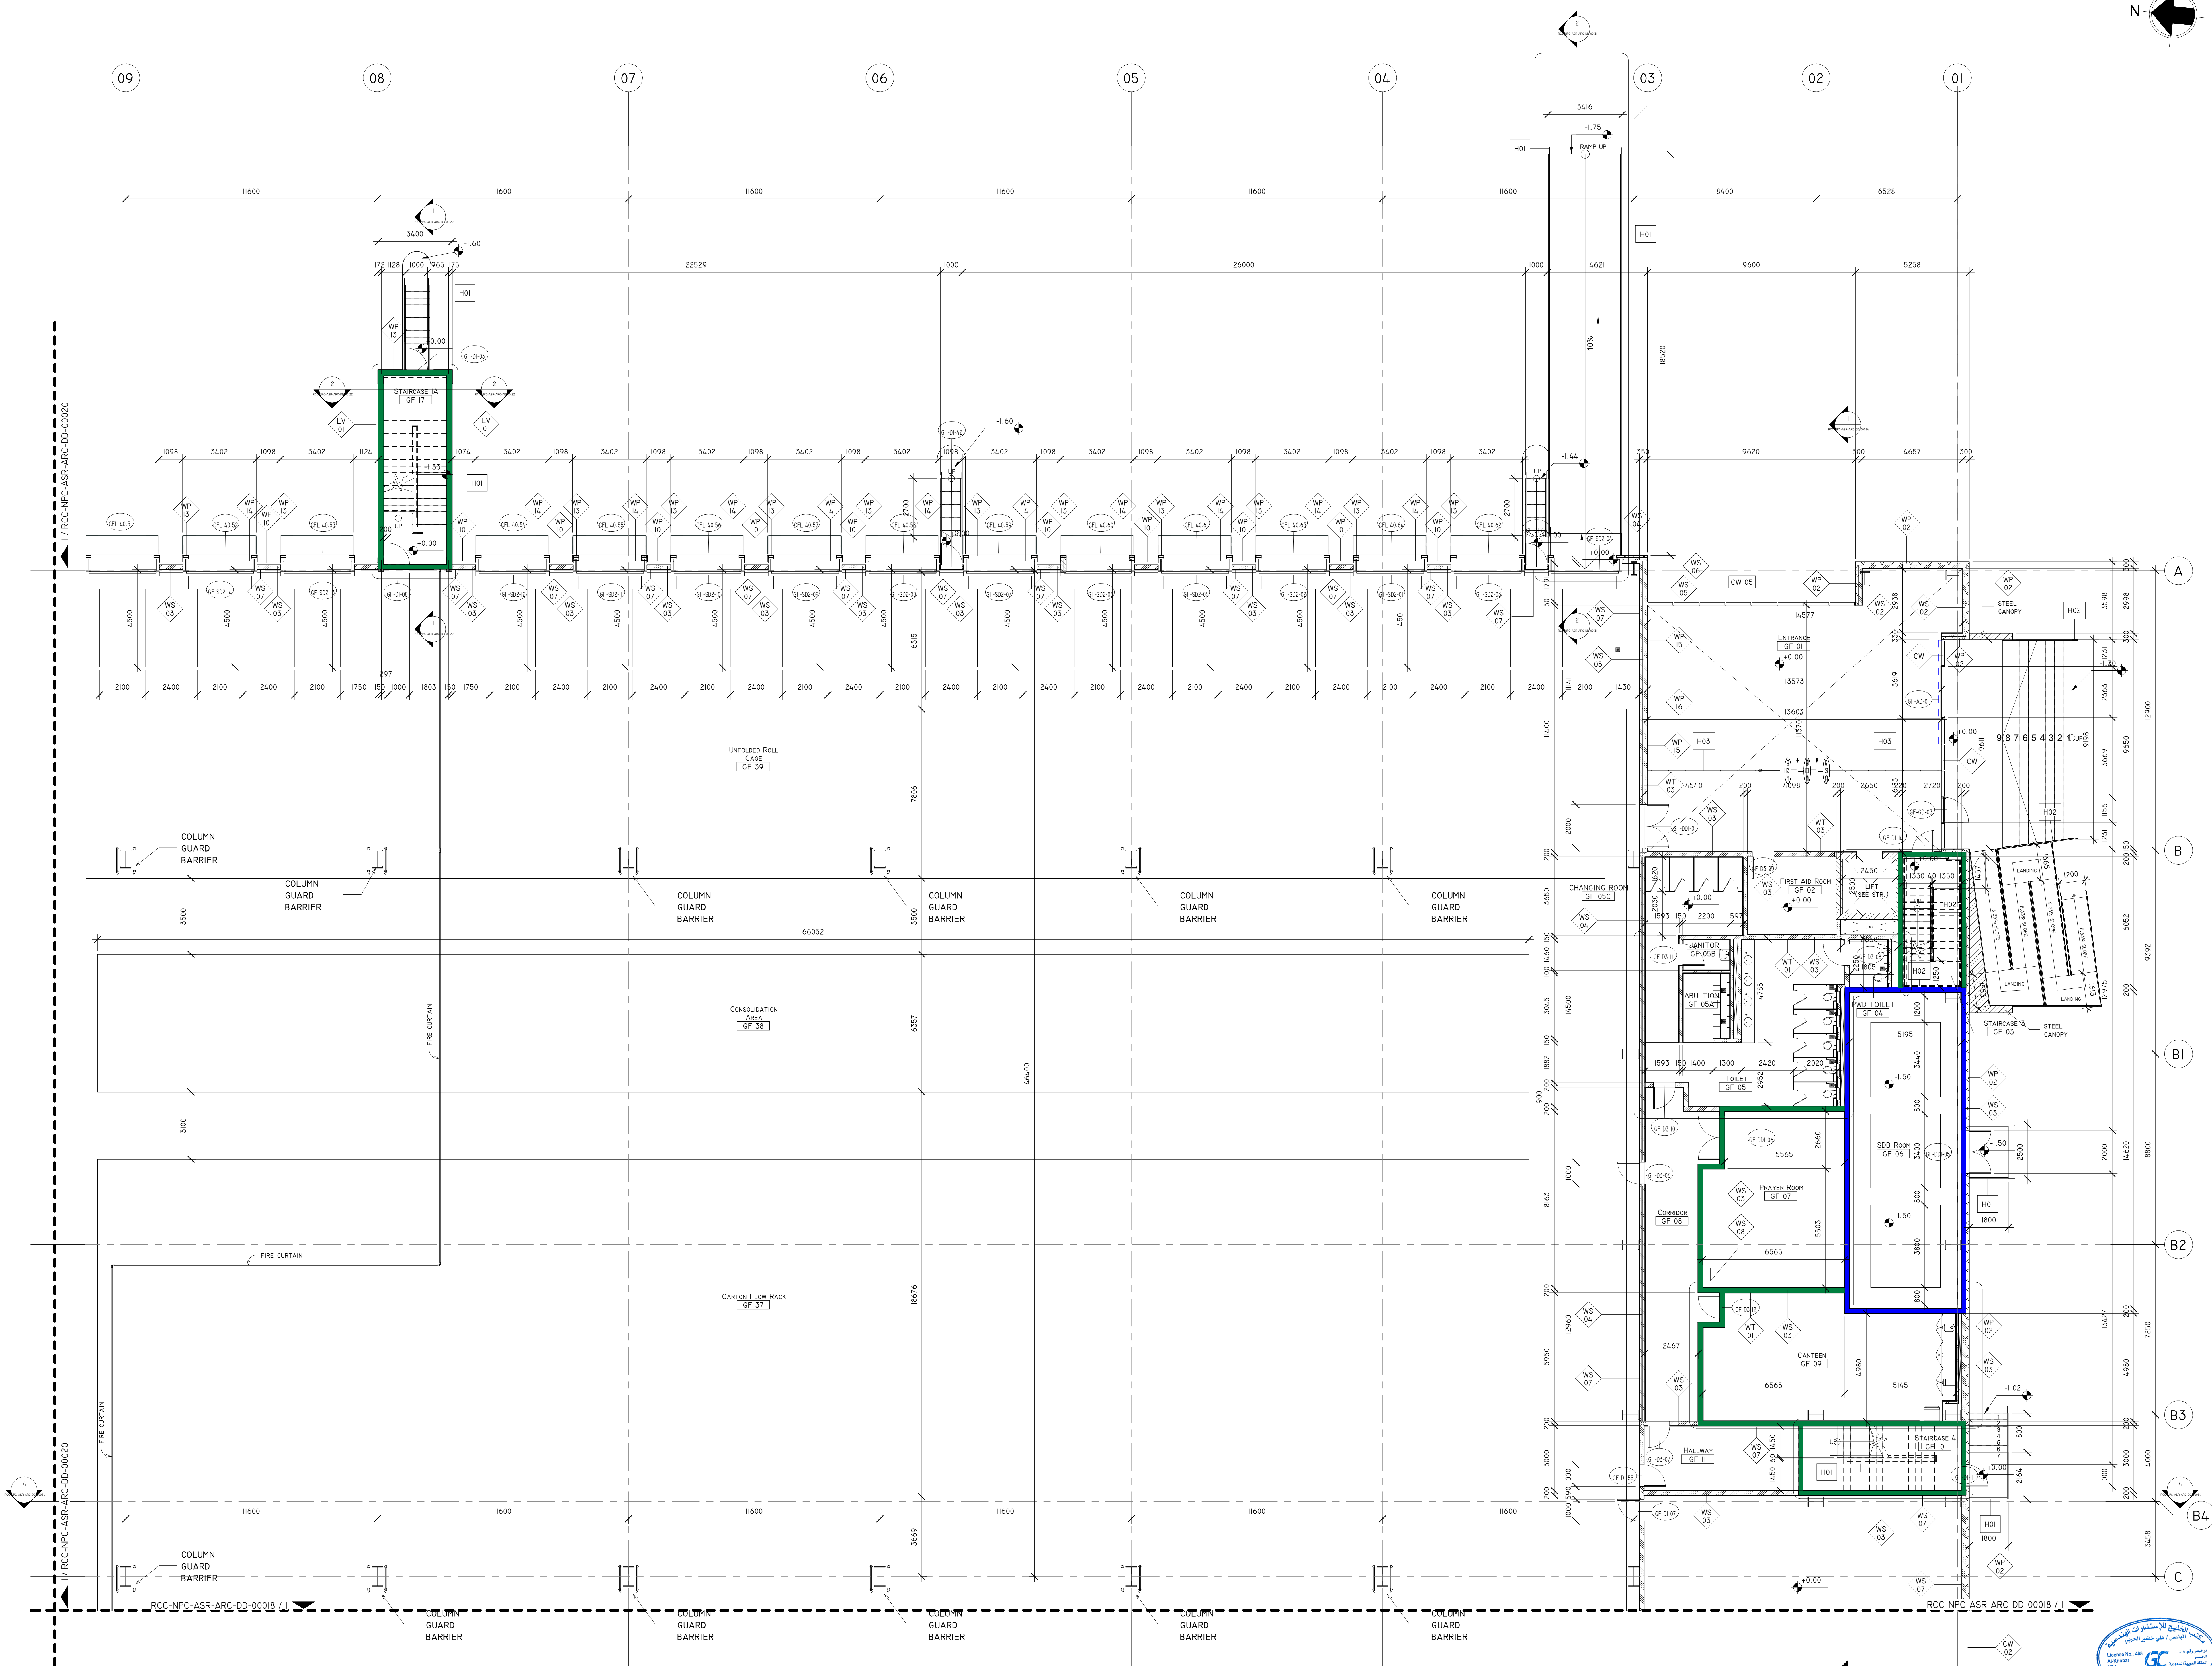

01- GROUND FLOOR GENERAL LAYOUT - PART A
1 : 100



نوبكو
nupco

NOTES & LEGENDS:

1. ALL DIMENSIONS ARE IN MILLIMETERS AND ALL LEVELS GIVEN IN METERS UNLESS OTHERWISE NOTED.

2. FINISHED FLOOR AND ELEVATION - F.F.L. +0.00 METERS SHOWN IN THIS DRAWING IS EQUIVALENT TO F.F.L. +0.00 AS REFERRED TO SITE GRADING LAYOUT DWG NO. RCC-NPC-ASR-CW-DD-0001.

3. THIS DRAWING SHALL BE READ IN CONJUNCTION WITH RELEVANT ELECTRICAL, MECHANICAL, TELECOM AND STRUCTURAL DRAWINGS.

4. CONTRACTOR SHALL BE RESPONSIBLE FOR VERIFYING ALL DIMENSIONS AND CONDITIONS AT SITE PRIOR TO THE START OF CONSTRUCTION. ANY DISCREPANCY SHOULD BE BROUGHT TO THE ATTENTION OF THE CLIENT FOR CLARIFICATION BEFORE PROCEEDING WITH THE AFFECTED PART OF WORK.

0 COLUMN GRID

00 SPOT ELEVATION

00 WALLFINISH TYPE

00 DOOR TAGS

00 ROOM NAME & NUMBER

00 ROOM NAME & NUMBER

WALLS LEGEND

REF DESCRIPTION

LV 01 CURTAIN LOUVER PARTITION

LV 02 CURTAIN LOUVER PARTITION

WP 03 EXTERIOR WALL PANEL SYSTEM 150MM THICK - COLOR WHITE

WP 03 EXTERIOR WALL PANEL SYSTEM 150MM THICK - COLOR BLUE

WP 04 INTERIOR PREPARED WALL PANEL SYSTEM 150MM THICK

WP 05 WALL PANEL SYSTEM 150MM THICK FOR STAGING AREA

WP 06 WALL PANEL SYSTEM 150MM THICK FOR STAGING AREA

WP 07 UN-INSULATED WALL PANEL SYSTEM 150MM THICK

WP 08 SOLID POLYMER FABRICATION RESIN TOILET COMPARTMENTS

WP 09 CLADDING 40MM THICK

WP 10 WALL PANEL SYSTEM 150MM THICK FOR CHILLED & FREEZER ROOMS

WP 11 EXTERIOR WALL PANEL SYSTEM 150MM THICK - COLOR WHITE

WP 12 COMPOSITE PANEL CLADDING 20MM THICK

WP 13 20MM HDP WOOD CLADDING VENEERED INCLUDING GROOVES EVERY 50 MM

WP 14 GREEN WALL

WS 01 CONCRETE MASONRY UNIT WALL (UNIT: 400X200, 150MM THICK)

WS 02 CONCRETE MASONRY UNIT WALL (UNIT: 400X200, 150MM THICK)

WS 03 CONCRETE MASONRY UNIT WALL (UNIT: 400X200, 200MM THICK)

WS 04 CONCRETE MASONRY UNIT WALL (UNIT: 400X200, 150MM THICK)

WS 05 CONCRETE MASONRY UNIT WALL (UNIT: 400X200, 150MM THICK)

WS 06 20MM HDP WOOD CLADDING VENEERED INCLUDING GROOVES EVERY 50 MM

WS 07 20MM THICK SAND CEMENT PLASTER TO EXTERNAL WALLS INCLUDING EXTERNAL PAINT

WS 08 20MM THICK SAND CEMENT PLASTER TO INTERNAL WALLS WITH WASHABLE OIL PAINT

WS 09 20MM THICK SAND CEMENT PLASTER TO INTERNAL WALLS INCLUDING EMULSION PAINT

WS 10 20MM THICK INSULATED GYPSUM DRYWALL CLADDING

WS 11 20MM THICK INSULATED GYPSUM DRYWALL CLADDING

WT 01 PORCELAIN TILE 150X75MM GLUE FIXED TO PLASTERED WALL

WT 02 150X75MM MARBLE TILE MECHANICAL FIXED

HANDRAIL LEGEND

REF DESCRIPTION

H01 100MM GALVANIZED STEEL HANDRAIL - EPOXY PAINTED

H02 100MM STAINLESS STEEL HANDRAIL

H03 100MM STAINLESS STEEL HANDRAIL WITH GLASS

KEY PLAN :

00 29/06/2025 ISSUE FOR DETAILED DESIGN

01 02/07/2025 ISSUE FOR DETAILED DESIGN

02 12/07/2025 ISSUE FOR DETAILED DESIGN

REV. DATE DESCRIPTION OF REVISION

SEAL & SIGNATURE:

DRAWN BY: AHM

CHECKED BY: ZYD

DATE (DD.MM.YYYY): 11.06.2025

NUPCO WAREHOUSE ASER, KSA

CLIENT:

PROJECT MANAGER: جسارة Jasara

PROJECT PROGRAM MANAGER: شركة الرامسات للمقاولات Al Ramsat contracting company

ARCHITECTURE & ENGINEERING CONSULTANT: GULF CONSULT ARCHITECTS & ENGINEERS

PHASE & DISCIPLINE: DETAIL DESIGN ARCHITECTURE

DRAWING TITLE: GROUND FLOOR PLAN - PART A

PROJECT NO: 102

DRAWING NUMBER: RCC-NPC-ASR-ARC-DD-00017

REV: 02