


THIS DRAWING AND THE DESIGN IT COVERS ARE THE PROPERTY OF GULF CONSULT. ARCHITECTS AND ENGINEERS THE USER SHALL NOT REPRODUCE, COPY, SHARE, ENHANCE, NOR USE EXCEPT IN A LIMITED WAY AND PRIVATE USE PERMITTED BY WRITTEN CONSENT GIVEN BY THE CONSULTANT.

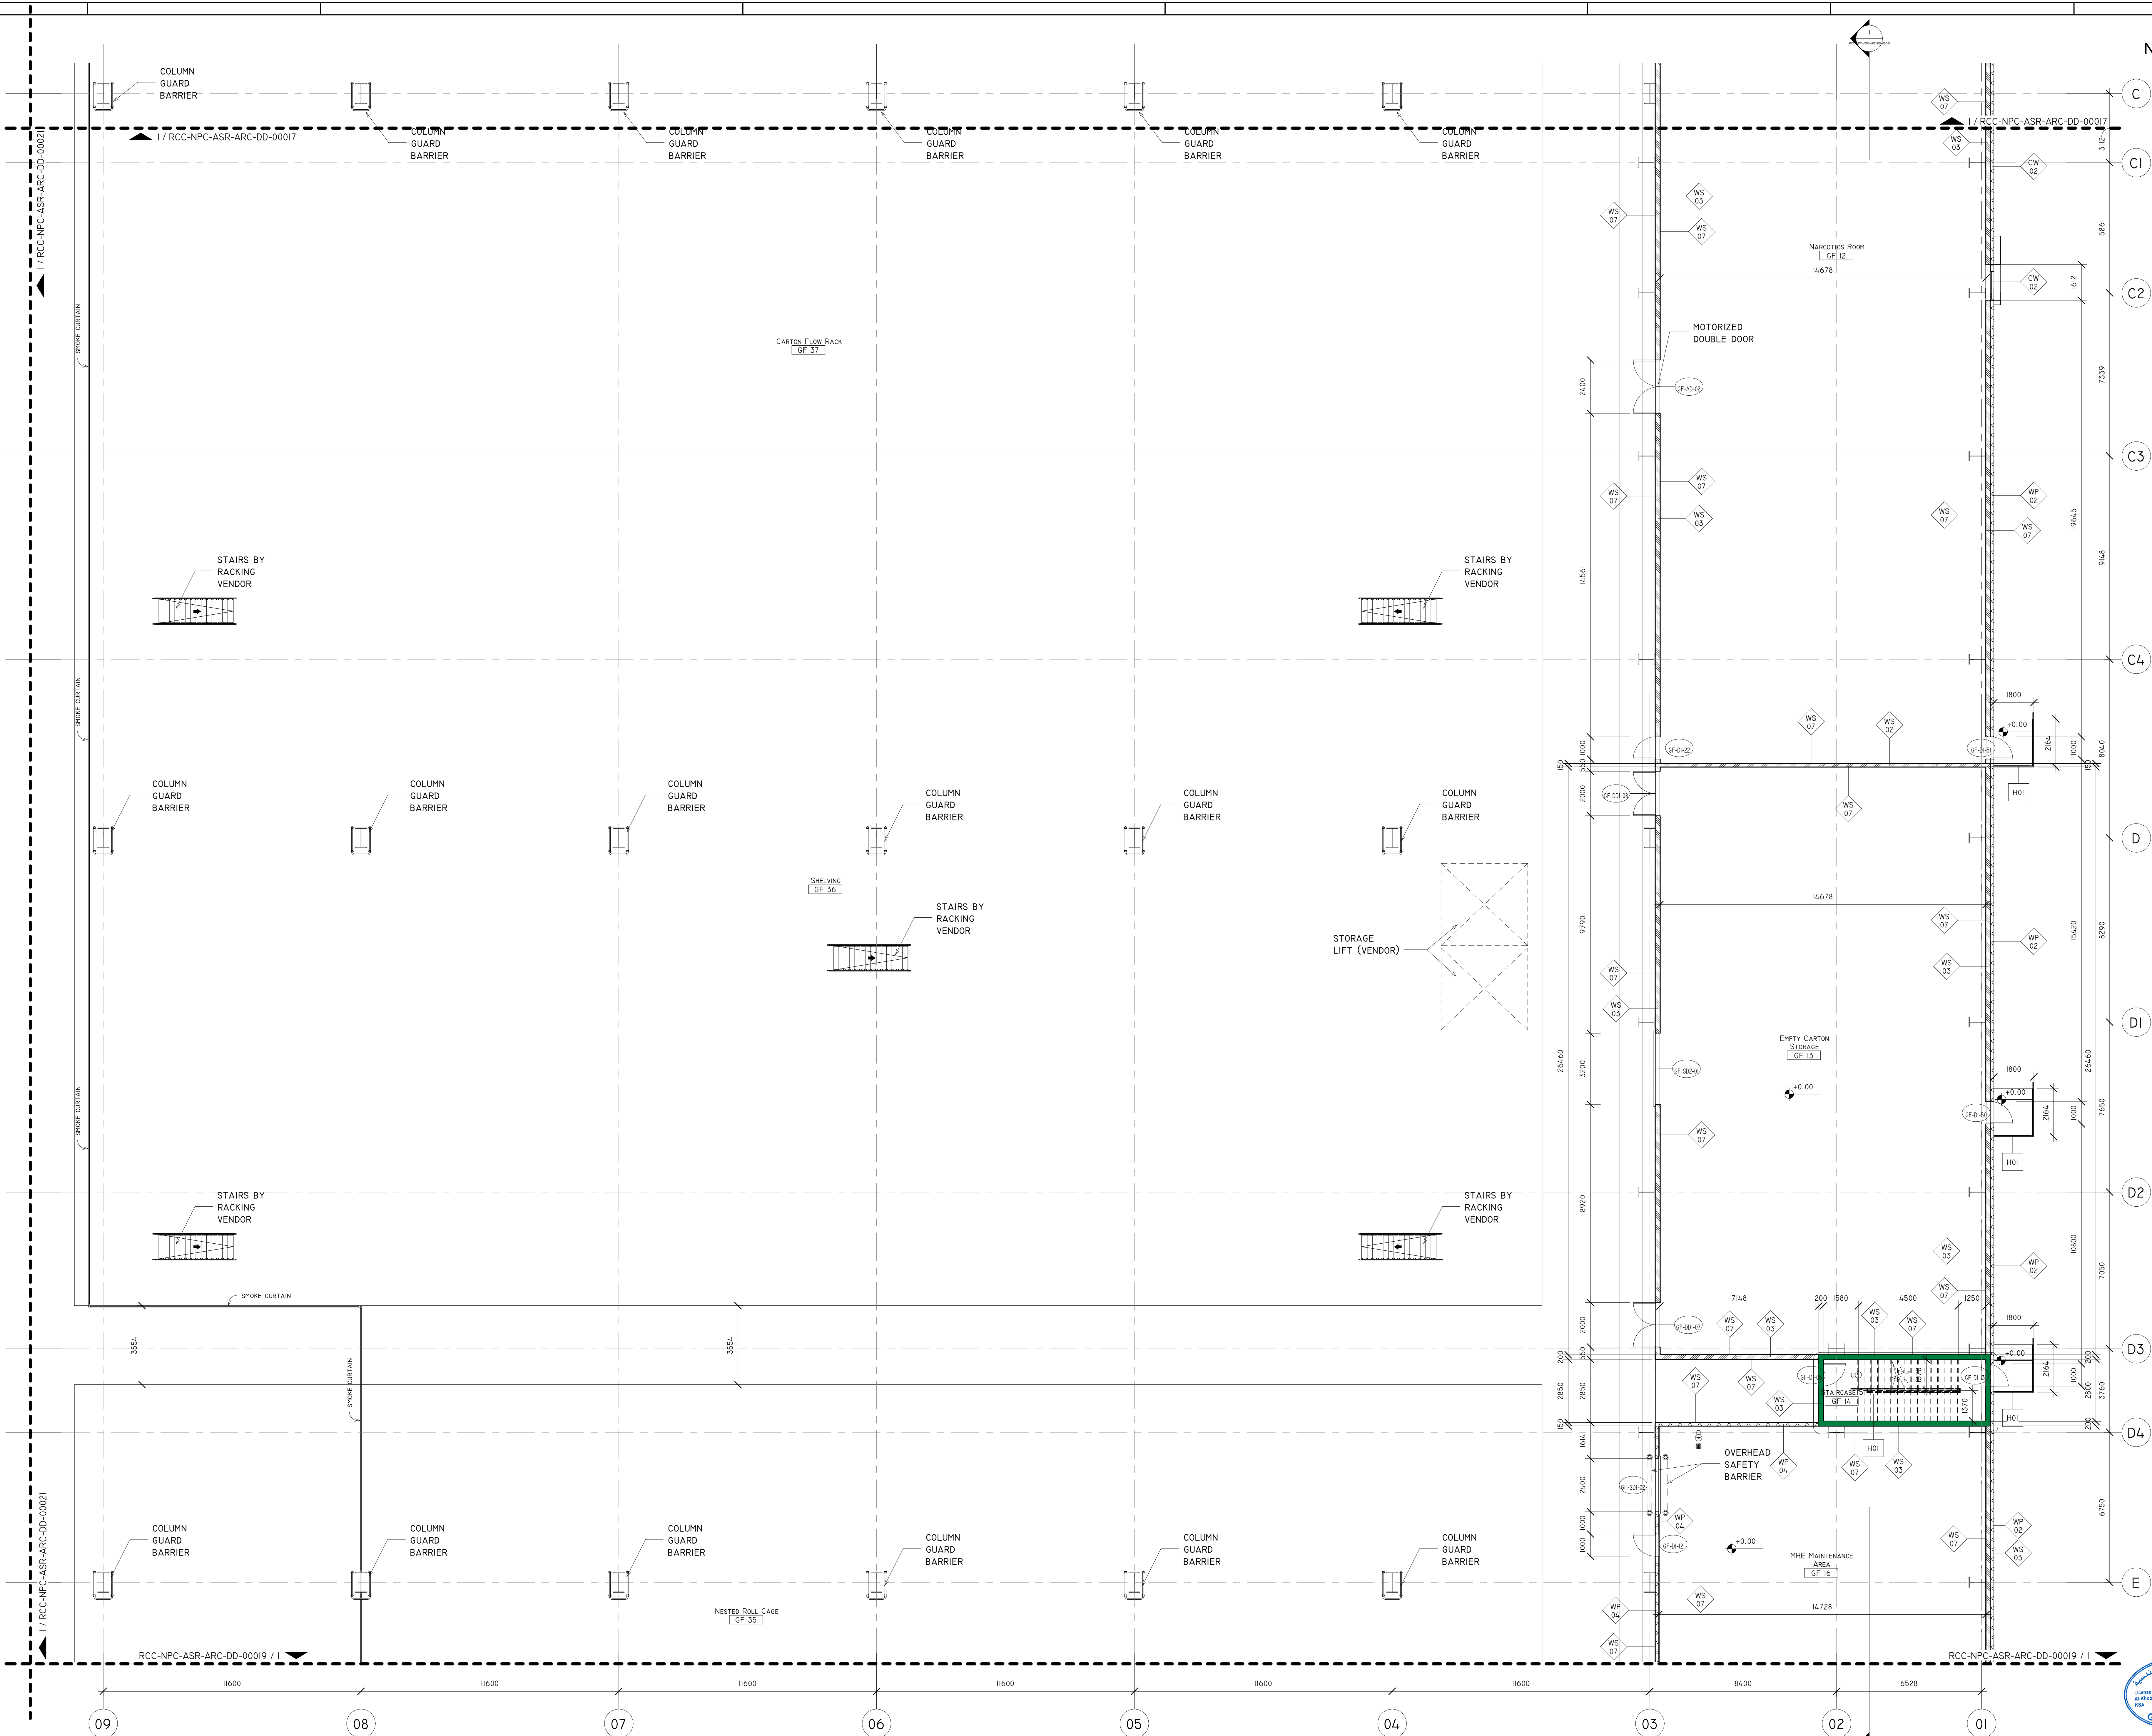

I 01- GROUND FLOOR GENERAL LAYOUT - PART B
1 : 100



NOTES & LEGENDS:

1. ALL DIMENSIONS ARE IN MILLIMETERS AND ALL LEVELS GIVEN IN METERS UNLESS OTHERWISE NOTED.

2. FINISHED FLOOR AND ELEVATION: F.F.L. +0.00 METERS SHOWN IN THIS DRAWING IS EQUIVALENT TO P.L. +0.00 METERS AS REFERENCED TO SITE GRADING LAYOUT DWG NO. RCC-NPC-ASR-CW-DD-0001.

3. THIS DRAWING SHALL BE READ IN CONJUNCTION WITH RELEVANT ELECTRICAL, MECHANICAL, TELECOM AND STRUCTURAL DRAWINGS.

4. CONTRACTOR SHALL BE RESPONSIBLE FOR OBTAINING ALL NECESSARY PERMITS PRIOR TO THE START OF CONSTRUCTION. ANY DISCREPANCY SHOULD BE BROUGHT TO THE ATTENTION OF THE CLIENT FOR CLARIFICATION BEFORE PROCEEDING WITH THE AFFECTED PART OF WORK.

0 COLUMN GRID

10-015 ELEVATION REFERENCE

REF SECTION REFERENCE

00 SPOT ELEVATION

11 A 11 WALLFINISH TYPE

XX YY A ZZ DOOR TAGS

XX YY A ZZ ROOM NAME & NUMBER

01 AIR FIVE RATED WALLS REFER ARCHITECTURE DRAWINGS FOR WALL TYPE

02 AIR FIVE RATED WALLS REFER ARCHITECTURE DRAWINGS FOR WALL TYPE

WALLS LEGEND

REF	DESCRIPTION
LV 01	CURTAIN LOUVER PARTITION
LV 02	CURTAIN LOUVER PARTITION
WP 03	EXTERIOR WALL PANEL SYSTEM 150MM THICK - COLOR WHITE
WP 04	EXTERIOR WALL PANEL SYSTEM 150MM THICK - COLOR BLUE
WP 05	WALL PANEL SYSTEM 150MM THICK FOR STAGING AREA
WP 06	WALL PANEL SYSTEM 150MM THICK FOR STAGING AREA
WP 07	DR-INSULATED WALL PANEL SYSTEM 150MM THICK
WP 08	SOLID POLYMER FABRICATION RESIN TOILET COMPARTMENTS
WP 09	ASB CLADDING 4MM THICK
WP 10	WALL PANEL SYSTEM 150MM THICK FOR CHILLED & FREEZER ROOMS
WP 11	EXTERIOR WALL PANEL SYSTEM 150MM THICK - COLOR WHITE
WP 12	COMPOSITE PANEL CLADDING 20MM THICK
WP 13	20MM HDF WOOD CLADDING VENEERED INCLUDING GROOVES EVERY 50 MM
WP 14	GREEN WALL
WS 01	CONCRETE MASONRY UNIT WALL (UNIT: 400X200, 100MM THICK)
WS 02	CONCRETE MASONRY UNIT WALL (UNIT: 400X200, 150MM THICK)
WS 03	CONCRETE MASONRY UNIT WALL (UNIT: 400X200, 200MM THICK)
WS 04	CONCRETE MASONRY UNIT WALL (UNIT: 400X200, 100MM THICK)
WS 05	CONCRETE MASONRY UNIT WALL (UNIT: 400X200, 150MM THICK)
WS 06	20MM THICK SAND CEMENT PLASTER TO EXTERNAL WALLS INCLUDING EXTERNAL PAINT
WS 07	20MM THICK SAND CEMENT PLASTER TO INTERNAL WALLS WITH WASHABLE OIL PAINT
WS 08	20MM THICK SAND CEMENT PLASTER TO INTERNAL WALLS INCLUDING EMULSION PAINT
WS 09	20MM THICK INSULATED TWO LAYERS OF GYPSUM BOARD FROM EACH SIDE - WALL PARTITIONING
WS 10	20MM THICK INSULATED GYPSUM DRYWALL CLADDING INCLUDING ROCKWOOL INSULATION
WS 11	20MM THICK INSULATED GYPSUM DRYWALL CLADDING
WS 12	20MM THICK INSULATED GYPSUM DRYWALL CLADDING
WS 13	20MM THICK INSULATED CEMENT BOARD WALL PARTITIONS ABOVE CURTAIN WALLS INCLUDING STEEL STRUCTURE & ROCK WOOL INSULATION
WS 14	20MM THICK INSULATED GYPSUM BOARD WALL PANELS
WT 01	PORCELAIN TILE 150X75MM GLUE FIXED TO PLASTERED WALL
WT 02	150X150MM MARBLE TILE MECHANICAL FIXED

HANDRAIL LEGEND

REF	DESCRIPTION
H01	1000MM GALVANIZED STEEL HANDRAIL - EPOXY PAINTED
H02	1000MM STAINLESS STEEL HANDRAIL
H03	1000MM STAINLESS STEEL HANDRAIL WITH GLASS

KEY PLAN :

REV	DATE	DESCRIPTION OF REVISION
00	29/06/2025	ISSUE FOR DETAILED DESIGN
01	02/07/2025	ISSUE FOR DETAILED DESIGN
02	12/07/2025	ISSUE FOR DETAILED DESIGN

SEAL & SIGNATURE:

DRAWN BY	CHECKED BY	DATE (DD.MM.YYYY)
AHM	ZYD	11.06.2025

NUPCO WAREHOUSE
ASEER, KSA

CLIENT:

PROJECT MANAGER:

PROJECT PROGRAM MANAGER:

ARCHITECTURE & ENGINEERING CONSULTANT:

PHASE & DISCIPLINE:

DETAIL DESIGN
ARCHITECTURE

DRAWING TITLE:

GROUND FLOOR PLAN - PART B

PROJECT NO.	DRAWING NUMBER	REV
102	RCC-NPC-ASR-ARC-DD-00018	02

SCALE (A0)
1 : 100