

- GLASS SPECS
- ALL GLAZING ON FACADE SHALL BE DOUBLE GLAZING OF THE FOLLOWING COMPOSITION:
 - 8MM CLEAR TEMPERED GLASS
 - 12MM AIR SPACE
 - 6MM CLEAR TEMPERED GLASS
 - GLASS COLOR SHALL BE BLUE GLASS SIMILAR TO NUPCO BLUE. TYPE AND SAMPLE SUBJECT TO APPROVAL OF THE CLIENT
 - ALL SPANDRILL GLASS GLASS PANEL SHALL BE DOUBLE GLAZING SAME AS MAIN GLASS BUT WITH OPAQUE FIL FROM INSIDE



NOTES & LEGENDS:

1. ALL DIMENSIONS ARE IN MILLIMETERS AND ALL LEVELS GIVEN IN METERS UNLESS OTHERWISE NOTED.

2. FINISHED FLOOR AND ELEVATION - F.F.L. +0.00 METERS SHOWN IN THIS DRAWING IS EQUIVALENT TO F.F.L. 2025 SHOWN AS REFERENCED TO SITE GRADING LAYOUT DWG NO. RCC-NPC-ASR-CIV-DD-0005.

3. THIS DRAWING SHALL BE READ IN CONJUNCTION WITH RELEVANT ELECTRICAL, MECHANICAL, TELECOM AND STRUCTURAL DRAWINGS.

4. CONTRACTOR TO VERIFY ALL DIMENSIONS AND CONDITIONS AT SITE PRIOR TO THE START OF CONSTRUCTION. ANY DISCREPANCY SHOULD BE BROUGHT TO THE ATTENTION OF THE CLIENT FOR CLARIFICATION BEFORE PROCEEDING WITH THE AFFECTED PART OF WORK.

5. FINAL RACKING POSITIONS TO BE PROVIDED BY VENDOR.

6. APPROVED FURNITURES TO BE PROVIDED BY AL RAMSAT.

Legend:

0	COLUMN GRID	SPOT ELEVATION
H01	RAILING TYPE	WALL/FRESH TYPE
00		DOOR TAGS

WALLS LEGEND

TYPE	DESCRIPTION
GW 01	GLAZED CURTAIN WALL PANELS
CW 02	ALUMINUM & GLASS PARTITION
LV 03	CURTAIN LOUVER PARTITION
LV 02	CURTAIN LOUVER PARTITION
WP 02	EXTERIOR WALL PANEL SYSTEM 150MM THICK - COLOR WHITE
WP 03	EXTERIOR WALL PANEL SYSTEM 150MM THICK - COLOR BLUE
WP 04	INTERIOR WALL PANEL SYSTEM 150MM THICK
WP 05	INTERIOR WALL PANEL SYSTEM 150MM THICK - HRR FIRE RATED
WP 06	WALL PANEL SYSTEM 150MM THICK FOR STAGING AREA
WP 07	WALL PANEL SYSTEM 150MM THICK FOR STAGING AREA
WP 08	UN-INSULATED WALL PANEL SYSTEM 150MM THICK
WP 09	SOLID POLYMER FABRICATION RESIN TOILET COMPARTMENTS
WP 10	SOLID POLYMER FABRICATION RESIN TOILET COMPARTMENTS
WP 11	SOLID POLYMER FABRICATION RESIN TOILET COMPARTMENTS
WP 12	ACP CLADDING 4MM THICK
WP 13	EXTERIOR WALL PANEL SYSTEM 150MM THICK - COLOR WHITE
WP 14	COMPOSITE PANEL CLADDING 20MM THICK
WP 15	WALL PANEL SYSTEM 150MM THICK FOR CHILLED & FREEZER ROOMS
WP 16	GREEN WALL
WS 01	CONCRETE MASONRY UNIT WALL (UNIT: 400X200; 100MM THICK)
WS 02	CONCRETE MASONRY UNIT WALL (UNIT: 400X200; 100MM THICK)
WS 03	CONCRETE MASONRY UNIT WALL (UNIT: 400X200; 200MM THICK)
WS 04	CONCRETE MASONRY UNIT WALL (UNIT: 400X200; 100MM THICK)
WS 05	CONCRETE MASONRY UNIT WALL (UNIT: 400X200; 200MM THICK)
WS 06	CONCRETE MASONRY UNIT WALL (UNIT: 400X200; 100MM THICK)
WS 07	CONCRETE MASONRY UNIT WALL (UNIT: 400X200; 100MM THICK)
HANDRAIL LEGEND

REF	DESCRIPTION
H01	100MM GALVANIZED STEEL HANDRAIL - EPOXY PAINTED
H02	100MM STAINLESS STEEL HANDRAIL
H03	100MM STAINLESS STEEL HANDRAIL WITH GLASS
H04	100MM STAINLESS STEEL HANDRAIL WALL MOUNTED

KEY PLAN :

REV	DATE	DESCRIPTION
00	30/06/2025	ISSUE FOR DETAILED DESIGN
01	11/08/2025	ISSUE FOR DETAILED DESIGN
02	28/08/2025	ISSUE FOR DETAILED DESIGN

REV. DATE DESCRIPTION OF REVISION

SEAL & SIGNATURE:

DRAWN BY	CHECKED BY	DATE (DD.MM.YYYY)
IBR	ZYD	29.05.2025

NUPCO WAREHOUSE
ASER, KSA

CLIENT:

نوبكو
nupco

PROJECT MANAGER:

جسارة
Jasara

PROJECT PROGRAM MANAGER:

شركة الرامسات للمقاولات
Al Ramsat contracting company

ARCHITECTURE & ENGINEERING CONSULTANT:

GC GULF CONSULT
ARCHITECTS & ENGINEERS


PHASE & DISCIPLINE:

DETAIL DESIGN
ARCHITECTURE


DRAWING TITLE:

NORTH ELEVATION PARTS I & 2

PROJECT NO.	DRAWING NUMBER	REV
102	RCC-NPC-ASR-ARC-DD-00077	02
SCALE (A0)	1 : 100	

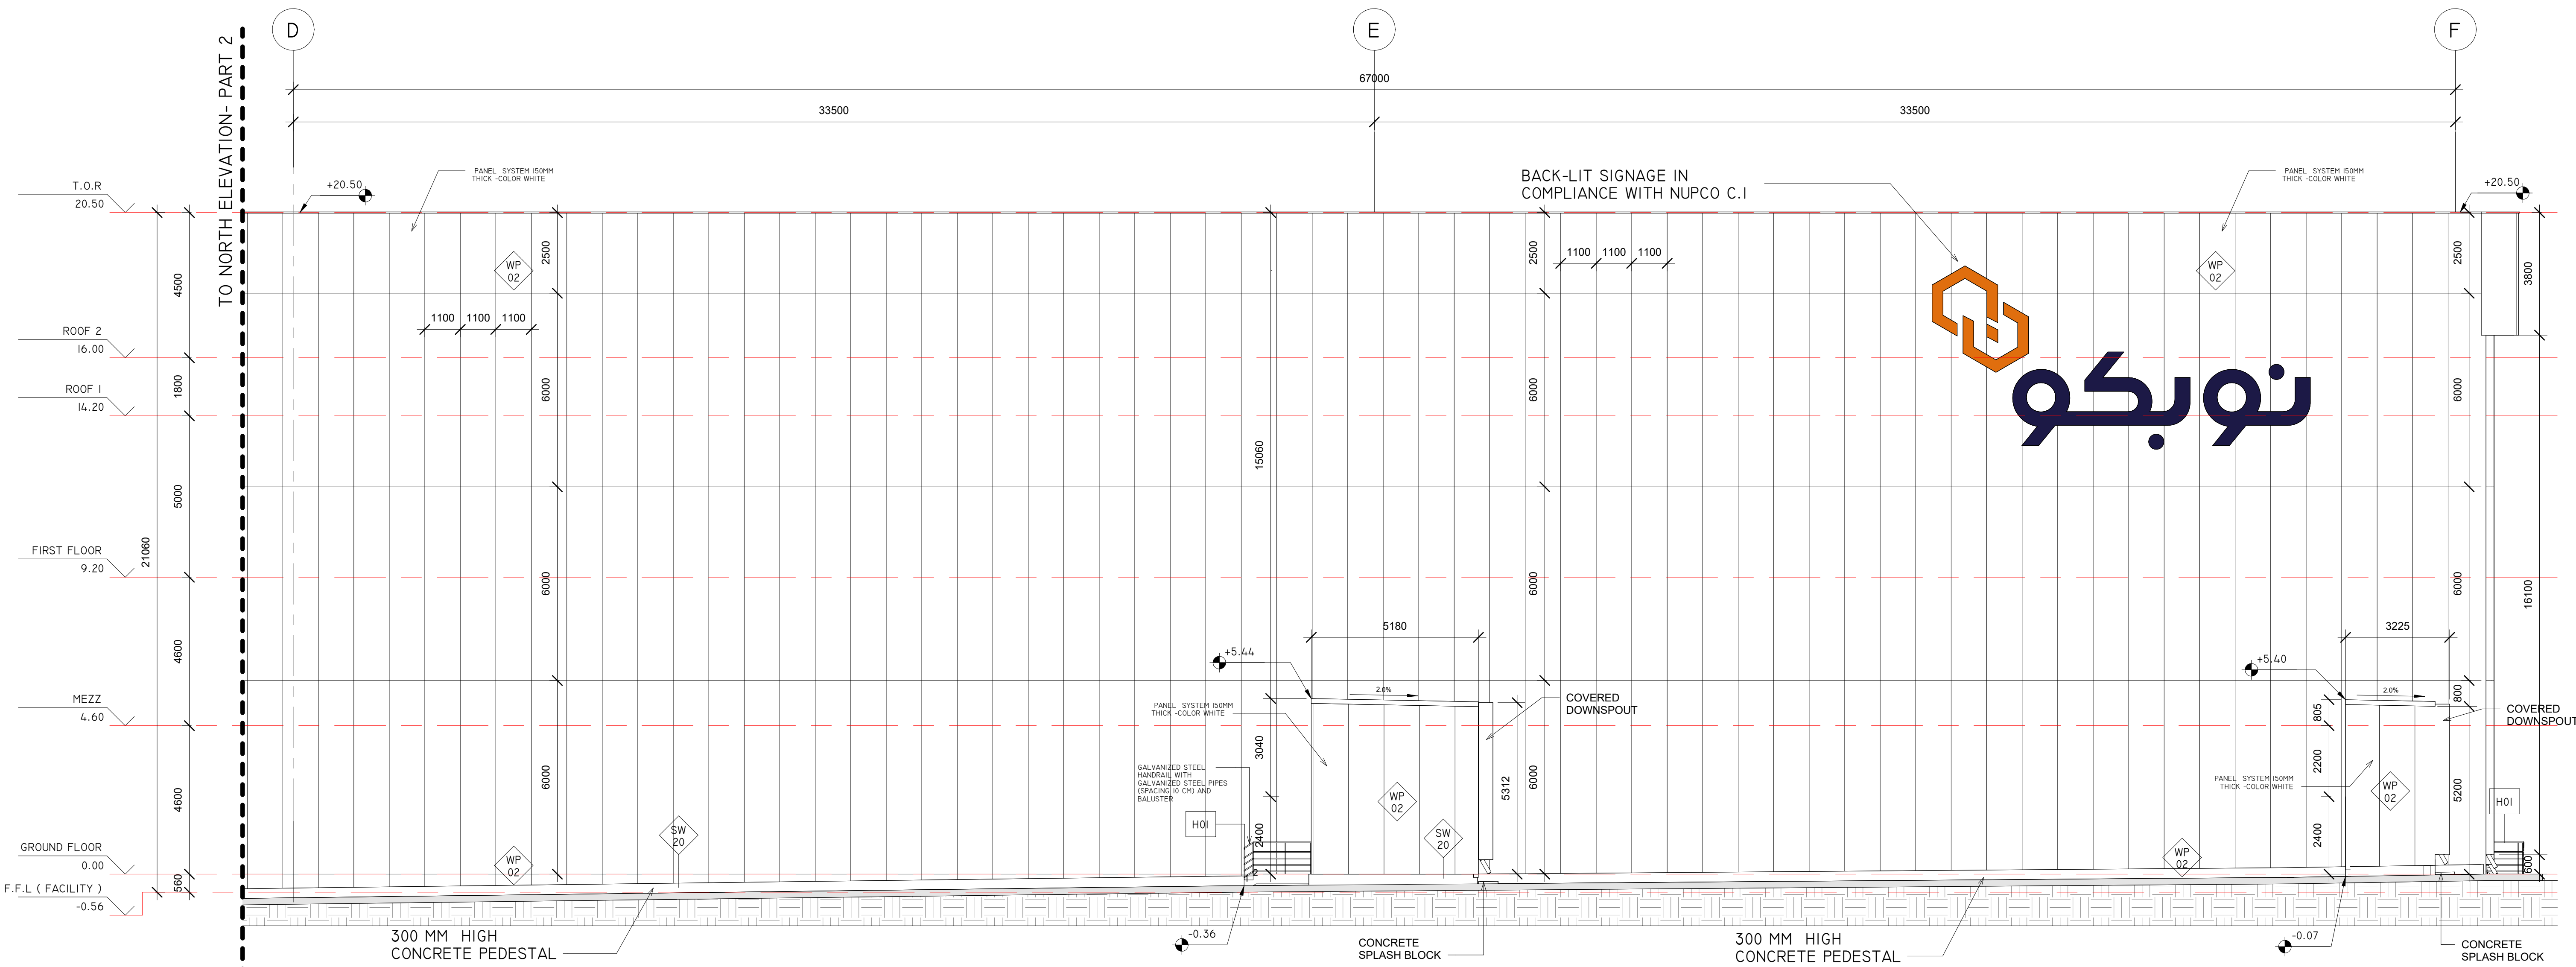

I NORTH ELEVATION- PART I
1 : 100

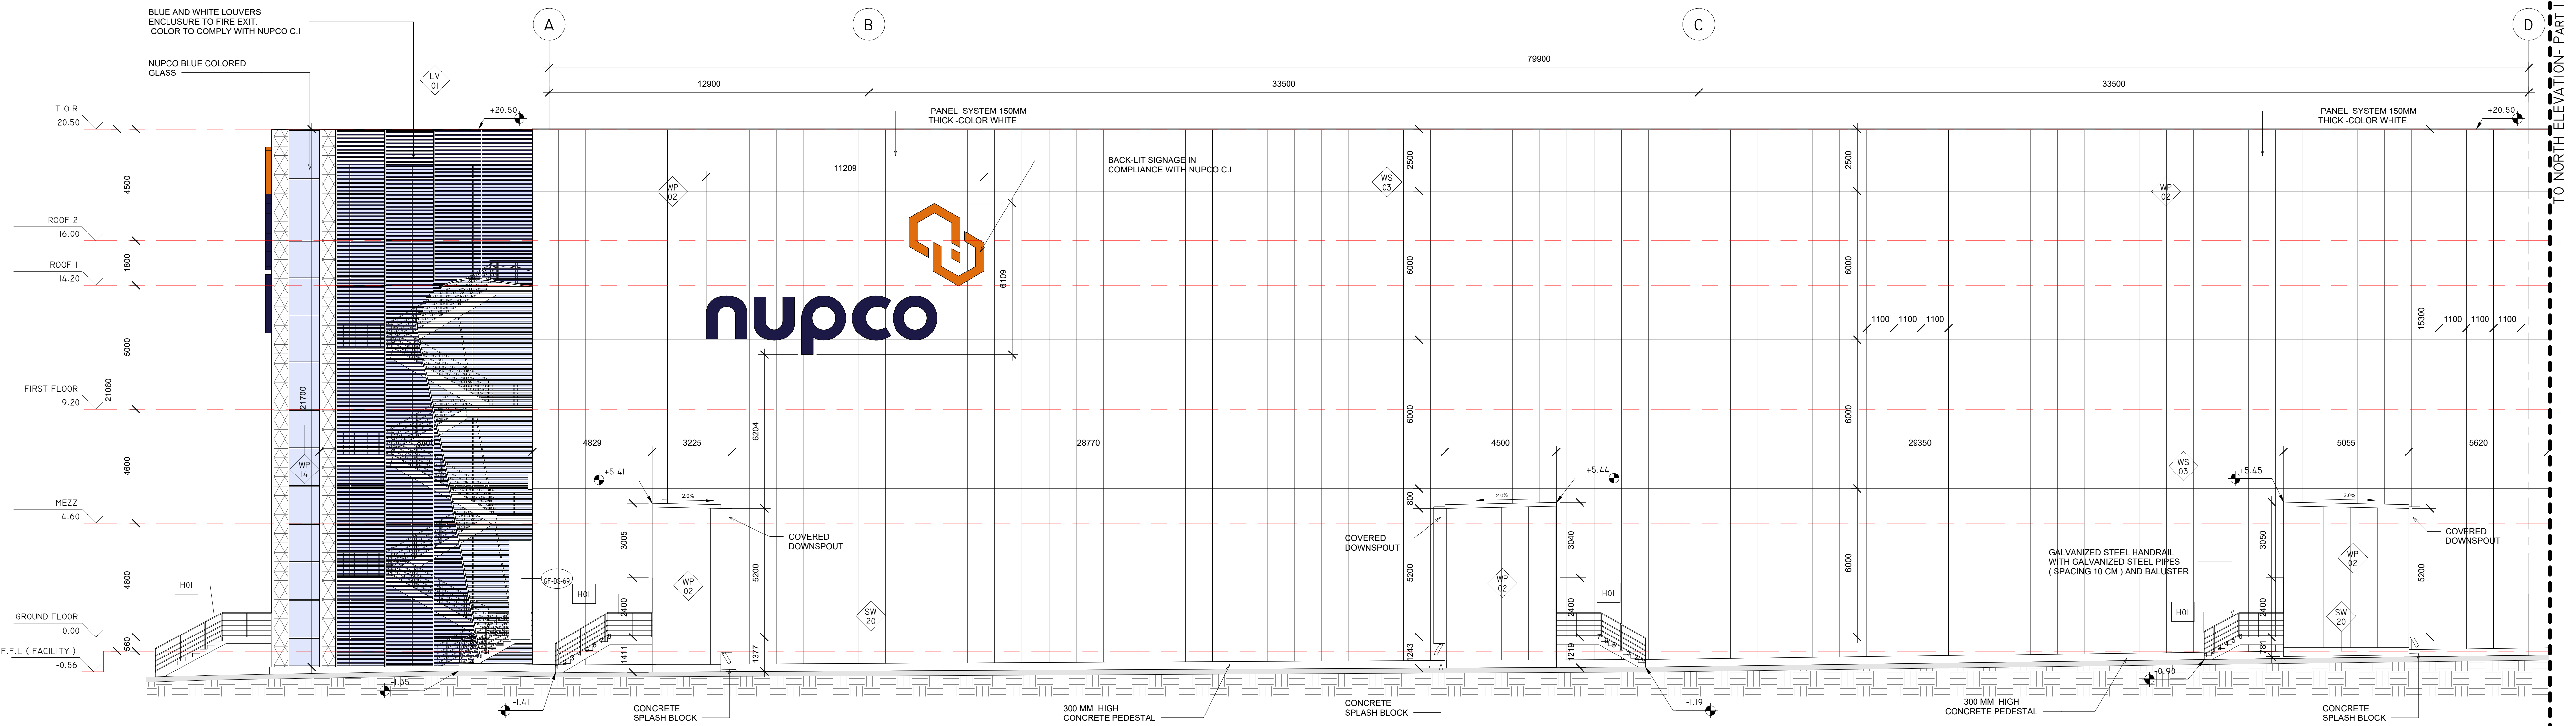

2 NORTH ELEVATION- PART 2
1 : 100